


GENERAL NOTES

1. FOR PLAN & ISOMETRIC VIEW
SEE 15_15229_40
2. FOR FRONT ELEVATION SEE
15_15229_41
3. FOR MATERIAL LIST SEE
19_15229_43

DESCRIPTION		FIRST ISSUE				
REV	A	DATE	15/09/2015	BY	JDH	CHKD OC
						APPD KM

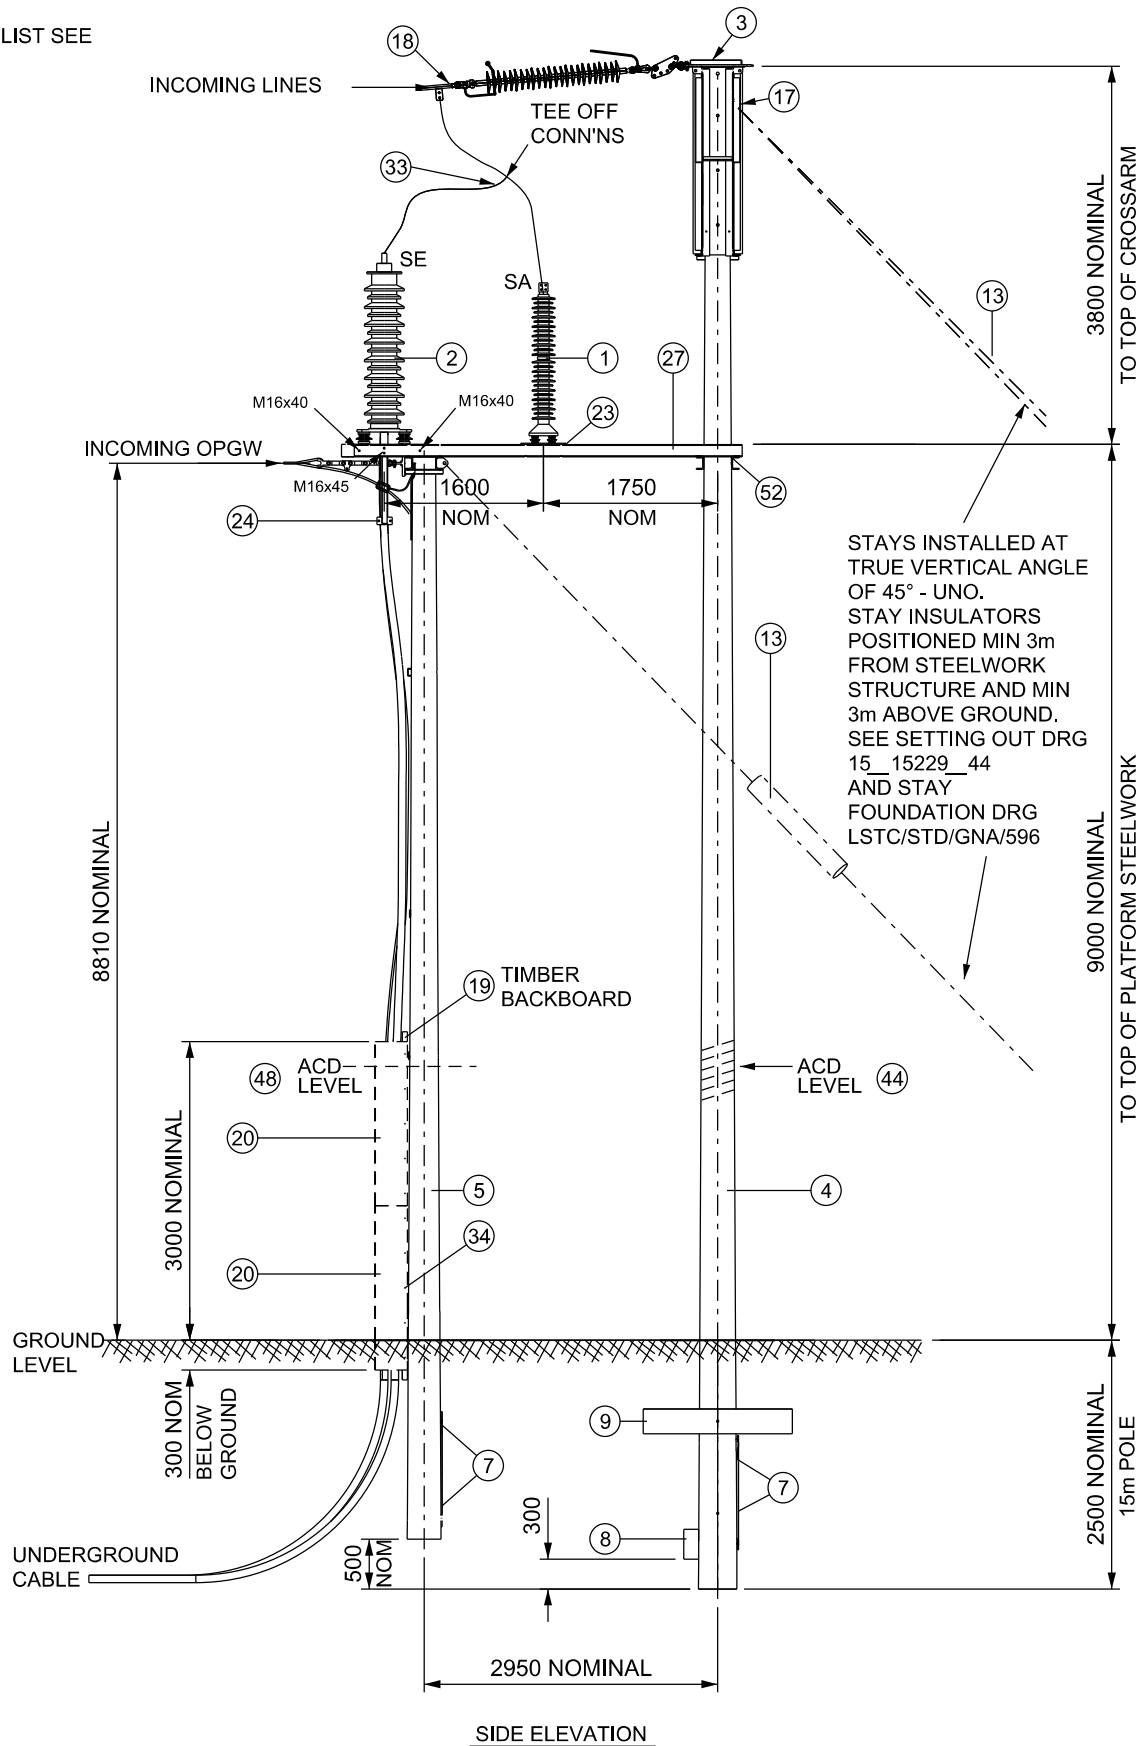

CLIENT	KTL
SPECIFICATION	CUMNOCK - DERSALLOCH ROUTE

TITLE	GA - SIDE ELEVATION 0° ENTRY / TERMINAL 4 POLE STRUCTURE
-------	---

SCALE	1 : 75 (UNLESS OTHERWISE STATED)	ORIGINAL SIZE	A4
DATE	04/08/15	CHECKED	OC
DRAWN	JDH	APPROVED	KM
DRAWING NUMBER	15_15229_42	REV	A

LS TRANSMISSION CONSULTANCY LIMITED Yorkshire House York Road Little Driffield East Yorkshire YO25 5XA 01377 253617
