
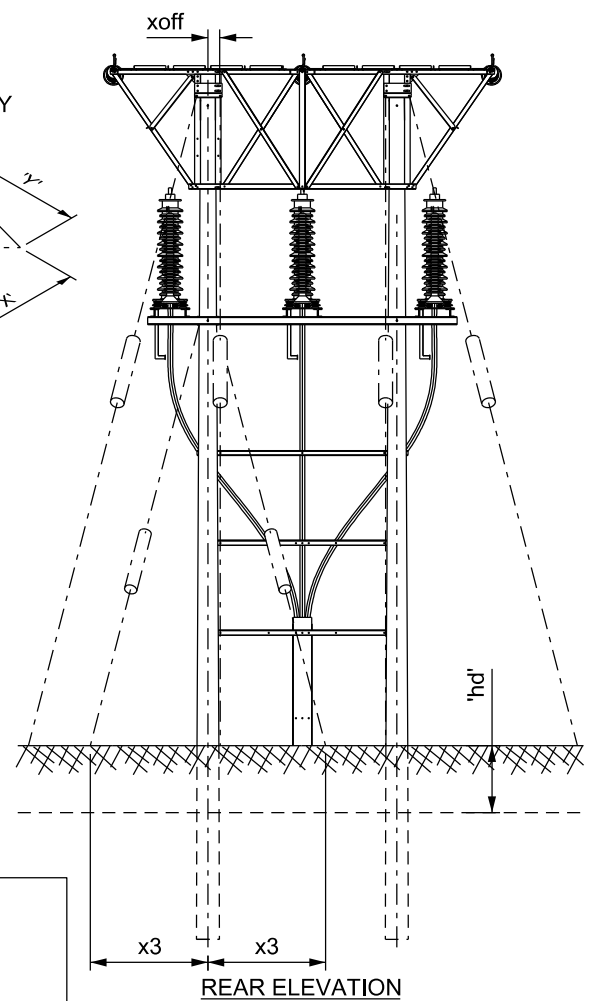


ISOMETRIC VIEW

SHOWING TYPICAL SETTING
OUT DIMENSIONS AND TRUE
VERTICAL STAY ANGLE 'b'


DESCRIPTION		FIRST ISSUE			
REV	DATE	BY	CHKD	APPD	
A	05/08/15	JDH	OC	KM	

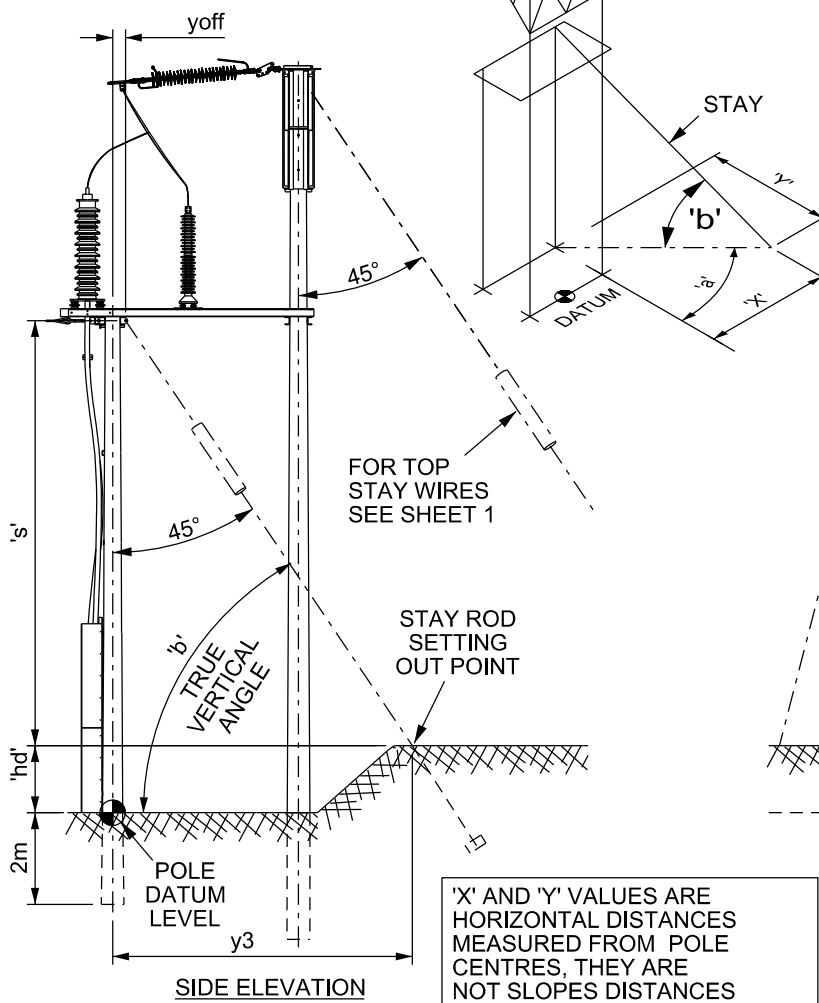

APPROXIMATE GUIDE FOR SETTING OUT
STAY POSITIONS AT VARIOUS GROUND LEVELS

Overall Pole length (m)		11	
Att. Height above ground (m)		9	
Height Difference (hd) (m)		X3 (m)	Y3 (m)
STAY	3	1.74	6.00
LEVEL	2.5	1.87	6.48
ABOVE	2	2.00	6.96
POLE	1.5	2.13	7.44
DATUM	1	2.26	7.93
LEVEL	0.5	2.39	8.41
0		2.52	8.89
0.5	STAY	2.65	9.38
1	LEVEL	2.78	9.86
1.5	BELOW	2.91	10.34
2	POLE	3.04	10.83
2.5	DATUM	3.17	11.31
3	LEVEL	3.30	11.79

True Angle 'b' (deg) =	45	xoff (m) =	0.19
Splay Angle 'a3' (deg) =	15	yoff (m) =	0.2

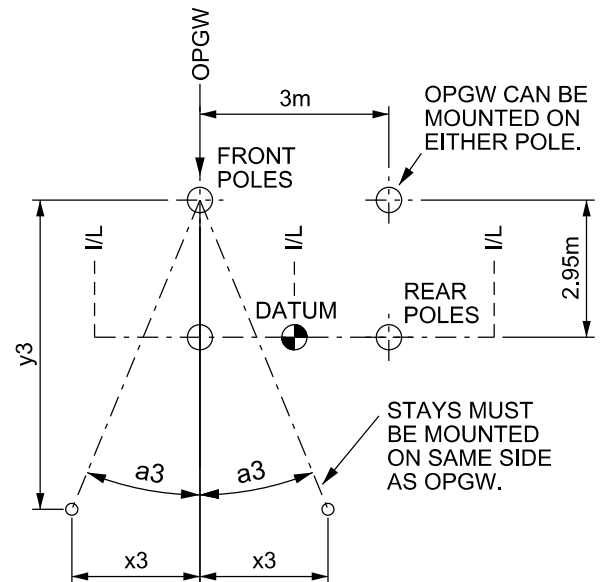

PLAN VIEW SHOWING TOP STAY
SPLAY ANGLES

NOTE:-

- TRUE STAY ANGLE 'b' = 45°
- 'hd' = MEASURED HEIGHT DIFFERENCE BETWEEN POLE G.L. DATUM AND STAY WIRE SETTING OUT POINT, THIS MUST BE DETERMINED FOR EACH STAY LOCATION BEFORE 'X' AND 'Y' SETTING OUT VALUES CAN BE USED.
- SETTING OUT VALUES ARE FOR GUIDANCE ONLY. 'X' AND 'Y' VALUES STATED ARE HORIZONTAL DISTANCES VIEWED FROM ABOVE. TRUE VERTICAL STAY AND SPLAY ANGLES TO BE SITE VERIFIED PRIOR TO INSTALLATION.

$$'x' = 'xoff' + 's' \times (\sin 'a' / \tan 'b')$$

$$'y' = 'yoff' + 's' \times (\cos 'a' / \tan 'b')$$

CLIENT

KTL

PROJECT

CUMNOCK - DERSALLOCH
ROUTE

TITLE

STAY -
SETTING OUT DRAWING
4 POLE TERMINAL
STRUCTURE
(SHEET 2 OF 2)
(OPGW STAYS)

SCALE NTS
(UNLESS OTHERWISE STATED)

DATE 05/08/2015

DRAWN JDH

DRAWING NUMBER 15_15229_44

ORIGINAL SIZE A4

CHECKED OC

APPROVED KM

REV A

LS TRANSMISSION CONSULTANCY LIMITED

Yorkshire House
York Road
Little Driffield
East Yorkshire
YO25 5XA
01377 253617