


DESCRIPTION		FIRST ISSUE			
REV	DATE	BY	CHKD	APPD	
A	14/09/15	JDH	OC	KM	

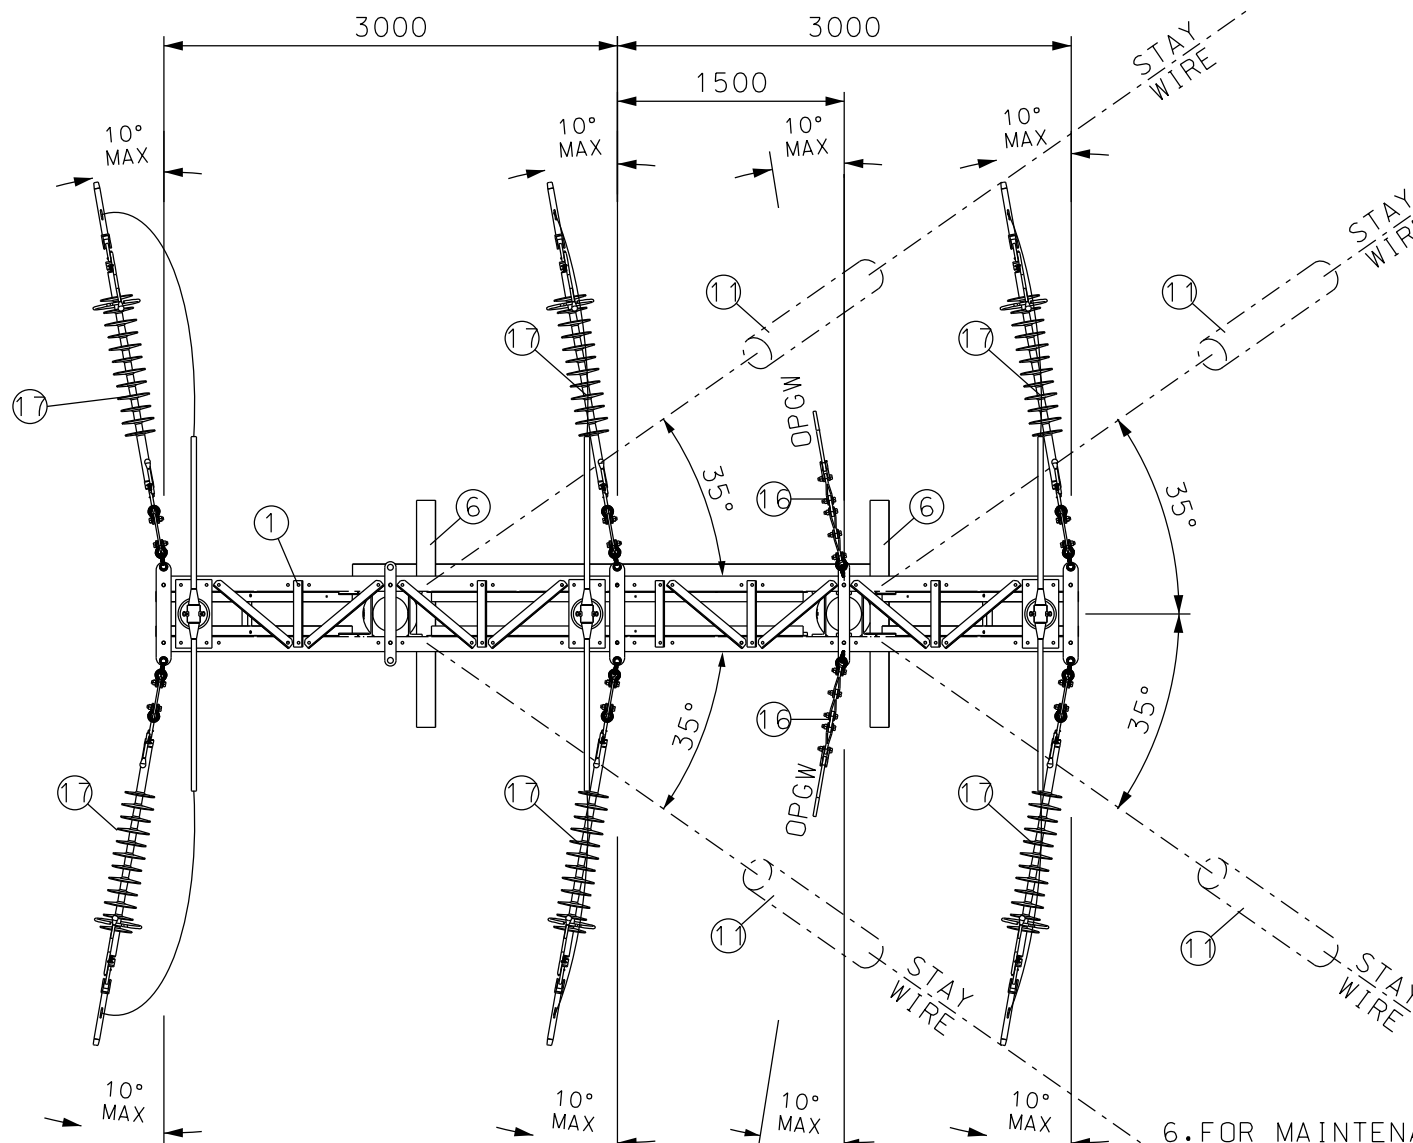

GENERAL NOTES:

1. ALL STEELWORK TO BE PROTOTYPE CHECK ERECTED BEFORE MASS PRODUCTION.
2. SAFETY SIGNS TO BE INSTALLED TO CONFORM TO POWER SYSTEMS PROCEDURES
- 3.FOR FRONT ELEVATION SEE 15_15229_52
- 4.FOR MATERIAL LIST SEE 19_15229_54
- 5.FOR STAY WIRE SETTING OUT DETAILS SEE 15_15229_56.

- 6.FOR MAINTENANCE ATTACHMENT LOCATIONS SEE LSTC/STD/GNA/551.
7. OPGW TO BE INSTALLED ON THE SAME SIDE OF STRUCTURES THROUGHOUT. NO CROSSING OF OPGW AND PHASE CONDUCTORS PERMITTED.

GENERAL NOTES:	CLIENT	TITLE	SCALE	1:50	ORIGINAL SIZE	A4	LS TRANSMISSION CONSULTANCY LIMITED Yorkshire House York Road Little Driffield East Yorkshire YO25 5XA 01377 253617
			(UNLESS OTHERWISE STATED)				
			DATE	14/09/2015	CHECKED	OC	
			DRAWN	JDH	APPROVED	KM	
			DRAWING NUMBER	15_15229_53		REV	
	SPECIFICATION		GA - PLAN VIEW 5-20° ANGLE STRUCTURE				
	CUMNOCK - DERSALLOCH ROUTE						