


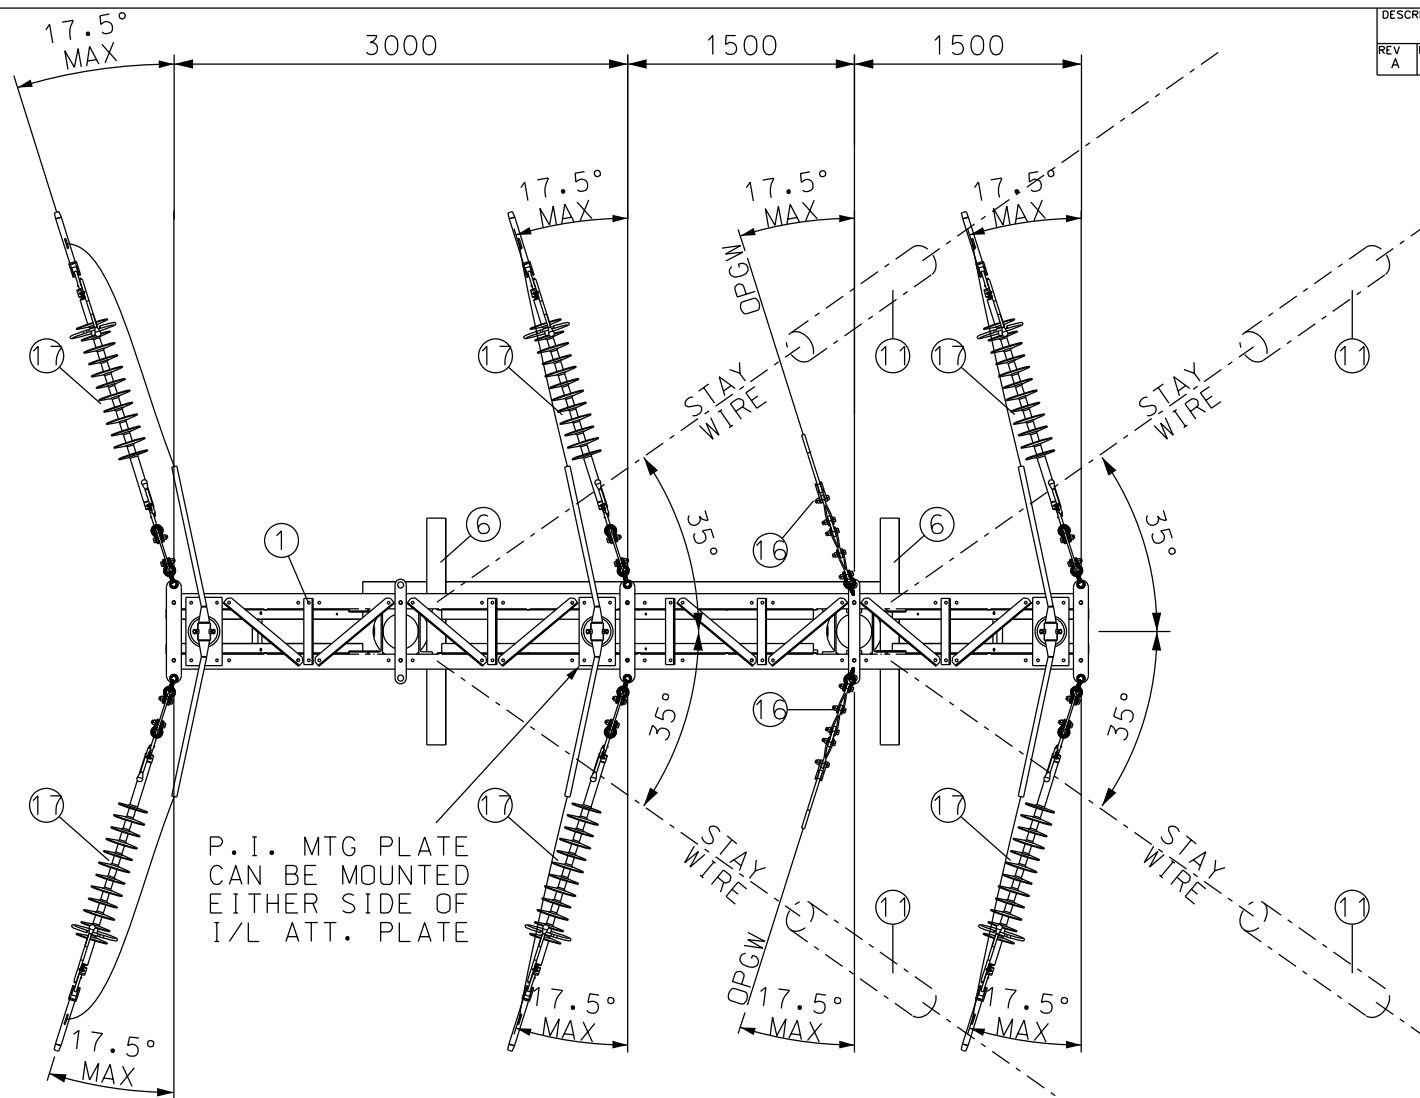

DESCRIPTION		FIRST ISSUE			
REV	DATE	BY	CHKD	APPD	
A	15/09/15	JDH	OC	KM	

GENERAL NOTES:

1. ALL STEELWORK TO BE CHECK ERECTED BEFORE MASS PRODUCTION.
2. SAFETY SIGNS TO BE INSTALLED TO CONFORM TO POWER SYSTEMS PROCEDURES
- 3.FOR FRONT ELEVATION SEE 15_15229_59
- 4.FOR MATERIAL LIST SEE 19_15229_61
- 5.FOR STAY WIRE SETTING OUT DETAILS SEE 15_15229_63.

- 6.FOR MAINTENANCE ATTACHMENT LOCATIONS SEE LSTC/STD/GNA/551.
7. OPGW TO BE INSTALLED ON THE SAME SIDE OF STRUCTURES THROUGHOUT. NO CROSSING OF OPGW AND PHASE CONDUCTORS PERMITTED.

GENERAL NOTES:	CLIENT	TITLE	SCALE	ORIGINAL SIZE	LS TRANSMISSION CONSULTANCY LIMITED Yorkshire House York Road Little Driffield East Yorkshire YO25 5XA 01377 253617
	SPECIFICATION		(UNLESS OTHERWISE STATED)		
	CUMNOCK - DERSALLOCH ROUTE	GA - PLAN VIEW 20-35° ANGLE STRUCTURE	DATE	CHECKED	
			DRAWN	APPROVED	
			DRAWING NUMBER	REV	
			15_15229_60	A	