


DESCRIPTION					
FIRST ISSUE					
REV	DATE	BY	CHKD	APPD	
A	15/09/15	JDH	OC	KM	

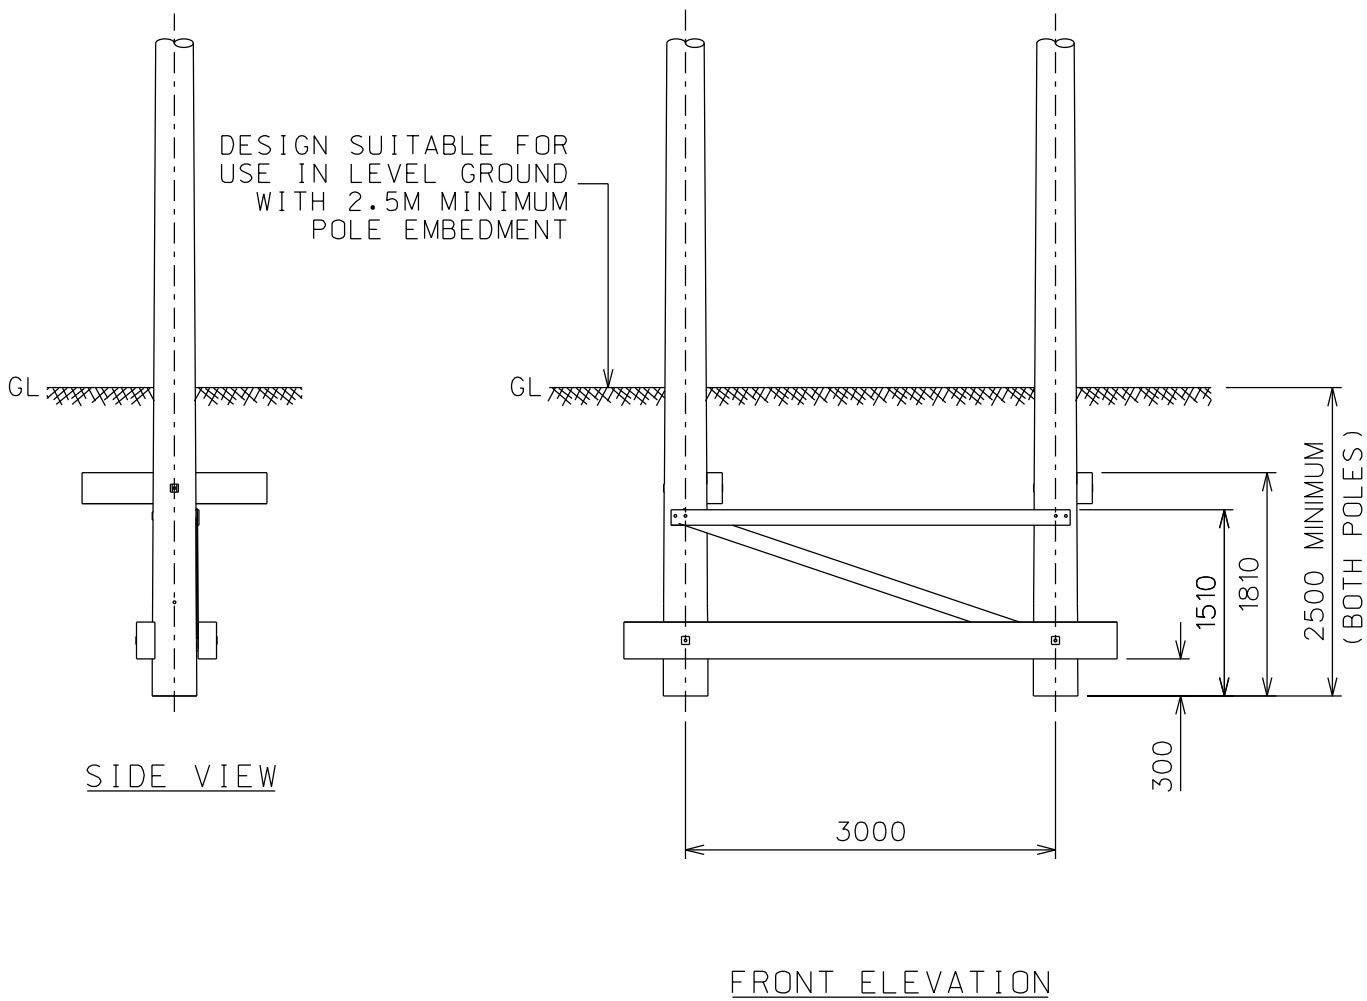

GENERAL NOTES:

- ALL STEELWORK TO BE PROTOTYPE CHECK ERECTED PRIOR TO MASS PRODUCTION.
 - ALL DIMENSIONS ARE IN MILLIMETRES.
 - NO ADDITIONAL ITEMS REQUIRED WHEN "POOR" SOIL CONDITIONS ARE ENCOUNTERED, BUT CAN ONLY BE INSTALLED IN LEVEL GROUND WITH 2.5M MINIMUM EMBEDMENT.
 - IMPORTANT:** REFER TO LSTC/STD/GNA/779 SHEETS 1 TO 4 FOR FOUNDATION DESIGN CRITERIA.
- SHT 1 : SOIL CLASSIFICATIONS & POLE EMBEDMENT DETAILS.
SHT 2 : FOUNDATION DETAILS / STRUCTURE TYPES.
SHT 3 : FACTORS OF SAFETY.
SHT 4 : OUTLINE DESIGN FOR "VERY POOR" SOIL FOUNDATIONS.
- TO BE READ IN CONJUNCTION WITH:
15_15229_66: H-POLE INTERMEDIATE STRUCTURE.
19_15229_67: MATERIAL LIST
LSTC/STD/GNA/555: BOLT LENGTH DETERMINATION

CLIENT  SPECIFICATION CUMNOCK - DERSALLOCH ROUTE	TITLE ADDITIONAL MATERIAL - 'H' POLE INTERMEDIATE POOR SOIL CONDITIONS	SCALE 1:60 (UNLESS OTHERWISE STATED)	ORIGINAL SIZE A4	LS TRANSMISSION CONSULTANCY LIMITED Yorkshire House York Road Little Driffield East Yorkshire YO25 5XA 01377 253617
		DATE 15/09/2015	CHECKED OC	
		DRAWN JDH	APPROVED KM	
		DRAWING NUMBER 16_15229_70	REV A	