



DESCRIPTION		FIRST ISSUE				
REV	DATE	BY	CHKD	APPD		
A	04/08/15	JDH	OC	KM		

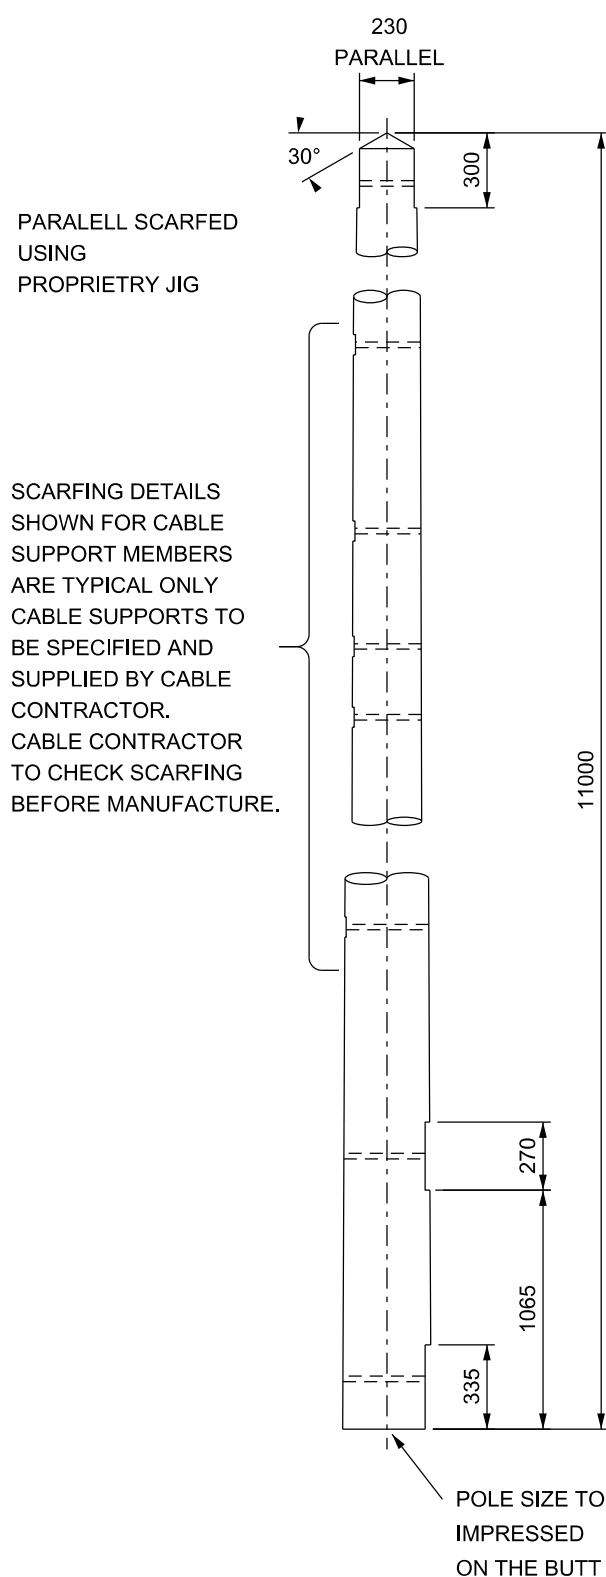

POLE SCARFED PARALLEL
ON BOTH SIDES TO GIVE
MIN 50mm FLAT FACE

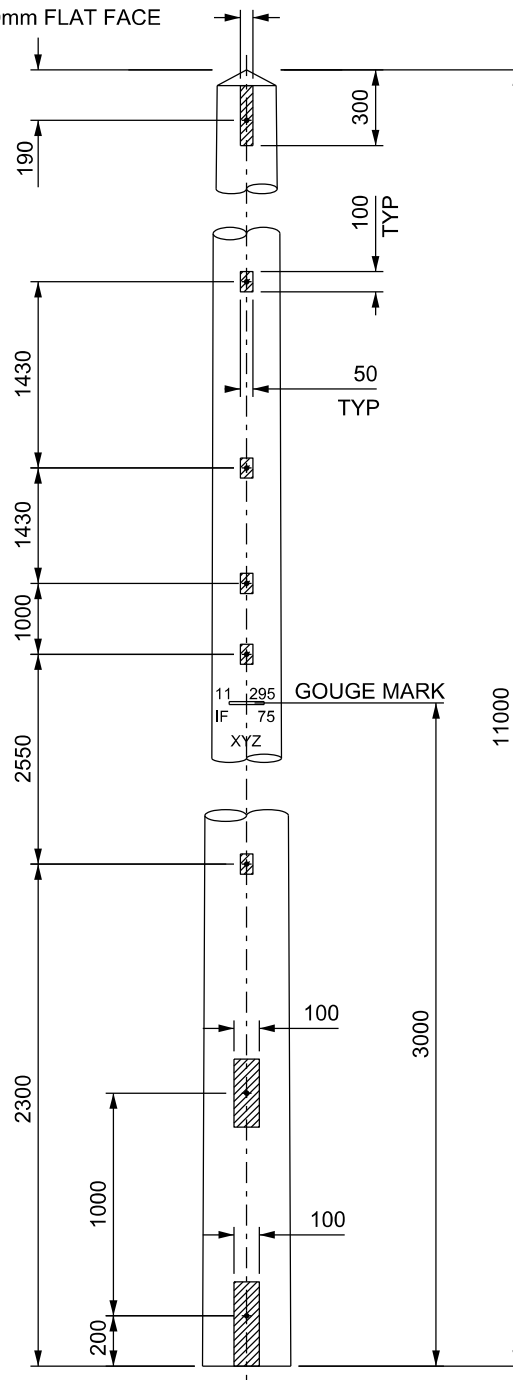

GENERAL NOTES:

1. ALL DIMENSIONS ARE IN mm, UNLESS NOTED
 2. ALL DRILLINGS TO BE 24mm DIAMETER HOLES
 3. POLE SIZES BASED ON BS1990, STOUT POLES RANGE
- LENGTH = 11m & PARALLEL WITHIN LIMITS
MINIMUM TOP DIAMETER = 240mm
MINIMUM DIA 1.5m FROM BUTT = 295mm

REFERENCE (typical only)

ACTUAL POLE VALUES TO BE USED

11 - POLE LENGTH

295 - POLE DIA. 1.5m FROM BUTT

IF - IMPORTED REDFIR

75 - YEAR OF CREOSOTING

XYZ - SUPPLIERS NAME OR MARK

GOUGE MARK 6 WIDE x 6 DEEP

3m FROM POLE BUTT

CLIENT

KTL

PROJECT

CUMNOCK - DERSALLOCH
ROUTE

TITLE

PART -
WOOD POLE SCARFING
4 POLE ENTRY TERMINAL
STRUCTURES
11m AUX. POLE

SCALE NTS
(UNLESS OTHERWISE STATED)

DATE 04/08/2015

DRAWN JDH

DRAWING NUMBER 18_15229_38

ORIGINAL SIZE A4

CHECKED OC

APPROVED KM

REV A

LS TRANSMISSION CONSULTANCY LIMITED
Yorkshire House
York Road
Little Driffield
East Yorkshire
YO25 5XA
01377 253617