


USED ON 15_15229_52

POLE SCARFED PARALLEL ON BOTH
SIDES TO GIVE 50mm WIDE FLAT FACE.

DESCRIPTION

FIRST ISSUE

REV	DATE	BY	CHKD	APPD
A	14/09/15	JDH	OC	KM

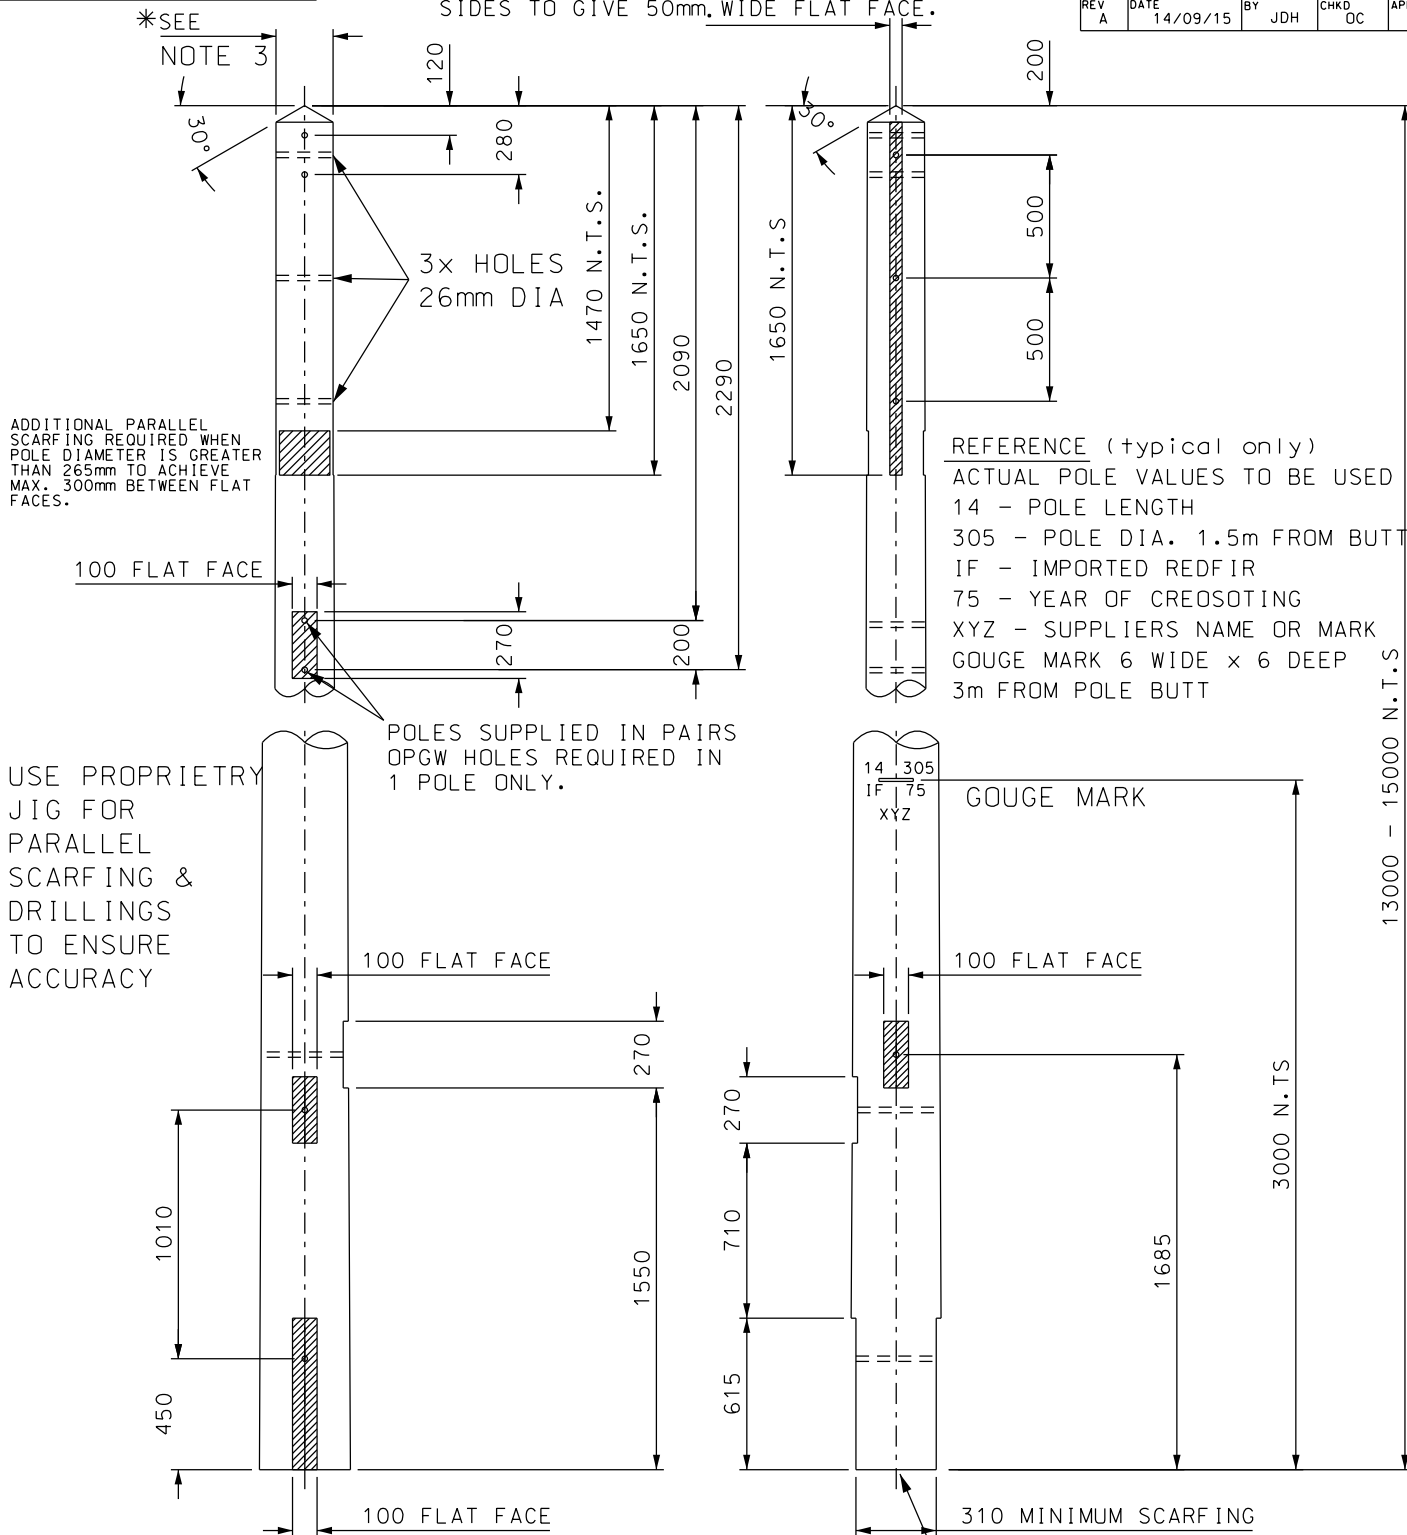

ADDITIONAL PARALLEL SCARFING REQUIRED WHEN POLE DIAMETER IS GREATER THAN 265mm TO ACHIEVE MAX. 300mm BETWEEN FLAT FACES.

USE PROPRIETARY JIG FOR PARALLEL SCARFING & DRILLINGS TO ENSURE ACCURACY

REFERENCE (typical only)
ACTUAL POLE VALUES TO BE USED
14 - POLE LENGTH
305 - POLE DIA. 1.5m FROM BUTT
IF - IMPORTED REDFIR
75 - YEAR OF CREOSOTING
XYZ - SUPPLIERS NAME OR MARK
GOUGE MARK 6 WIDE x 6 DEEP
3m FROM POLE BUTT

GENERAL NOTES:

1. ALL DIMENSIONS ARE IN mm, UNLESS NOTED
2. ALL DRILLINGS TO BE 24mm DIAMETER HOLES
3. POLE SIZES BASED ON BS1990, EXTRA STOUT POLES RANGE

LENGTH = 13m - 15m & PARALLEL WITHIN LIMITS

- * MINIMUM TOP DIST BETWEEN FLATS = 200mm
- * MAXIMUM TOP DIST BETWEEN FLATS = 265mm
- MINIMUM DIAMETER 1.5m FROM BUTT = 305mm

POLE SIZE TO BE
IMRESSED
ON THE BOTTOM

BAR MARK / ITEM NUMBER
TE666

SUPPLIER TO NOTE THESE DIMENSIONS ARE FOR GENERIC POLE DRILLING AND SCARFING ONLY TO SUIT A RANGE OF POLE SIZES. ACTUAL POLE MINIMUM DIMENSIONS TO BE SPECIFIED AT TIME OF ORDERING ORDER VALUES WILL SUPERSEDE THESE STATED VALUES. MAXIMUM VALUE NOT TO BE EXCEEDED.

CLIENT



TITLE

PART -
WOOD POLE
SCARFING DETAIL
5-20° ANGLE STRUCTURES

SPECIFICATION

CUMNOCK - DERSALLOCH
ROUTE

SCALE 1 : 30

(UNLESS OTHERWISE STATED)

DATE 14/09/2015

DRAWN JDH

DRAWING NUMBER 18_15229_55

ORIGINAL SIZE A4

CHECKED OC

APPROVED KM

REV A

LS TRANSMISSION CONSULTANCY LIMITED
Yorkshire House
York Road
Little Driffield
East Yorkshire
YO25 5XA
01377 253617

