
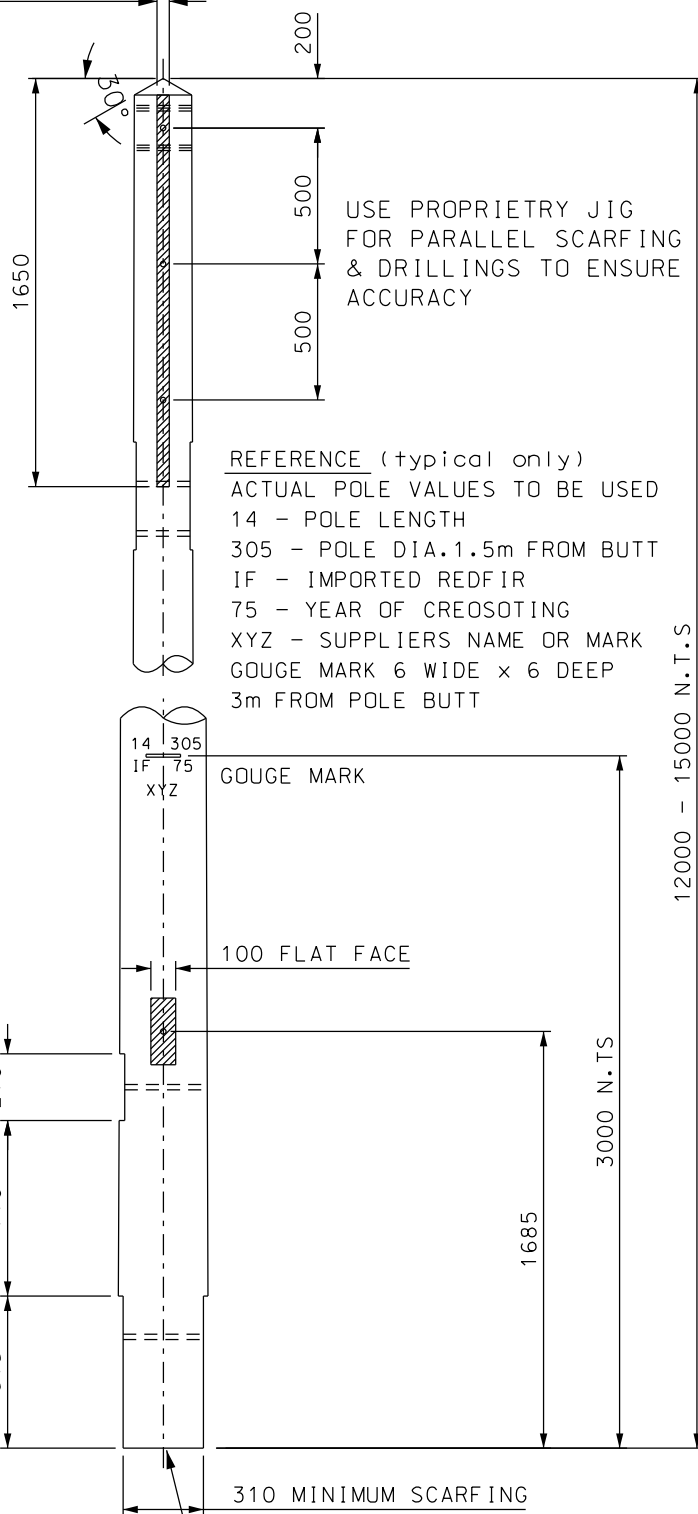


USED ON 15_15229_59

POLE SCARFED PARALLEL ON BOTH
SIDES TO GIVE 50mm WIDE FLAT FACE.

DESCRIPTION		FIRST ISSUE			
REV	DATE	BY	CHKD	APPD	
A	15/09/15	JDH	OC	KM	

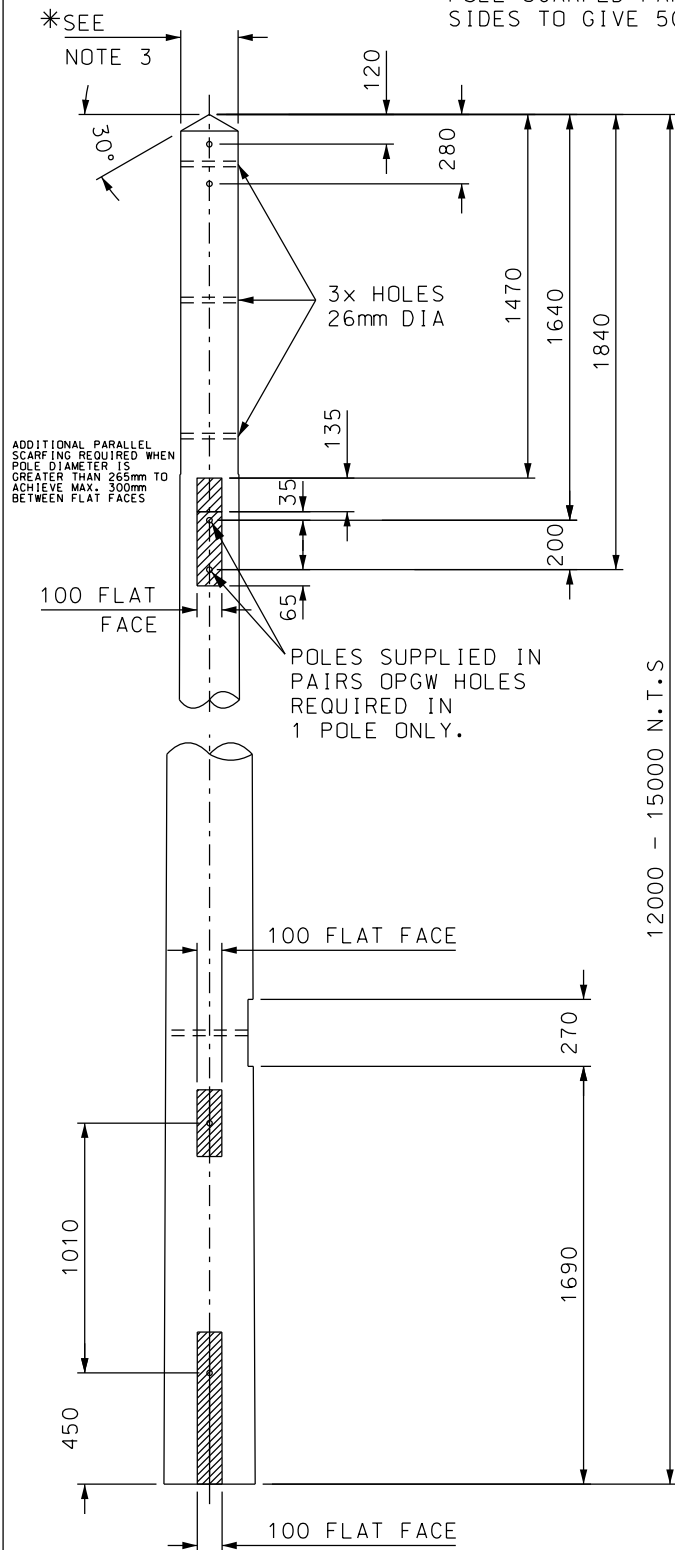

GENERAL NOTES:

1. ALL DIMENSIONS ARE IN mm, UNLESS NOTED
2. ALL DRILLINGS TO BE 24mm DIAMETER HOLES
3. POLE SIZES BASED ON BS1990, EXTRA STOUT POLES RANGE

LENGTH = 12m - 15m & PARALLEL WITHIN LIMITS.

*MINIMUM TOP DIST BETWEEN FLATS = 200mm

*MAXIMUM TOP DIST BETWEEN FLATS = 265mm

MINIMUM DIAMETER 1.5m FROM BUTT = 305mm

SUPPLIER TO NOTE THESE DIMENSIONS ARE FOR GENERIC
POLE DRILLING AND SCARFING ONLY TO SUIT A RANGE OF
POLE SIZES, ACTUAL POLE MINIMUM DIMENSIONS TO BE
SPECIFIED AT TIME OF ORDERING. ORDER VALUES WILL
SUPERSEDE THESE STATED VALUES. MAXIMUM VALUE NOT
TO BE EXCEEDED.

CLIENT



SPECIFICATION

CUMNOCK - DERSALLOCH
ROUTE

TITLE

PART -
WOOD POLE
SCARFING DETAILS
20-35° ANGLE
STRUCTURES

SCALE 1:30

(UNLESS OTHERWISE STATED)

DATE 15/09/15

DRAWN JDH

DRAWING NUMBER

18_15229_62

ORIGINAL SIZE

A4

CHECKED

OC

APPROVED

KM

REV

A

LS TRANSMISSION CONSULTANCY LIMITED
Yorkshire House
York Road
Little Driffield
East Yorkshire
YO25 5XA
01377 253617

