


USED ON 15_15229_66

POLE SCARFED PARALLEL ON BOTH
SIDES TO GIVE 50mm WIDE FLAT FACE

DESCRIPTION

FIRST ISSUE

REV	DATE	BY	CHKD	APPD
A	15/09/15	JDH	OC	KM

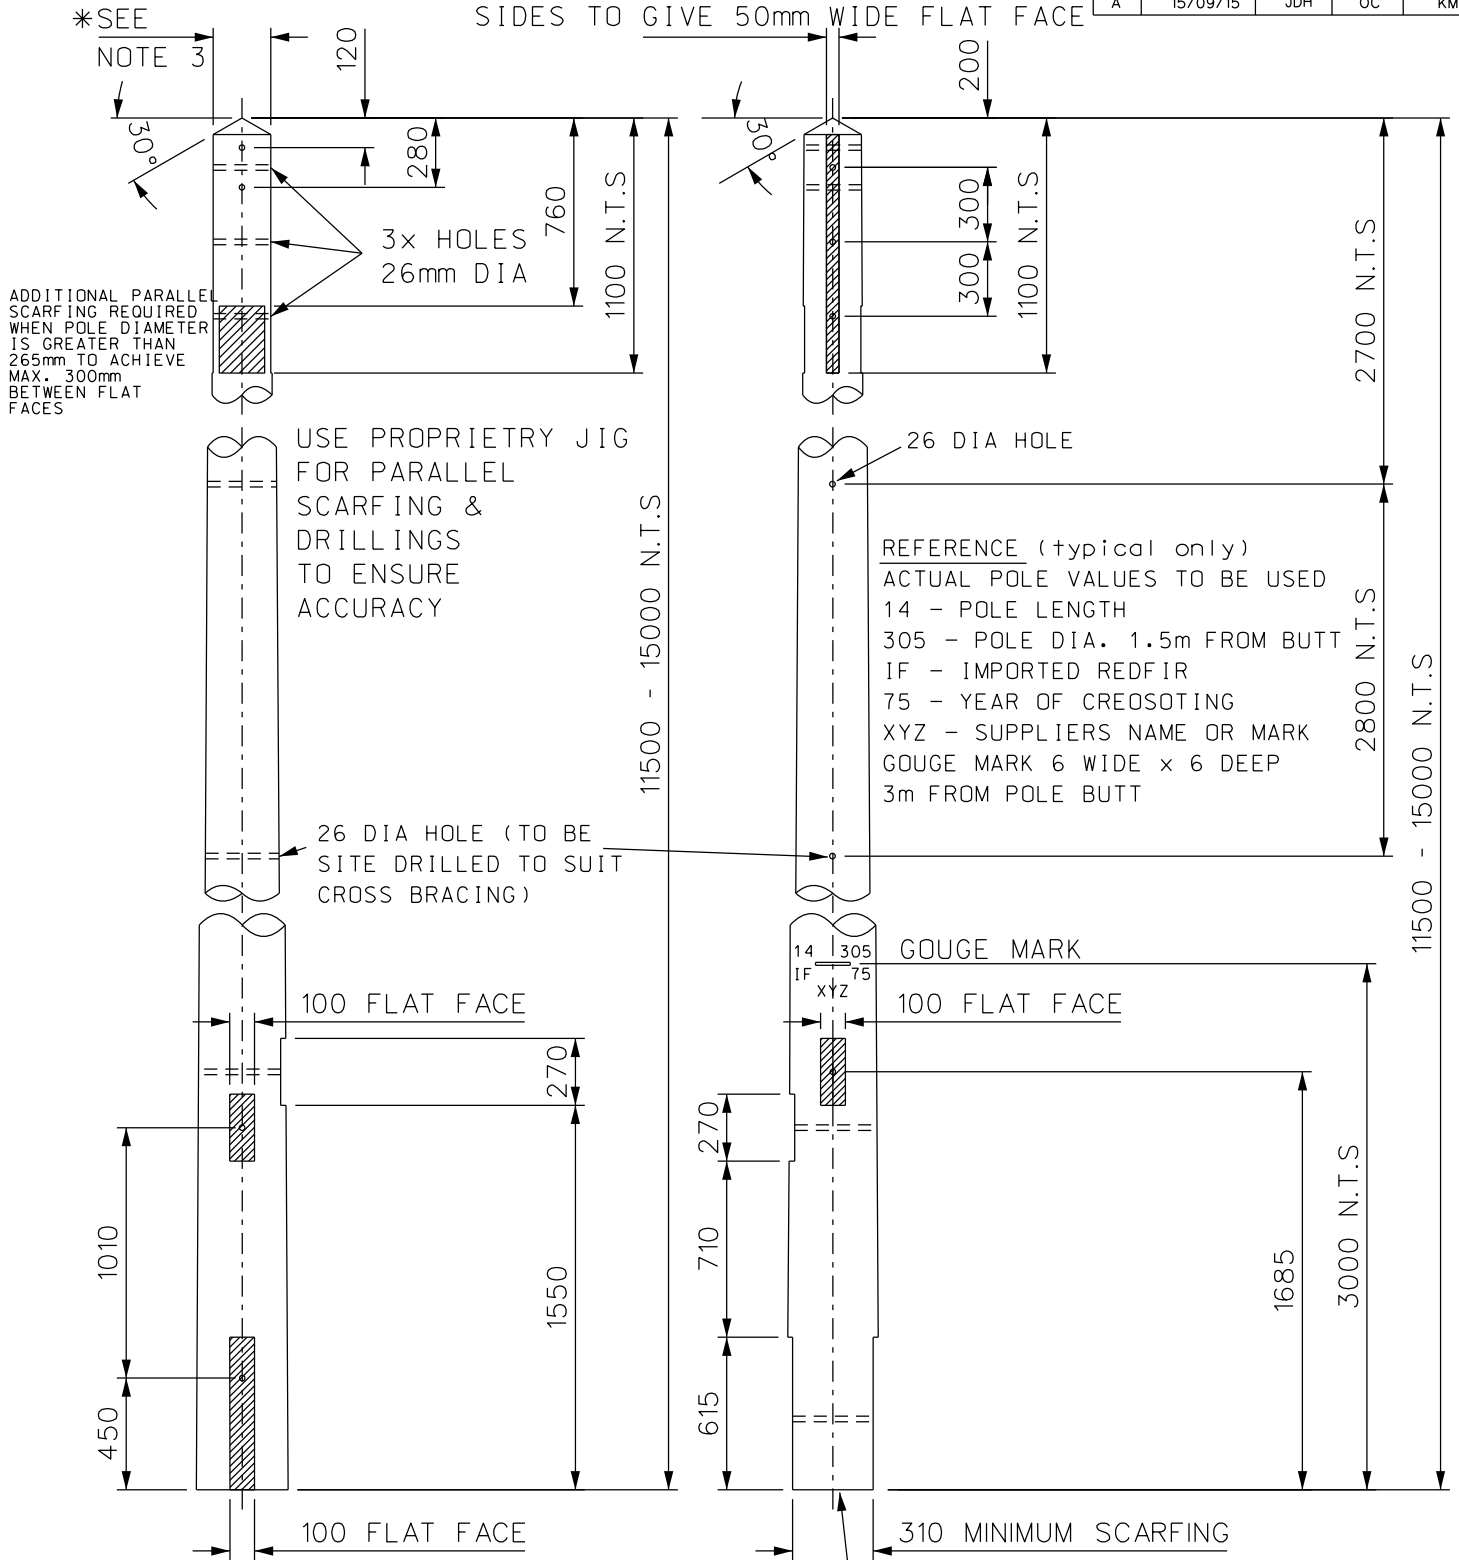

GENERAL NOTES:

1. ALL DIMENSIONS ARE IN mm, UNLESS NOTED
2. ALL DRILLINGS TO BE 24mm DIAMETER HOLES UND.
3. POLE SIZES BASED ON BS1990, EXTRA STOUT POLES RANGE
LENGTH = 11.5m - 15m & PARALLEL WITHIN LIMITS
MINIMUM TOP DIST BETWEEN FLATS = 200mm
*MAXIMUM TOP DIST BETWEEN FLATS = 265mm
*MINIMUM DIAMETER 1.5m FROM BUTT = 305mm

SUPPLIER TO NOTE THESE DIMENSIONS ARE FOR GENERIC POLE DRILLING AND SCARFING ONLY TO SUIT A RANGE OF POLE SIZES. ACTUAL POLE MINIMUM DIMENSIONS TO BE SPECIFIED AT TIME OF ORDERING. ORDER VALUES WILL SUPERSEDE THESE STATED VALUES. MAXIMUM VALUE NOT TO BE EXCEEDED.

CLIENT



SPECIFICATION

CUMNOCK - DERSALLOCH
ROUTE

TITLE

PART -
WOOD POLE
SCARFING DETAILS
'H' POLE INTERMEDIATE

SCALE 1:30

(UNLESS OTHERWISE STATED)

DATE 15/09/2015

DRAWN JDH

DRAWING NUMBER

18_15229_68

ORIGINAL SIZE

A4

CHECKED

OC

APPROVED

KM

REV

A

LS TRANSMISSION CONSULTANCY LIMITED

Yorkshire House

York Road

Little Driffield

East Yorkshire

YO25 5XA

01377 253617

