


USED ON LSTC/STD/GNA/527

POLE SCARFED PARALLEL ON BOTH SIDES TO GIVE 50mm WIDE FLAT FACE

DESCRIPTION



FOR ISSUE

REV	DATE	BY	RF	CHKD	SP	APPD	GS
6	27/11/07						

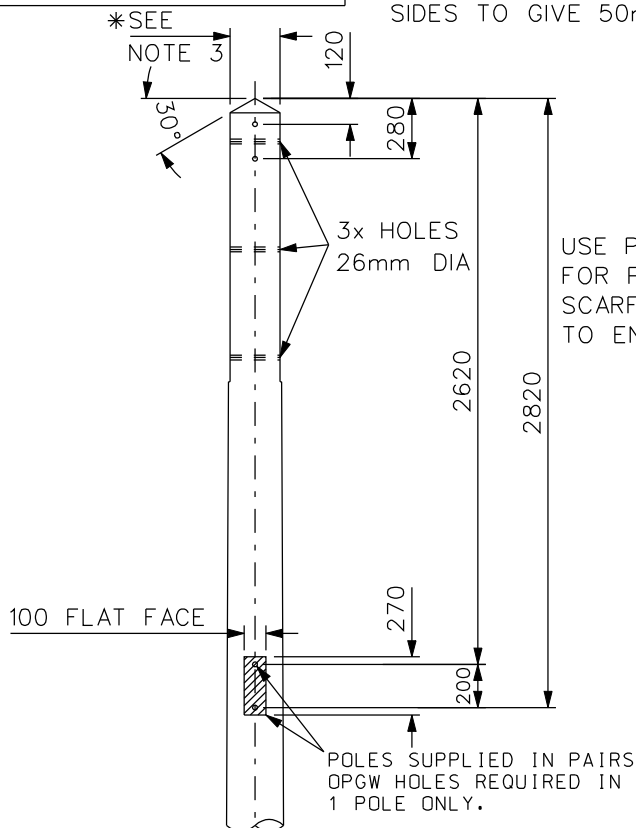


USE PROPRIETARY JIG FOR PARALLEL SCARFING & DRILLINGS TO ENSURE ACCURACY

REFERENCE (typical only)
 ACTUAL POLE VALUES TO BE USED
 14 - POLE LENGTH
 305 - POLE DIA. 1.5m FROM BUTT
 IF - IMPORTED REDFIR
 75 - YEAR OF CREOSOTING
 XYZ - SUPPLIERS NAME OR MARK
 GOUGE MARK 6 WIDE x 6 DEEP
 3m FROM POLE BUTT

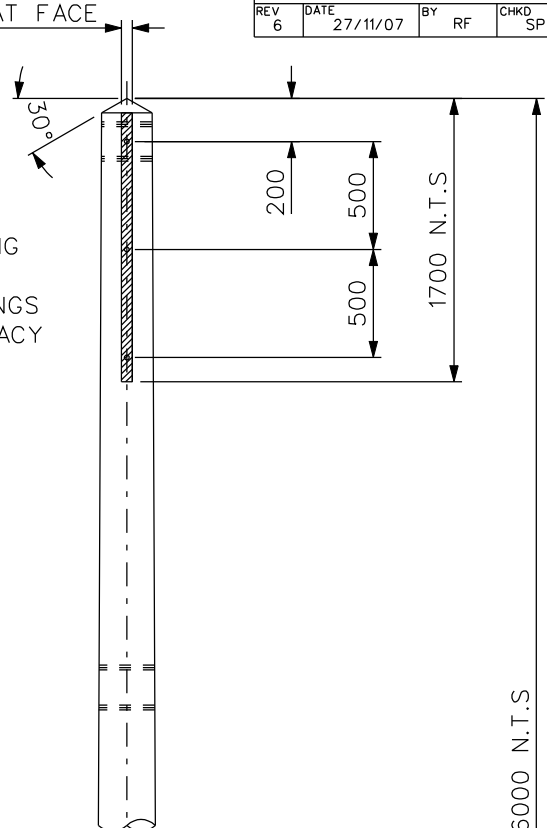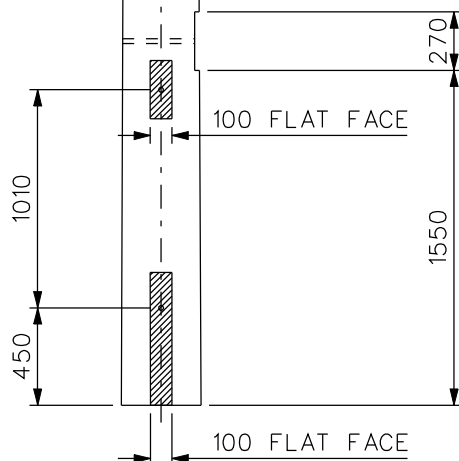

14000 - 16000 N.T.S

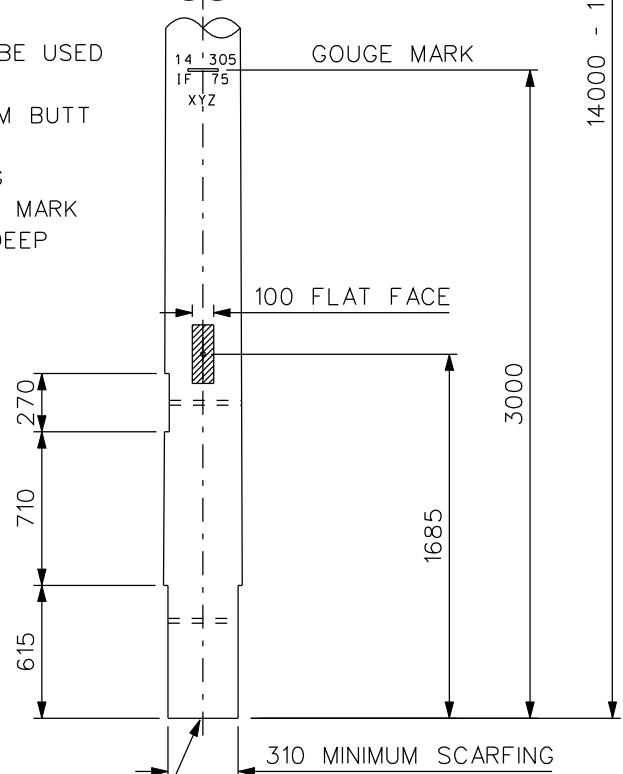

GENERAL NOTES:

1. ALL DIMENSIONS ARE IN mm, UNLESS NOTED
2. ALL DRILLINGS TO BE 24mm DIAMETER HOLES
3. POLE SIZES BASED ON BS1990, EXTRA STOUT POLES RANGE
 LENGTH = 14m - 16m & PARALLEL WITHIN LIMITS
 *MINIMUM TOP DIST BETWEEN FLATS = 200mm
 *MAXIMUM TOP DIST BETWEEN FLATS = 265mm
 MINIMUM DIAMETER 1.5m FROM BUTT = 305mm

POLE SIZE TO BE IMPRESSED ON THE BOTTOM

BAR MARK / ITEM NUMBER
 TE640

SUPPLIER TO NOTE THESE DIMENSIONS ARE FOR GENERIC POLE DRILLING AND SCARFING ONLY TO SUIT A RANGE OF POLE SIZES, ACTUAL POLE MINIMUM DIMENSIONS TO BE SPECIFIED AT TIME OF ORDERING. ORDER VALUES WIL SUPERSEDE THESE STATED VALUES. MAXIMUM VALUE NOT TO BE EXCEEDED

CLIENT PowerSystems		TITLE PART - WOOD POLE SCARFING DETAILS	SCALE 1 : 35 (UNLESS OTHERWISE STATED)		ORIGINAL SIZE A4	LS TRANSMISSION CONSULTANCY LIMITED Yorkshire House York Road Little Driffeld East Yorkshire YO25 5XA 01377 253617 
SPECIFICATION OHL-03-132			DATE 17/01/05	CHECKED GS		
			DRAWN JN	APPROVED PP		
			DRAWING NUMBER LSTC/STD/PAR/640		REV 6	

