
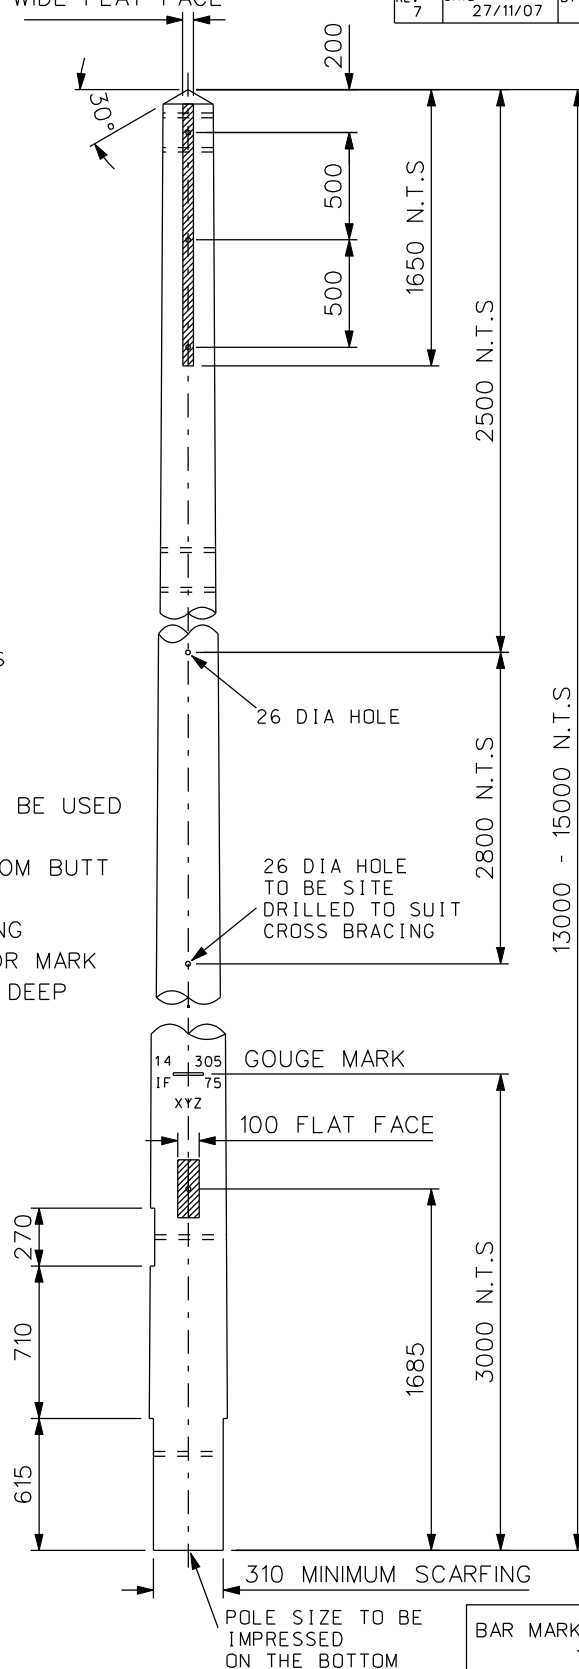


USED ON LSTC/STD/GNA/542

POLE SCARFED PARALLEL ON BOTH SIDES TO GIVE 50mm WIDE FLAT FACE

DESCRIPTION		FOR ISSUE				
REV	DATE	BY	RF	CHKD	SP	APPD
7	27/11/07					GS

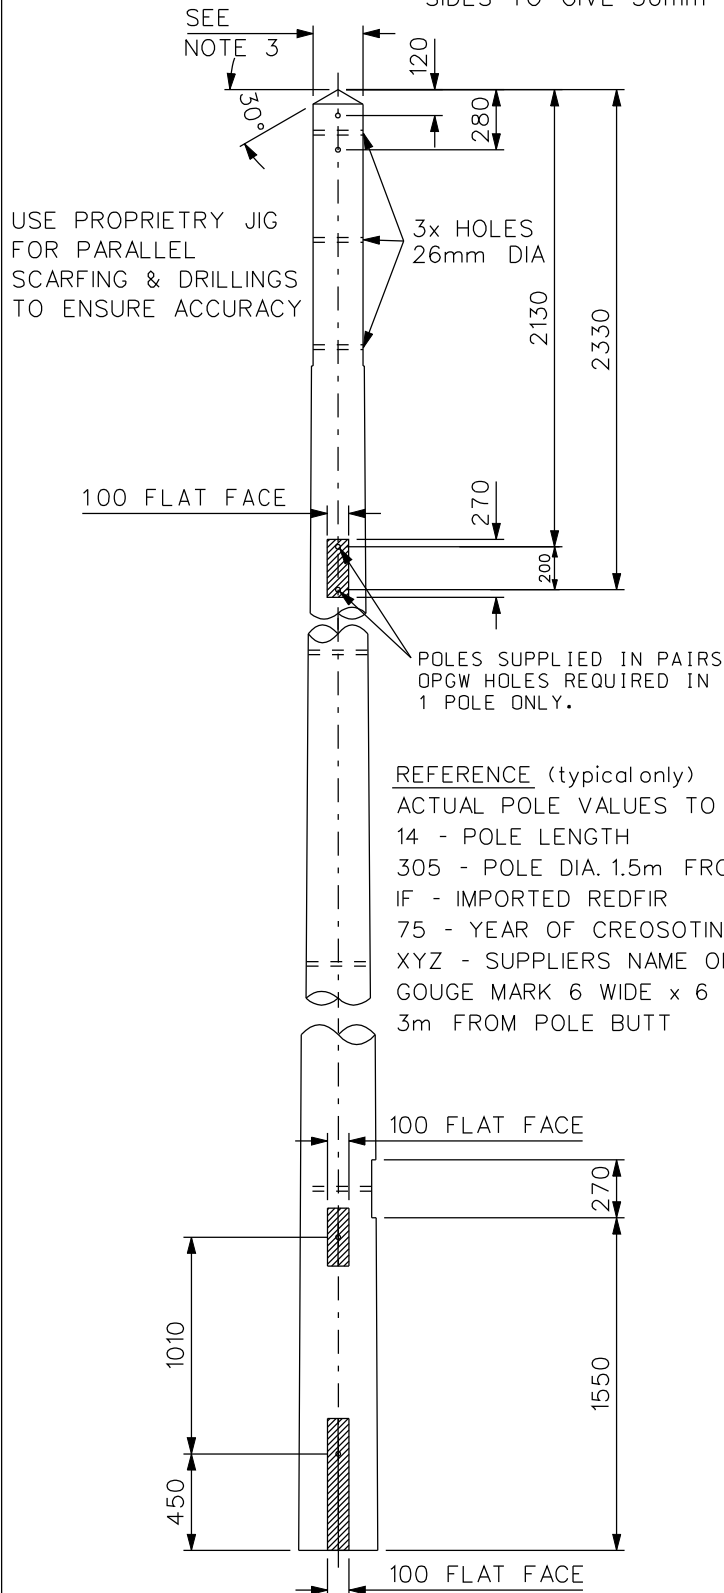

GENERAL NOTES:

1. ALL DIMENSIONS ARE IN mm, UNLESS NOTED
2. ALL DRILLINGS TO BE 24mm DIAMETER HOLES UNO.
3. POLE SIZES BASED ON BS1990, EXTRA STOUT POLES RANGE
 LENGTH = 13m - 15m & PARALLEL WITHIN LIMITS
 * MINIMUM TOP DIST BETWEEN FLATS = 200mm
 * MAXIMUM TOP DIST BETWEEN FLATS = 265mm
 MINIMUM DIAMETER 1.5m FROM BUTT = 305mm

SUPPLIER TO NOTE THESE DIMENSIONS ARE FOR GENERIC POLE DRILLING AND SCARFING ONLY TO SUIT A RANGE OF POLE SIZES, ACTUAL POLE MINIMUM DIMENSIONS TO BE SPECIFIED AT TIME OF ORDERING. ORDER VALUES WILL SUPERSEDE THESE STATED VALUES. MAXIMUM VALUE NOT TO BE EXCEEDED

BAR MARK / ITEM NUMBER
TE650

CLIENT	PowerSystems
SPECIFICATION	OHL-03-132

TITLE	PART - WOOD POLE SCARFING DETAILS - SECTION STRUCTURE
-------	--

SCALE	1 : 35 (UNLESS OTHERWISE STATED)	ORIGINAL SIZE	A4
DATE	17/01/05	CHECKED	GS
DRAWN	JN	APPROVED	PP
DRAWING NUMBER	LSTC/STD/PAR/650	REV	7

LS TRANSMISSION CONSULTANCY LIMITED
 Yorkshire House
 York Road
 Little Driffield
 East Yorkshire
 YO25 5XA
 01377 253617

