
DESCRIPTION				
FIRST ISSUE				
REV	DATE	BY	CHKD	APPD
A	15/09/15	JDH	OC	KM

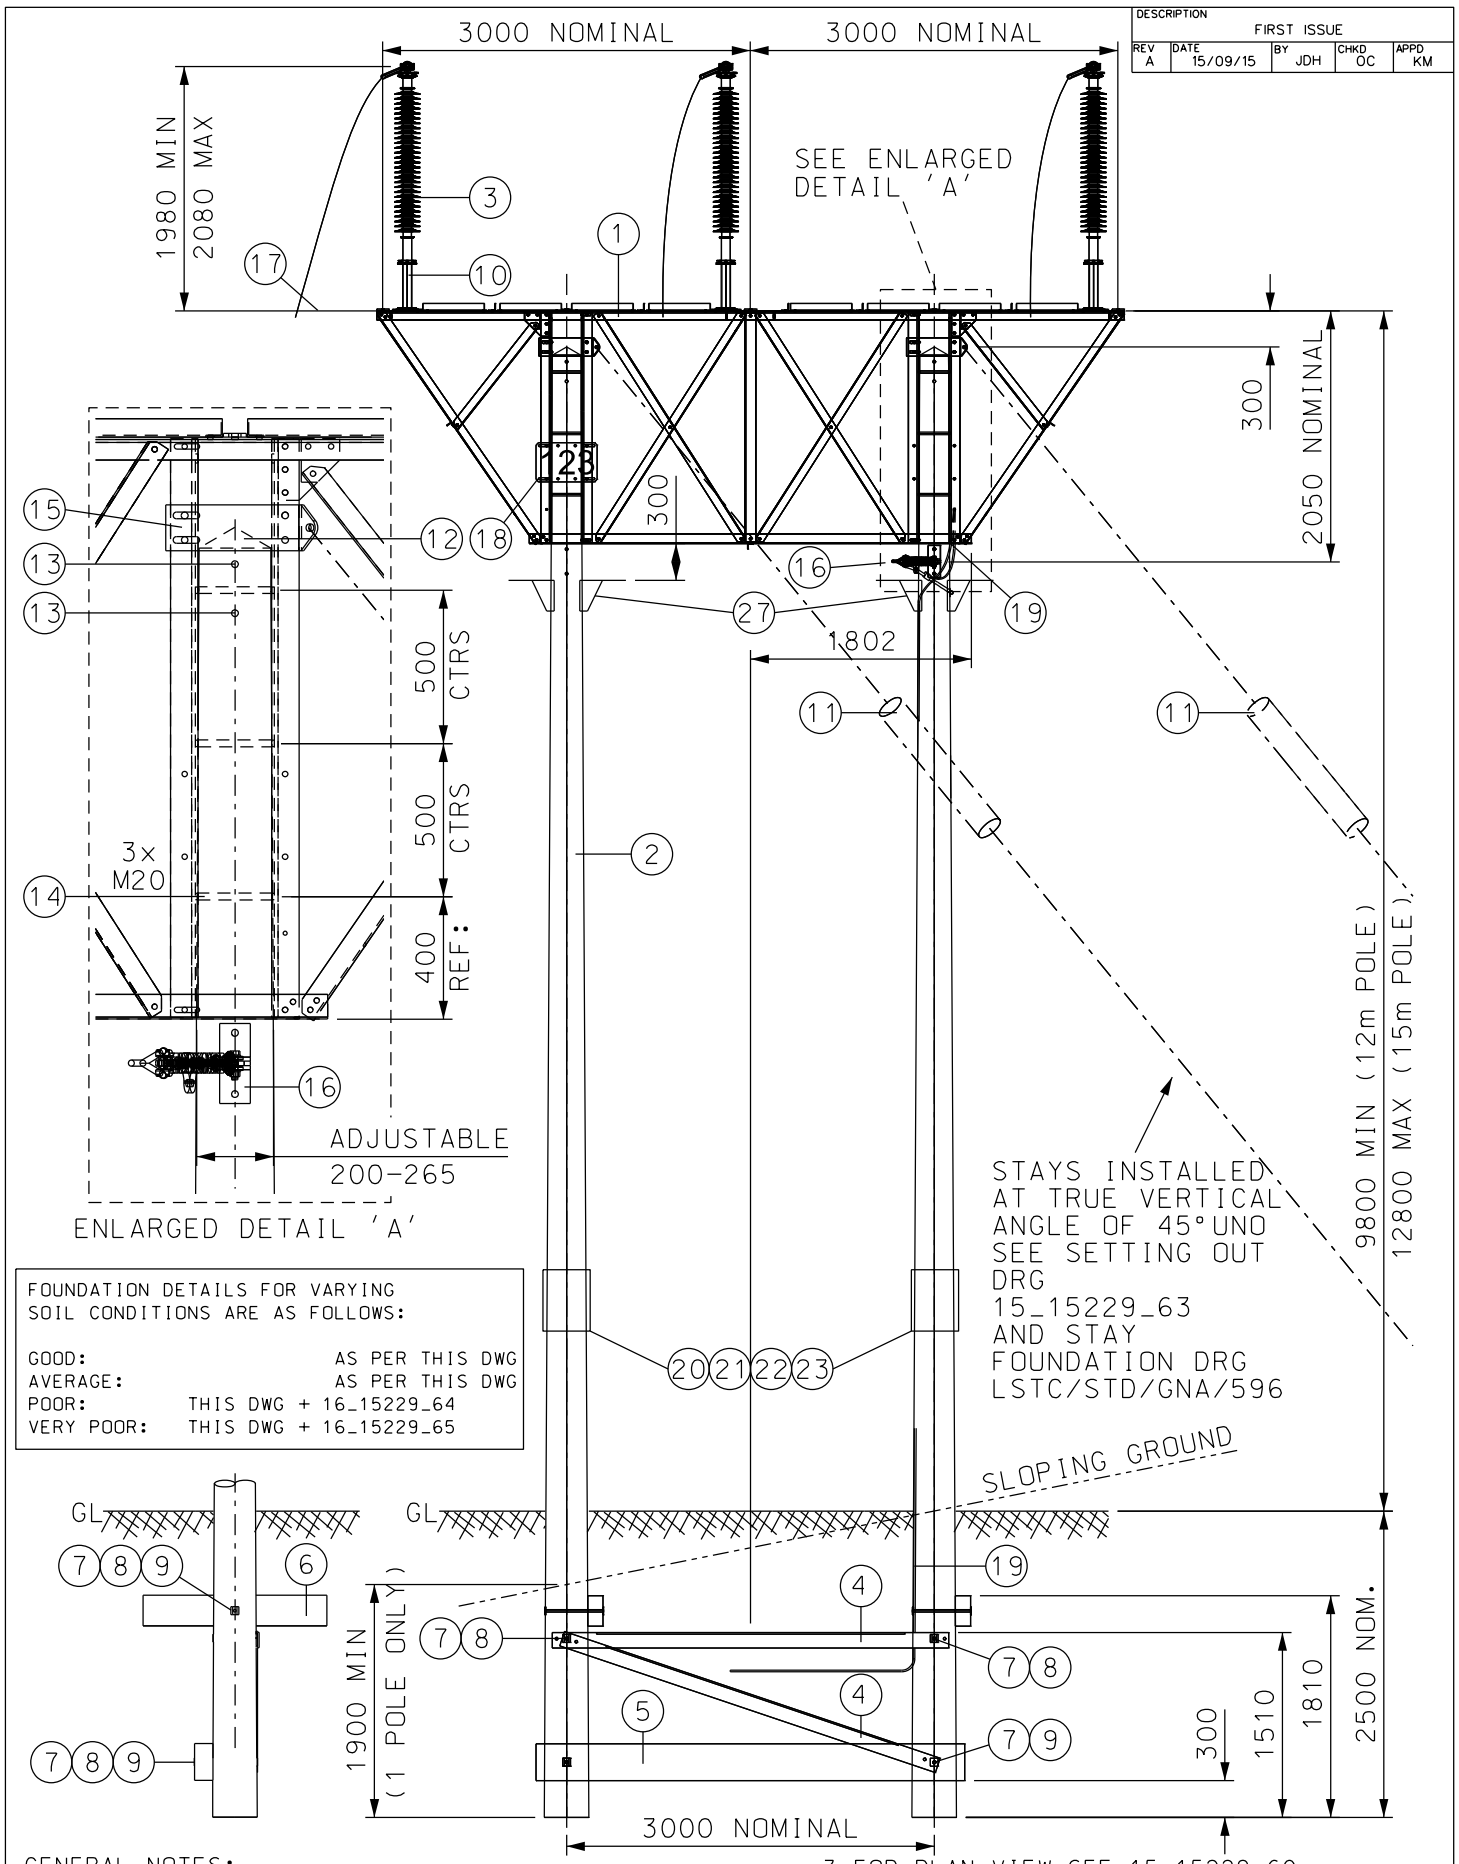

FOUNDATION DETAILS FOR VARYING SOIL CONDITIONS ARE AS FOLLOWS:

GOOD:	AS PER THIS DWG
AVERAGE:	AS PER THIS DWG
POOR:	THIS DWG + 16_15229_64
VERY POOR:	THIS DWG + 16_15229_65

GENERAL NOTES:

1. ALL STEELWORK TO BE PROTOTYPE CHECK ERECTED BEFORE MASS PRODUCTION.
2. SAFETY SIGNS TO BE INSTALLED TO CONFORM TO POWER SYSTEMS PROCEDURES
3. FOR PLAN VIEW SEE 15_15229_60
4. FOR MATERIAL LIST SEE 19_15229_61
5. OPGW TO BE INSTALLED ON THE SAME SIDE OF STRUCTURES THROUGHOUT. NO CROSSING OF OPGW AND PHASE CONDUCTORS PERMITTED.

CLIENT: KTL	TITLE: GA - 20-35° ANGLE STRUCTURE	SCALE: 1:60 (UNLESS OTHERWISE STATED)	ORIGINAL SIZE: A4
SPECIFICATION: CUMNOCK - DERSALLOCH ROUTE		DATE: 15/09/2015	CHECKED: OC
		DRAWN: JDH	APPROVED: KM
		DRAWING NUMBER: 15_15229_59	REV: A

LS TRANSMISSION CONSULTANCY LIMITED
Yorkshire House
York Road
Little Driffield
East Yorkshire
YO25 5XA
01377 253617