
DESCRIPTION				
FIRST ISSUE				
REV	DATE	BY	CHKD	APPD
A	15/09/15	JDH	OC	KM

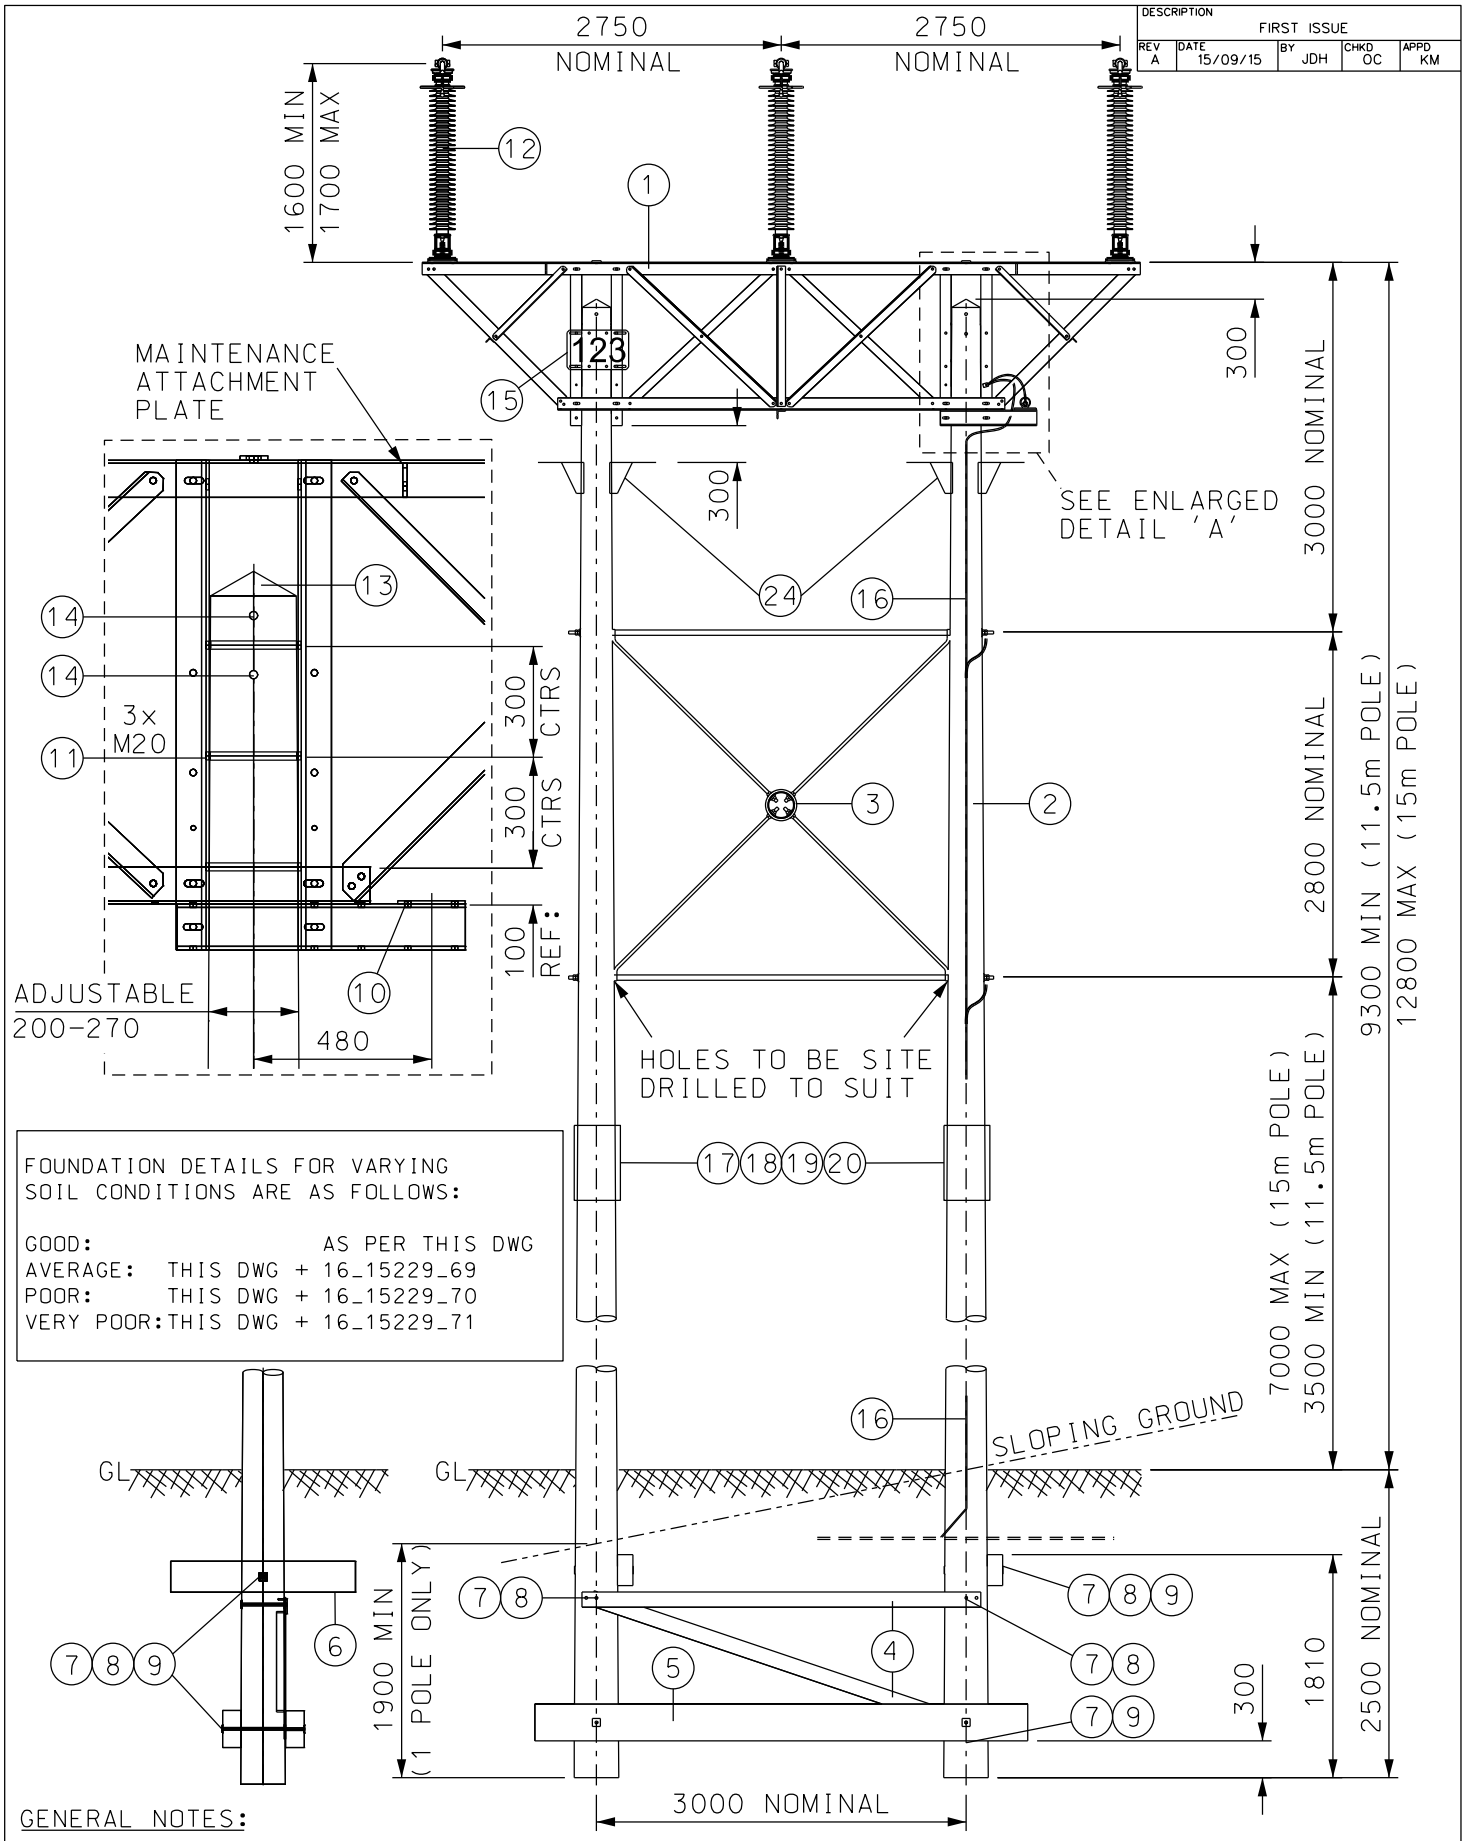

FOUNDATION DETAILS FOR VARYING SOIL CONDITIONS ARE AS FOLLOWS:

GOOD:	AS PER THIS DWG
AVERAGE:	THIS DWG + 16_15229_69
POOR:	THIS DWG + 16_15229_70
VERY POOR:	THIS DWG + 16_15229_71

GENERAL NOTES:

1. ALL STEELWORK TO BE PROTOTYPE CHECK ERECTED BEFORE MASS PRODUCTION.
2. SAFETY SIGNS TO BE INSTALLED TO CONFORM TO POWER SYSTEMS PROCEDURES
3. FOR MATERIAL LIST SEE 19_15229_67
4. OPGW TO BE INSTALLED ON THE SAME SIDE OF STRUCTURES THROUGHOUT. NO CROSSING OF OPGW AND PHASE CONDUCTORS PERMITTED.
5. FOR MAINTENANCE ATTACHMENT LOCATIONS SEE LSTC/STD/GNA/550

CLIENT: KTL	TITLE: GA - 'H' POLE INTERMEDIATE STRUCTURE	SCALE: 1:60 (UNLESS OTHERWISE STATED)	ORIGINAL SIZE: A4
SPECIFICATION: CUMNOCK - DERSALLOCH ROUTE		DATE: 15/09/2015	CHECKED: OC
		DRAWN: JDH	APPROVED: KM
		DRAWING NUMBER: 15_15229_66	REV: A

LS TRANSMISSION CONSULTANCY LIMITED
Yorkshire House
York Road
Little Driffield
East Yorkshire
YO25 5XA
01377 253617