


DESCRIPTION					FIRST ISSUE				
REV	A	DATE	01/01/06	BY	T.S.	CHKD	G.S.	APPD	PP

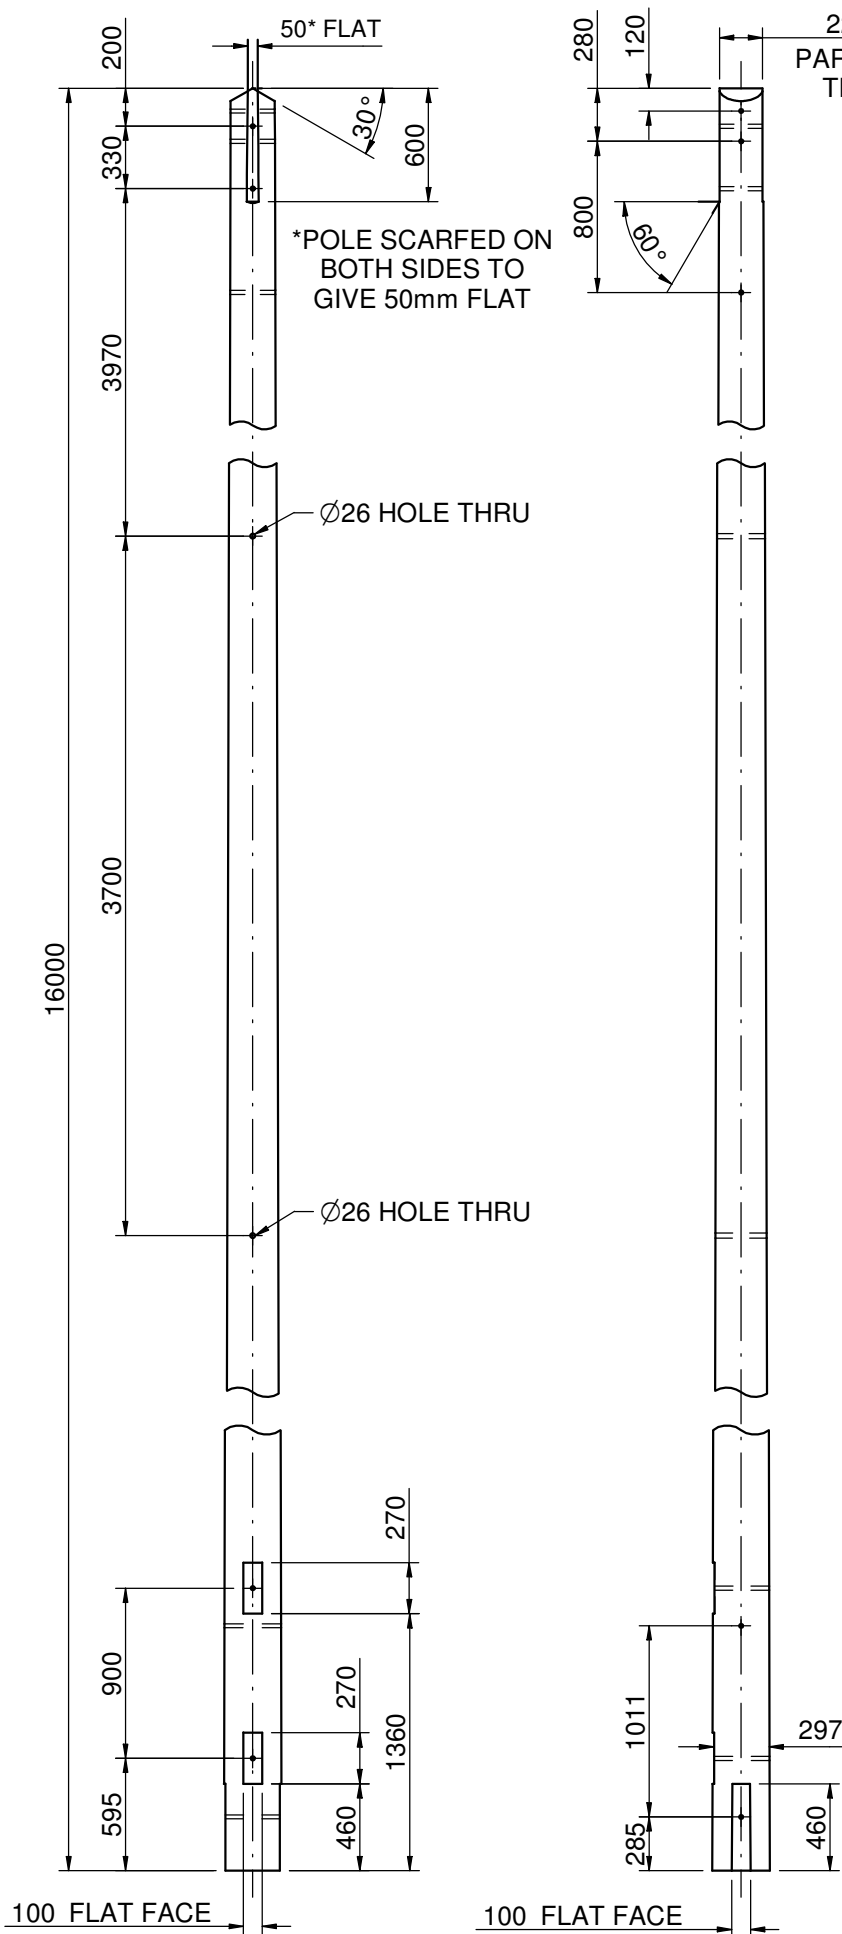

227 - 240mm
PARALLEL WITHIN
THESE LIMITS

GENERAL NOTES:

1. ALL DIMENSIONS ARE IN MILLIMETRES (mm).
2. ALL HOLES TO BE 22mm DIA UNLESS OTHERWISE STATED.
3. POLE SIZES BASED ON BS1990 EXTRA STOUT POLES.
4. 233mm MIN. TOP POLE DIAMETER.
365mm MIN. DIAMETER @ 1.5M FROM BUTT.
5. USE IN CONJUNCTION WITH DRAWINGS:
15_06093_20 : GA DRAWING
19_06093_34 : MATERIAL LIST
6. STRUCTURE TO BE CHECK ERECTED PRIOR TO SITE INSTALLATION.

SCARFING NOTES:

SCARFING DETAILS SHOWN ARE TO POSITION BAULKS THAT ARE SUITABLE FOR GOOD GROUND CONDITIONS. SEE NOTE 5 DRG No.15_06093_20.

CLIENT
Enterprise Power Services

PROJECT
M1 WIDENING

TITLE
WOOD POLE DETAILS
BAR MARK: INT_05
SHEET 5 OF 6

SCALE	1:5	ORIGINAL SIZE	A4
DATE	11/04/06	CHECKED	G.S.
DRAWN	TSleap	APPROVED	PP
DRAWING NUMBER	18_06093_21_Sht5	REV	A



Yorkshire House
York Road
Little Drifffield
East Yorkshire
YO25 5XA
Tel 01377 253617
Fax 01377 259555