





USED ON LSTC/STD/GNA/505

POLE SCARFED PARALLEL ON BOTH
SIDES TO GIVE 50mm WIDE FLAT FACE.

DESCRIPTION

FOR ISSUE

REV	DATE	BY	RF	CHKD	SP	APPD	GS
6	27/11/07						

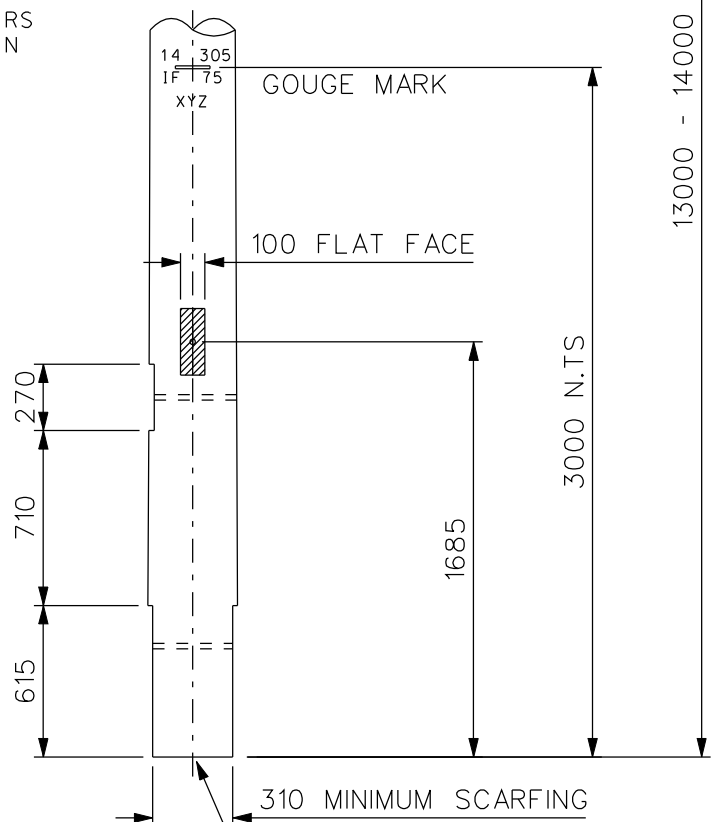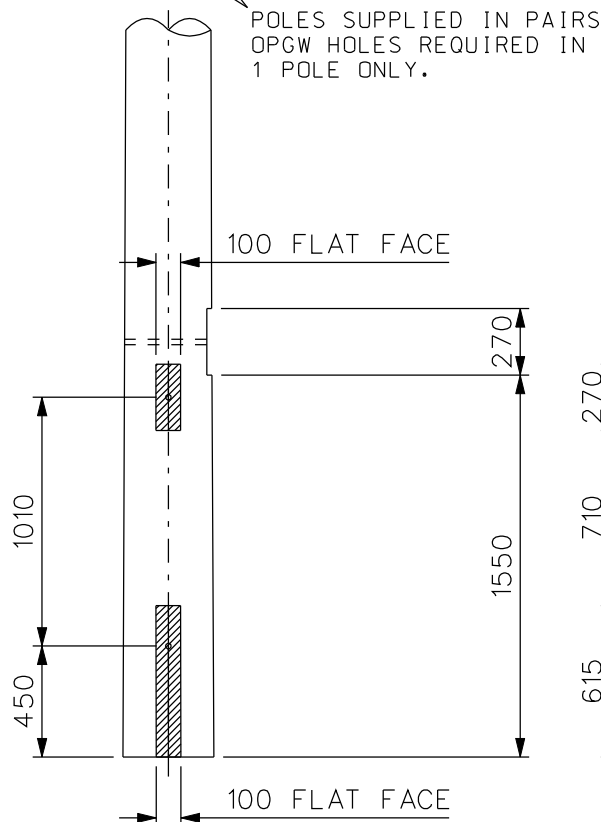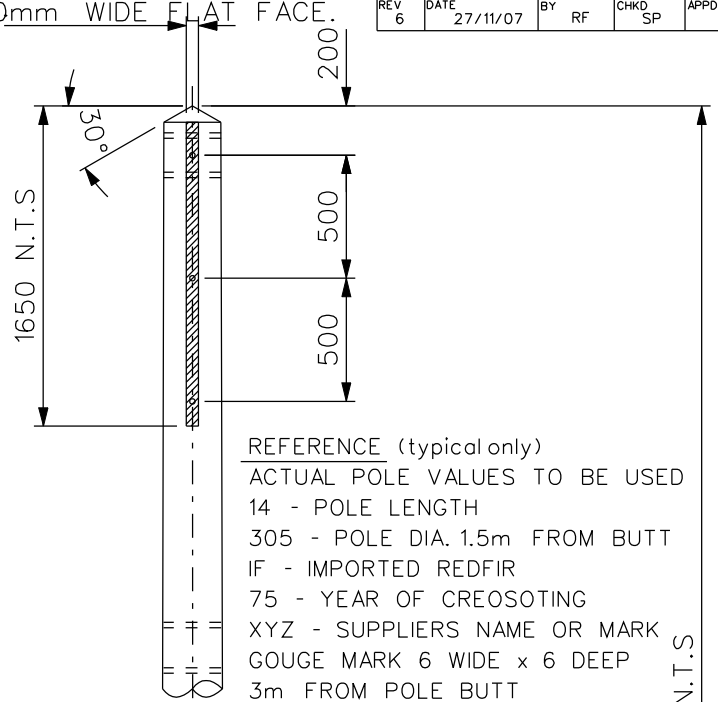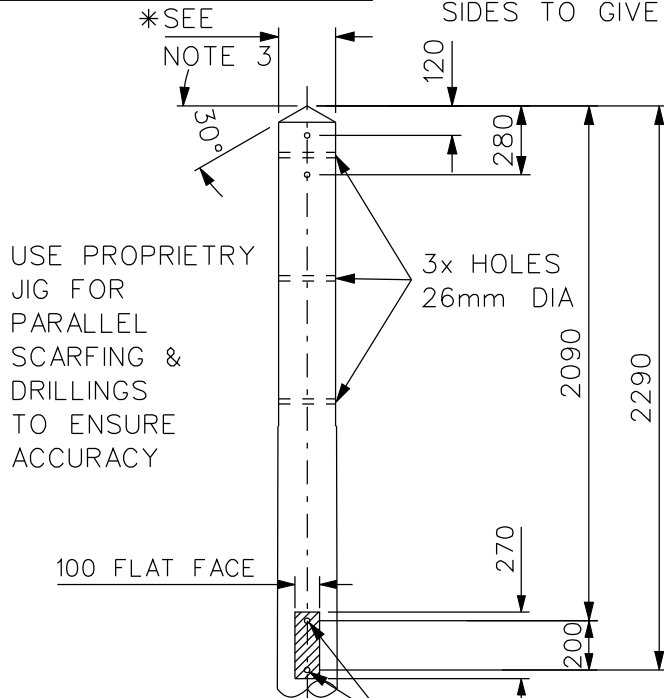

GENERAL NOTES:

1. ALL DIMENSIONS ARE IN mm, UNLESS NOTED
2. ALL DRILLINGS TO BE 24mm DIAMETER HOLES
3. POLE SIZES BASED ON BS1990, EXTRA STOUT POLES RANGE

LENGTH = 13m - 14m & PARALLEL WITHIN LIMITS

* MINIMUM TOP DIST BETWEEN FLATS = 200mm

* MAXIMUM TOP DIST BETWEEN FLATS = 265mm

MINIMUM DIAMETER 1.5m FROM BUTT = 305mm

POLE SIZE TO BE
IMRESSED
ON THE BOTTOMBAR MARK / ITEM NUMBER
TE666

SUPPLIER TO NOTE THESE DIMENSIONS ARE FOR GENERIC POLE DRILLING AND SCARFING ONLY TO SUIT A RANGE OF POLE SIZES, ACTUAL POLE MINIMUM DIMENSIONS TO BE SPECIFIED AT TIME OF ORDERING ORDER VALUES WILL SUPERSEDE THESE STATED VALUES. MAXIMUM VALUE NOT TO BE EXCEEDED.

CLIENT
PowerSystemsSPECIFICATION
OHL-03-132TITLE
PART -
WOOD POLE
SCARFING DETAIL
5-20° ANGLE STRUCTURES

SCALE 1:30

(UNLESS OTHERWISE STATED)

DATE 17/01/05

DRAWN JN

DRAWING NUMBER LSTC/STD/PAR/666

ORIGINAL SIZE A4

CHECKED GS

APPROVED PP

REV 6

LS TRANSMISSION CONSULTANCY LIMITED
Yorkshire House
York Road
Little Driffield
East Yorkshire
YO25 5XA
01377 253617

