


DESCRIPTION					
FIRST ISSUE					
REV	A	DATE	28/04/06	BY	RF
		CHKD	JG	APPD	GS

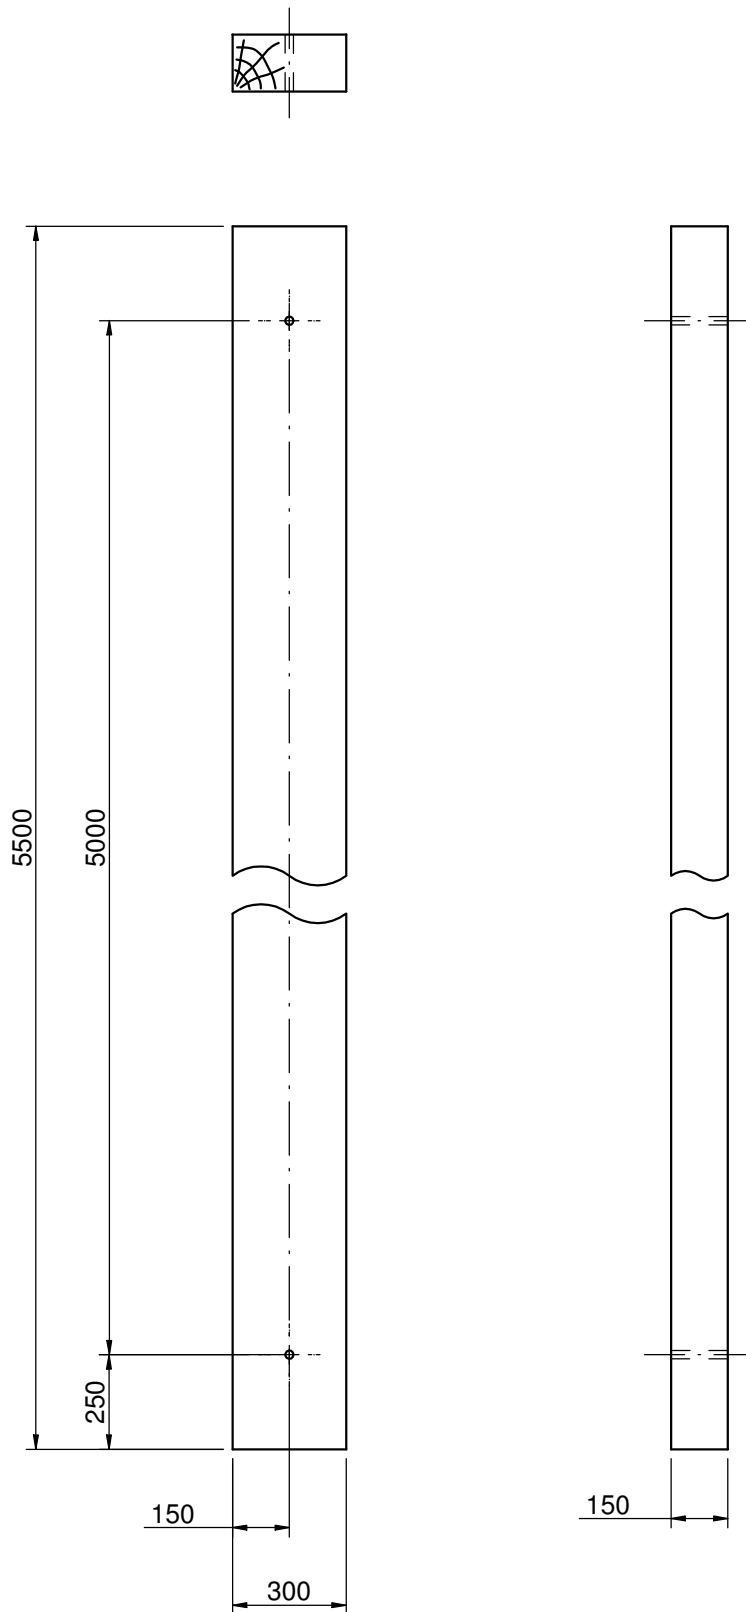

GENERAL NOTES:

1. ALL DIMENSIONS ARE IN MILLIMETRES (mm)
2. ALL HOLES TO BE 22.0 DIA UNLESS NOTED OTHERWISE.
3. APPROX WEIGHT = 175kg

CLIENT Enterprise Power Services	TITLE H POLE TIMBER BAULK	SCALE 1:20	ORIGINAL SIZE A4	 Yorkshire House York Road Little Drifffield East Yorkshire YO25 5XA Tel 01377 253617 Fax 01377 259555
		DATE 28/04/06	CHECKED JG	
PROJECT M1 WIDENING	SHEET 2 OF 4	DRAWN RFisk	APPROVED GS	
		DRAWING NUMBER 18_06093_13_Sht 2	REV A	