


DESCRIPTION		DRAFT ISSUE							
REV	B	DATE	23/07/04	BY	JN	CHKD	GS	APPD	PP
DESCRIPTION		DRAFT ISSUE - REDESIGN OF FOUNDATIONS							
REV	C	DATE	02/08/04	BY	JN	CHKD	GS	APPD	PP

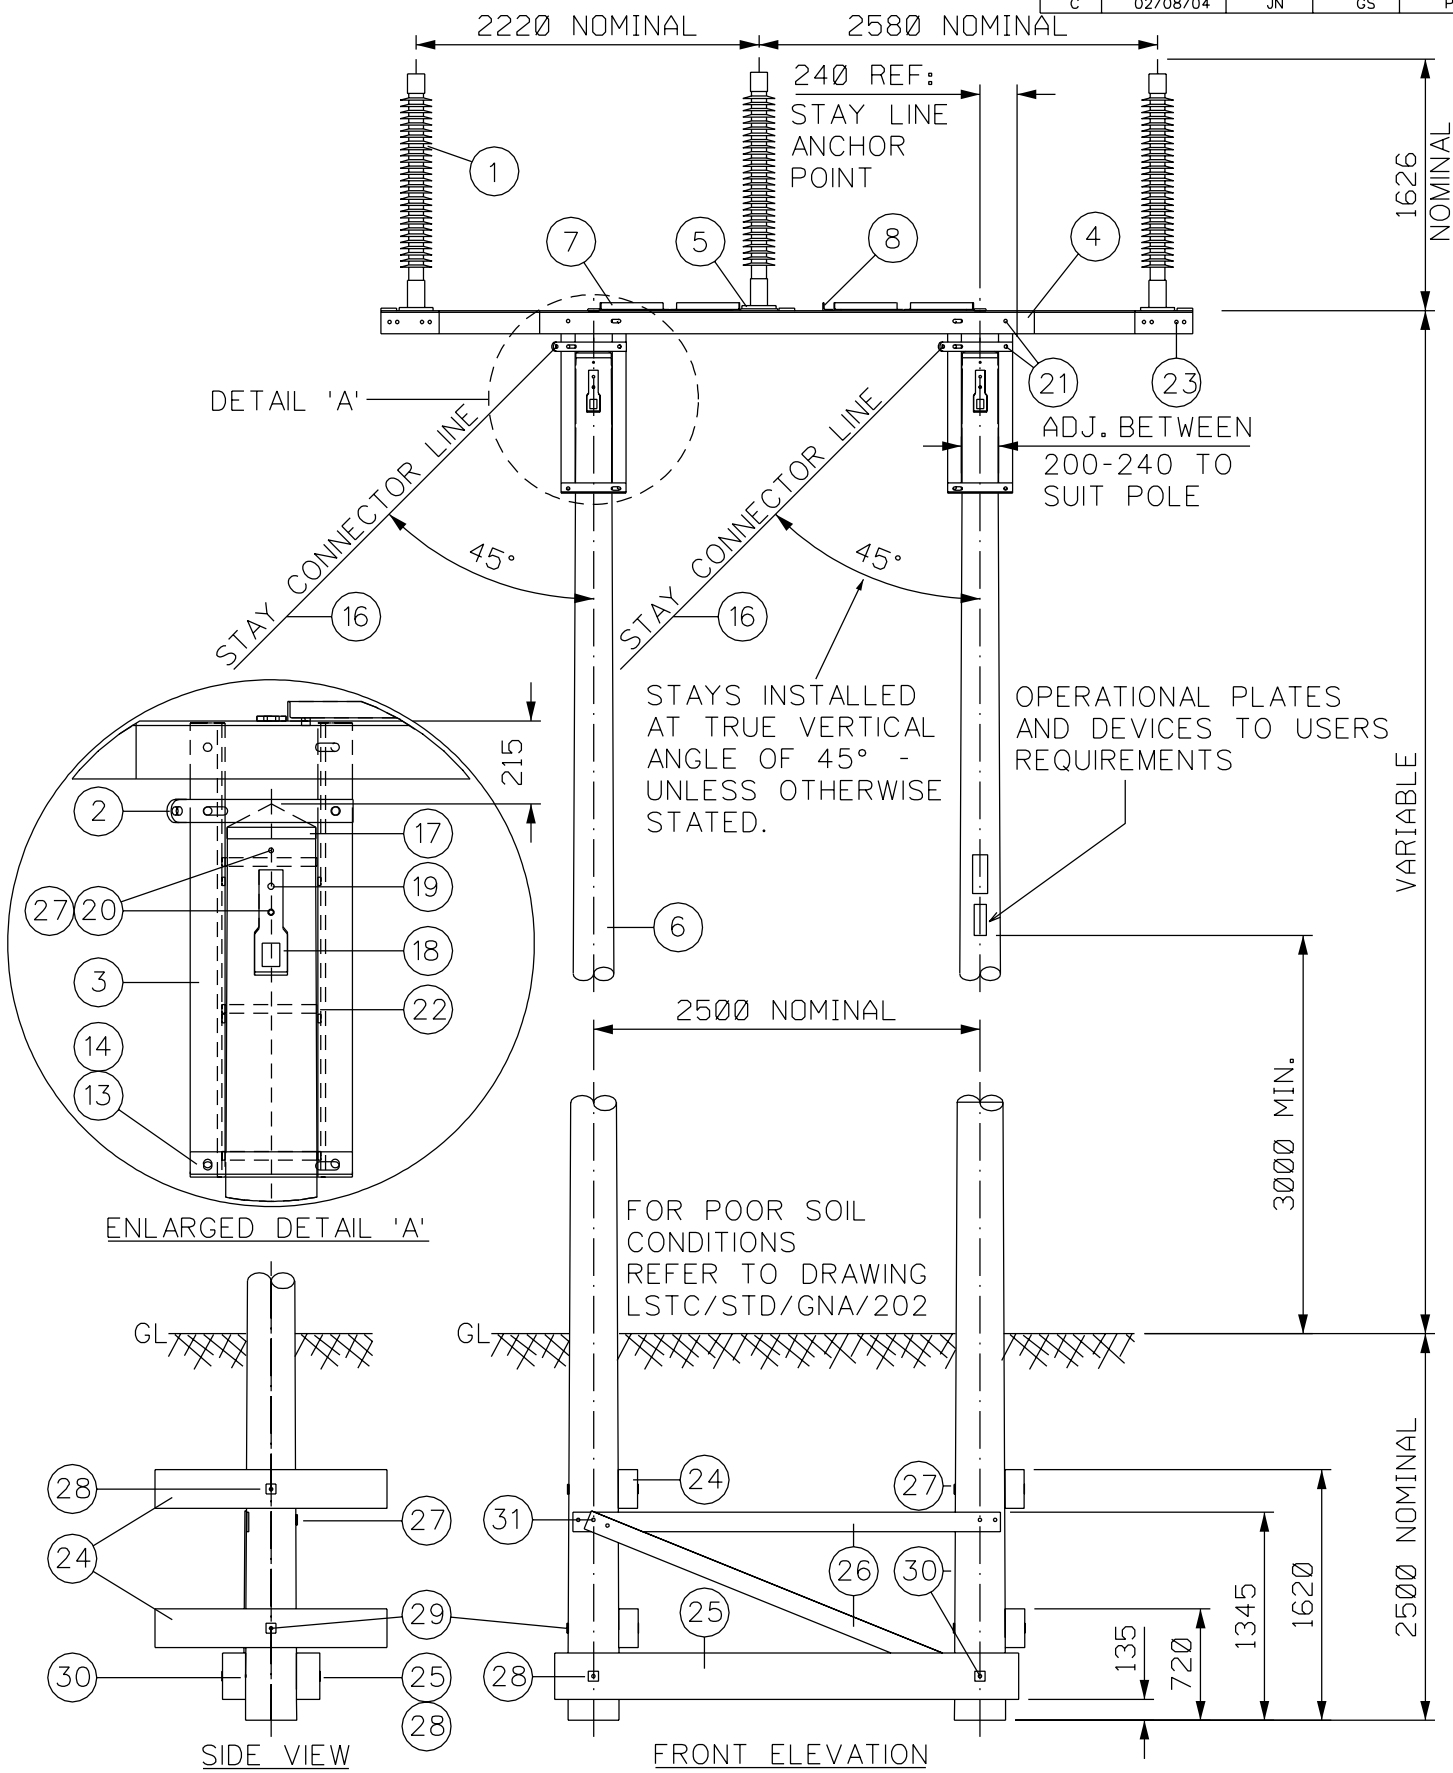

GENERAL NOTES

1. ALL STEELWORK TO BE PROTOTYPE CHECK ERECTED BEFORE MASS PRODUCTION.
2. SAFETY SIGNS INSTALLED TO SSE POWER DISTRIBUTION PROCEDURE PR-PS-325
3. DETAILS OF POSITIONS AND MOUNTING HEIGHTS FOR SIGNS AND PLATES TO SSE POWER DISTRIBUTION DRG HO/39/4400 & 4401.
4. FOR PLAN VIEW SEE LSTC/STD/GNA/13
5. FOR MATERIAL LIST SEE LSTC/STD/GNA/14

CLIENT SSE POWER DISTRIBUTION		TITLE TRIDENT 2 POLE UP TO 30° MAX ANGLE STRUCTURE	SCALE 1 : 50 (UNLESS OTHERWISE STATED)		ORIGINAL SIZE A4		LS TRANSMISSION CONSULTANCY LIMITED PADDOCK HOUSE 10 MIDDLE STREET SOUTH DRIFFIELD EAST YORKSHIRE YO25 6PT TEL: 01377 240047
PROJECT 132kV SINGLE CIRCUIT UNEARTHED OVERHEAD LINE			DATE 02/08/04		CHECKED GS		
			DRAWN JN		APPROVED PP		
			DRAWING NUMBER LSTC/STD/GNA/12		REV C		