


DESCRIPTION		FOR ISSUE				
REV	6	DATE	22/11/07	BY	RF	CHKD SP APPD GS

GENERAL NOTES

1. FOR PLAN & ISOMETRIC VIEW SEE LSTC/STD/GNA/545
2. FOR FRONT ELEVATION SEE LSTC/STD/GNA/546
3. FOR MATERIAL LIST SEE LSTC/STD/GNA/548

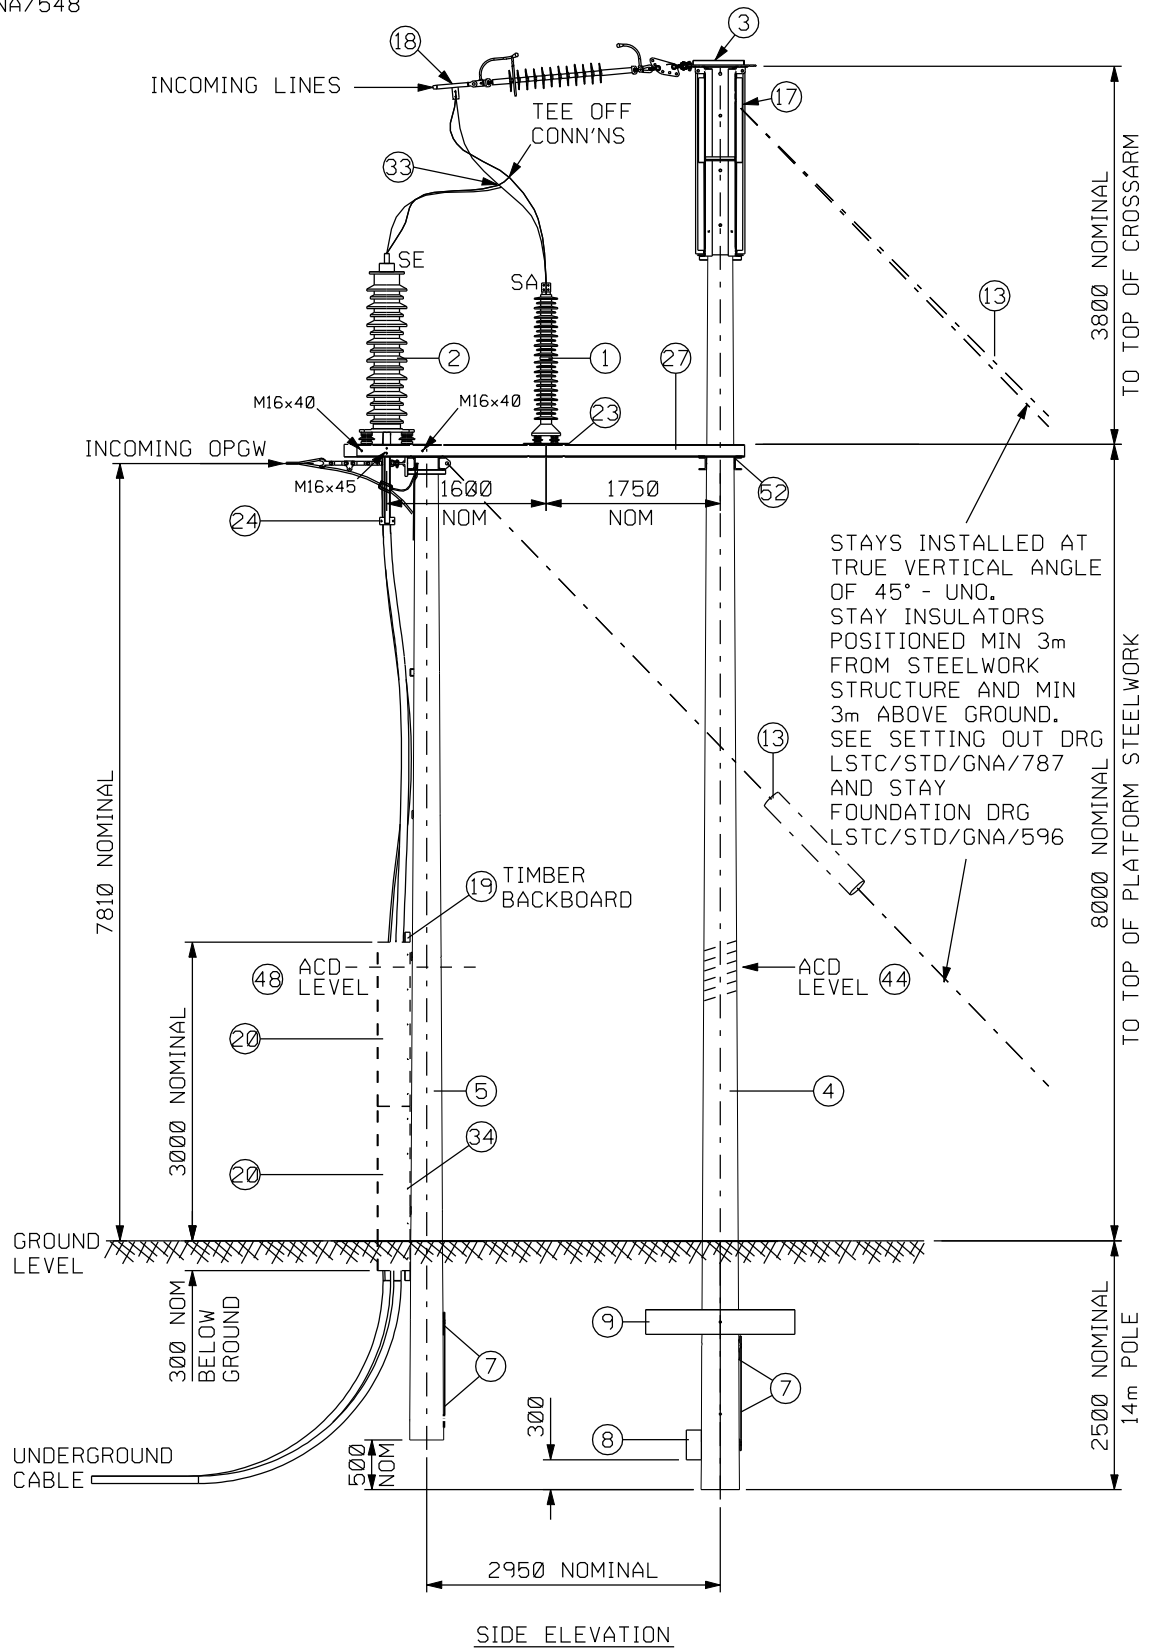

CLIENT PowerSystems	TITLE GA - SIDE ELEVATION 0° ENTRY / TERMINAL 4 POLE STRUCTURE	SCALE 1 : 75 (UNLESS OTHERWISE STATED)	ORIGINAL SIZE A4	LS TRANSMISSION CONSULTANCY LIMITED Yorkshire House York Road Little Driffield East Yorkshire YO25 5XA 01377 253617
		DATE 26/01/05	CHECKED GS	
DRAWN R.T.J		APPROVED PP		
DRAWING NUMBER LSTC/STD/GNA/547		REV 6		
SPECIFICATION OHL-03-132				