
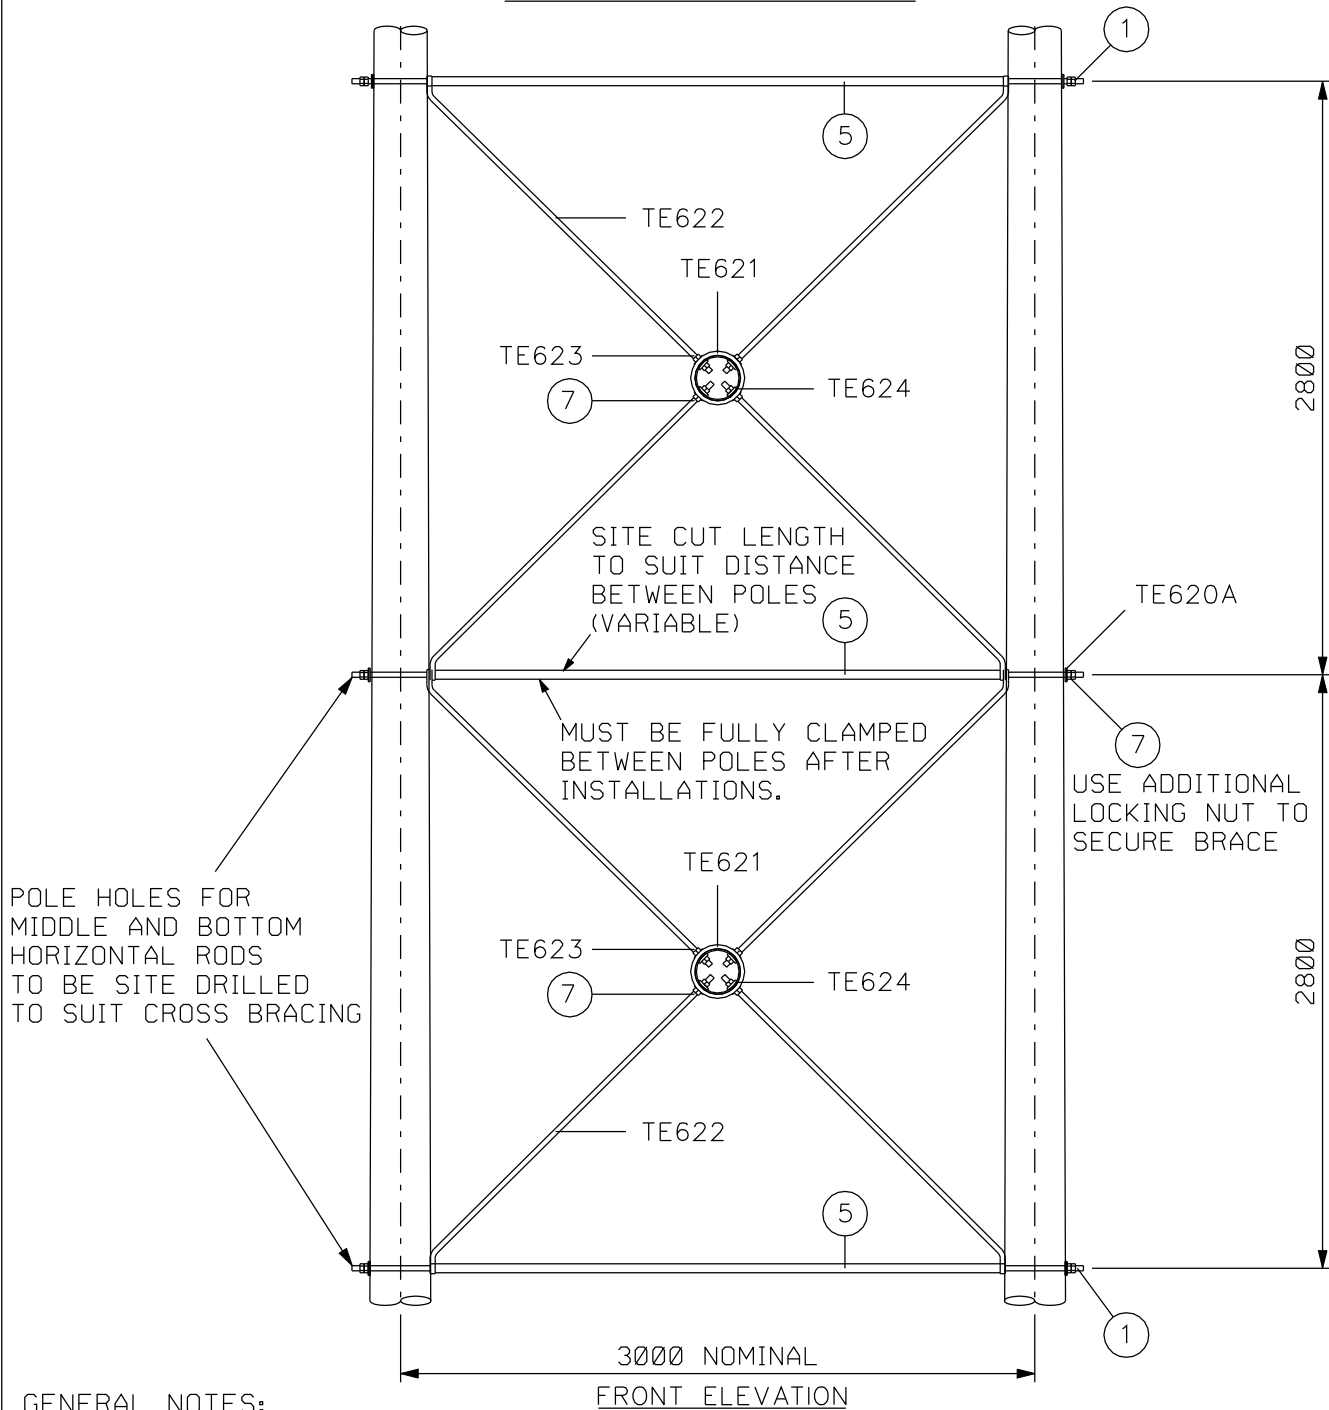


DESCRIPTION		FOR ISSUE			
REV	DATE	BY	CHKD	APPD	PP
3	03/08/07	JR	GS	PP	

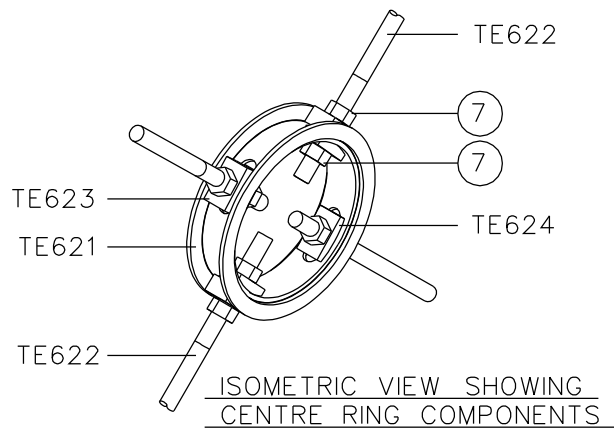

GENERAL NOTES:

1. ALL STEELWORK TO BE PROTOTYPE CHECK
ERECTED BEFORE MASS PRODUCTION.
2. FOR MATERIAL LIST SEE LSTC/STD/GNA/559

CLIENT	TITLE GA - WOOD POLE BRACE ASSEMBLY DOUBLE	SCALE 1:33.33 (UNLESS OTHERWISE STATED)	ORIGINAL SIZE A4	LS TRANSMISSION CONSULTANCY LIMITED Yorkshire House York Road Little Driffield East Yorkshire YO25 5XA 01377 253617
PowerSystems		DATE 01/12/04	CHECKED GS	
SPECIFICATION		DRAWN R.T.J	APPROVED PP	
OHL-03-132		DRAWING NUMBER LSTC/STD/GNA/558	REV 3	