


DESCRIPTION		FOR ISSUE			
REV	DATE	BY	CHKD	APPD	PP
6	13/08/07	JR	GS	PP	

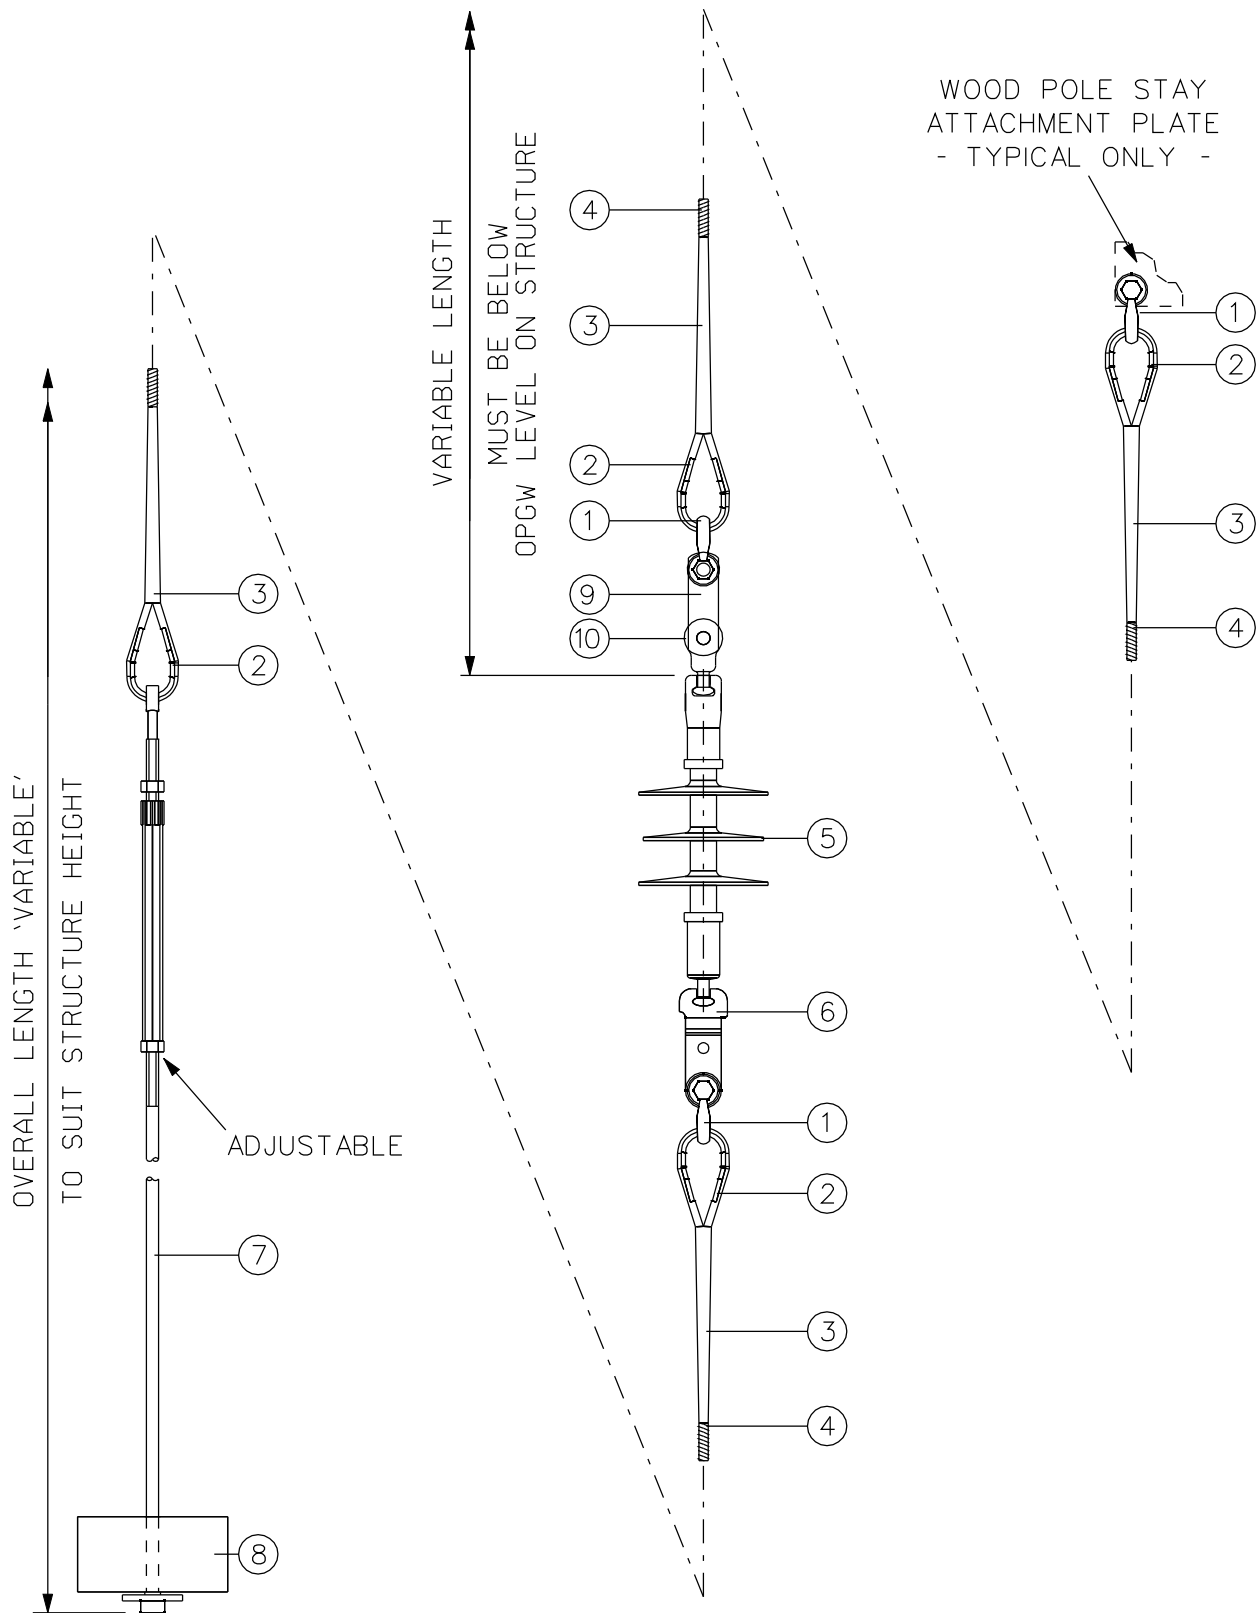

FOR MATERIAL LIST SEE LSTC/STD/GNA/561

CLIENT PowerSystems	TITLE STAY - INSULATED ASSEMBLY GA 101kN MFL	SCALE 1 : 12.5 (UNLESS OTHERWISE STATED)	ORIGINAL SIZE A4	LS TRANSMISSION CONSULTANCY LIMITED Yorkshire House York Road Little Driffield East Yorkshire YO25 5XA 01377 253617 	
		DATE 24/11/04	CHECKED RTJ		
SPECIFICATION OHL-03-132		DRAWN JN	APPROVED PP		
		DRAWING NUMBER LSTC/STD/GNA/560			REV 6