



DESCRIPTION		FOR ISSUE			
REV	DATE	BY	CHKD	APPD	GS
5	22/11/07	RF	SP	GS	

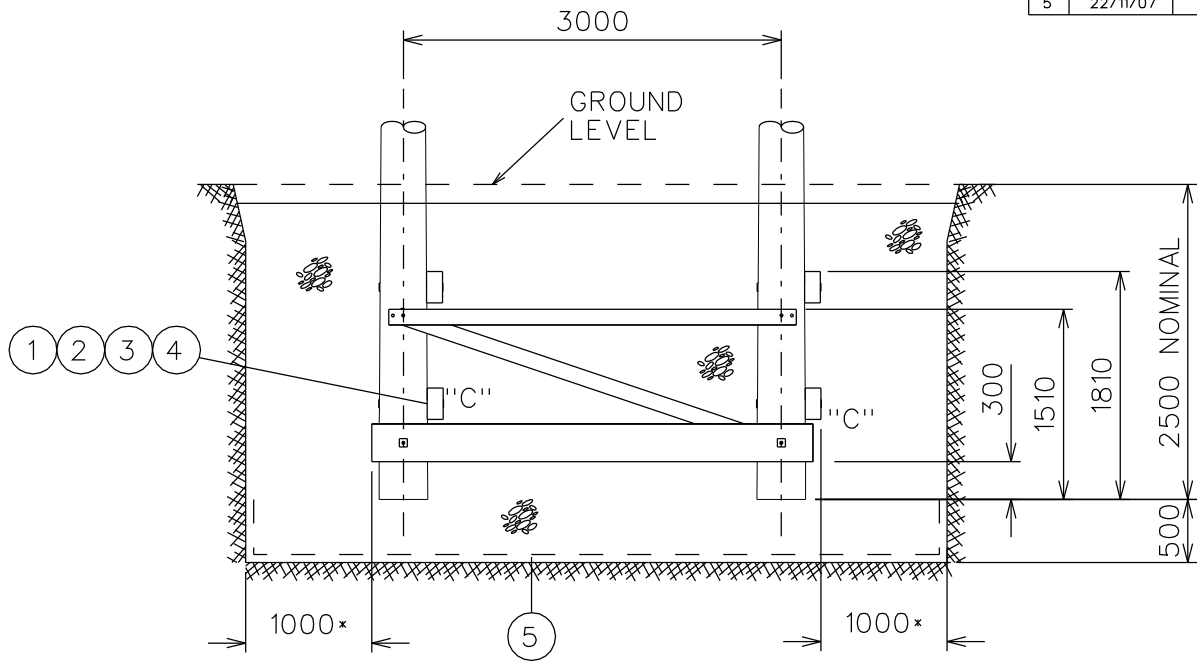

14M POLE FRONT ELEVATION

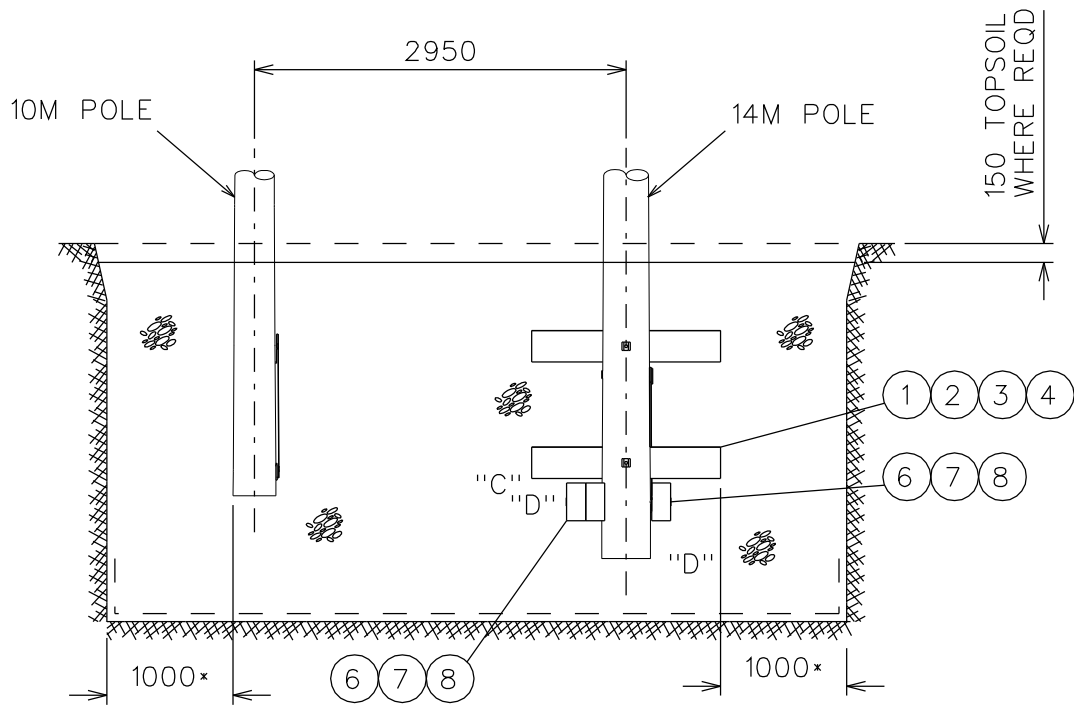

SIDE ELEVATION

* MINIMUM DISTANCE BETWEEN FACE OF EXCAVATION AND STRUCTURE
TO ALLOW ACCESS TO PLACE GRANULAR FILL & COMPACT

FOR GENERAL NOTES & MATERIAL LIST SEE LSTC/STD/GNA/814 SHEET 2

CLIENT PowerSystems	TITLE ADDITIONAL MATERIAL - 4 POLE TERMINAL FOR VERY POOR SOIL CONDITIONS SHT 1 OF 2	SCALE 1:60 (UNLESS OTHERWISE STATED)	ORIGINAL SIZE A4	LS TRANSMISSION CONSULTANCY LIMITED Yorkshire House York Road Little Driffield East Yorkshire YO25 5XA 01377 253617	
		DATE 16/05/05	CHECKED GS		
SPECIFICATION OHL-03-132		DRAWN R.F.	APPROVED PP		
		DRAWING NUMBER LSTC/STD/GNA/814			REV 5