
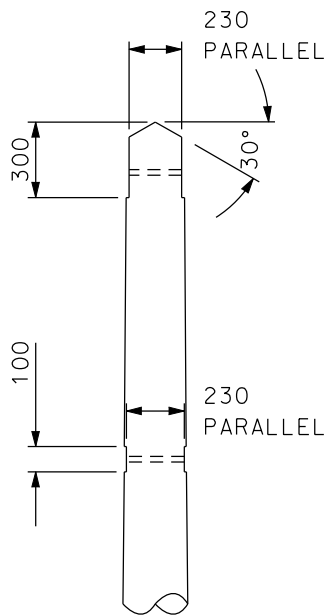


GENERAL NOTES:

1. ALL DIMENSIONS ARE IN mm, UNLESS NOTED
2. ALL DRILLINGS TO BE 22mm DIAMETER HOLES
3. POLE SIZES BASED ON BS1990, STOUT POLES RANGE
LENGTH = 9m
MINIMUM TOP DIAMETER = 235mm
MINIMUM DIAMETER 1.5m FROM BUTT = 275mm

POLE SCARFED ON
BOTH SIDES TO GIVE
MIN 50mm FLAT FACE

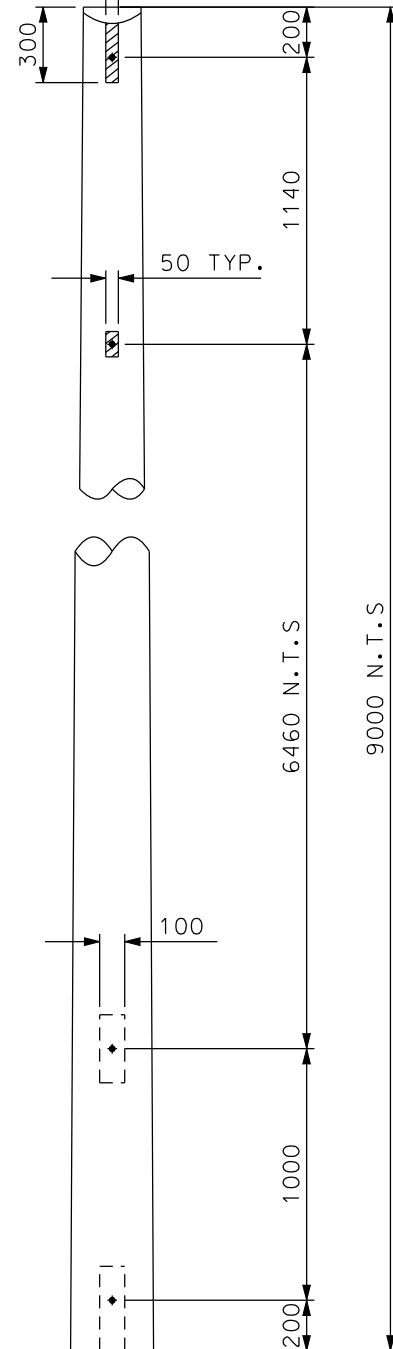

POLE SIZE TO BE
IMPRESSED
ON THE BUTT

REFERENCE

- 9 - POLE LENGTH
275 - POLE DIAMETER AT
1.5m FROM BUTT
1F - IMPORTED REDFIR
75 - YEAR OF CREOSOTING
XYZ - SUPPLIERS NAME OR MARK
GOUGE MARK 6 WIDE x 6 DEEP
3m FROM POLE BUTT

CLIENT
SSE POWER DISTRIBUTION

PROJECT
TG-PS-525 STRUCTURE
SMALL PIECE DETAIL

TITLE
WOOD POLE SCARFING
4 POLE STRUCTURE
WITH CVTs & LINE TRAPS

SCALE 1 : 30
(UNLESS OTHERWISE STATED)
DATE 26/04/05
DRAWN JN
DRAWING NUMBER LSTC_STD_PAR_254

ORIGINAL SIZE A4
CHECKED GS
APPROVED PP
REV 1

LS TRANSMISSION CONSULTANCY LIMITED
PADDOCK HOUSE
10 MIDDLE STREET SOUTH
DRIFFIELD
EAST YORKSHIRE YO25 6PT
TEL: 01377 259500

