


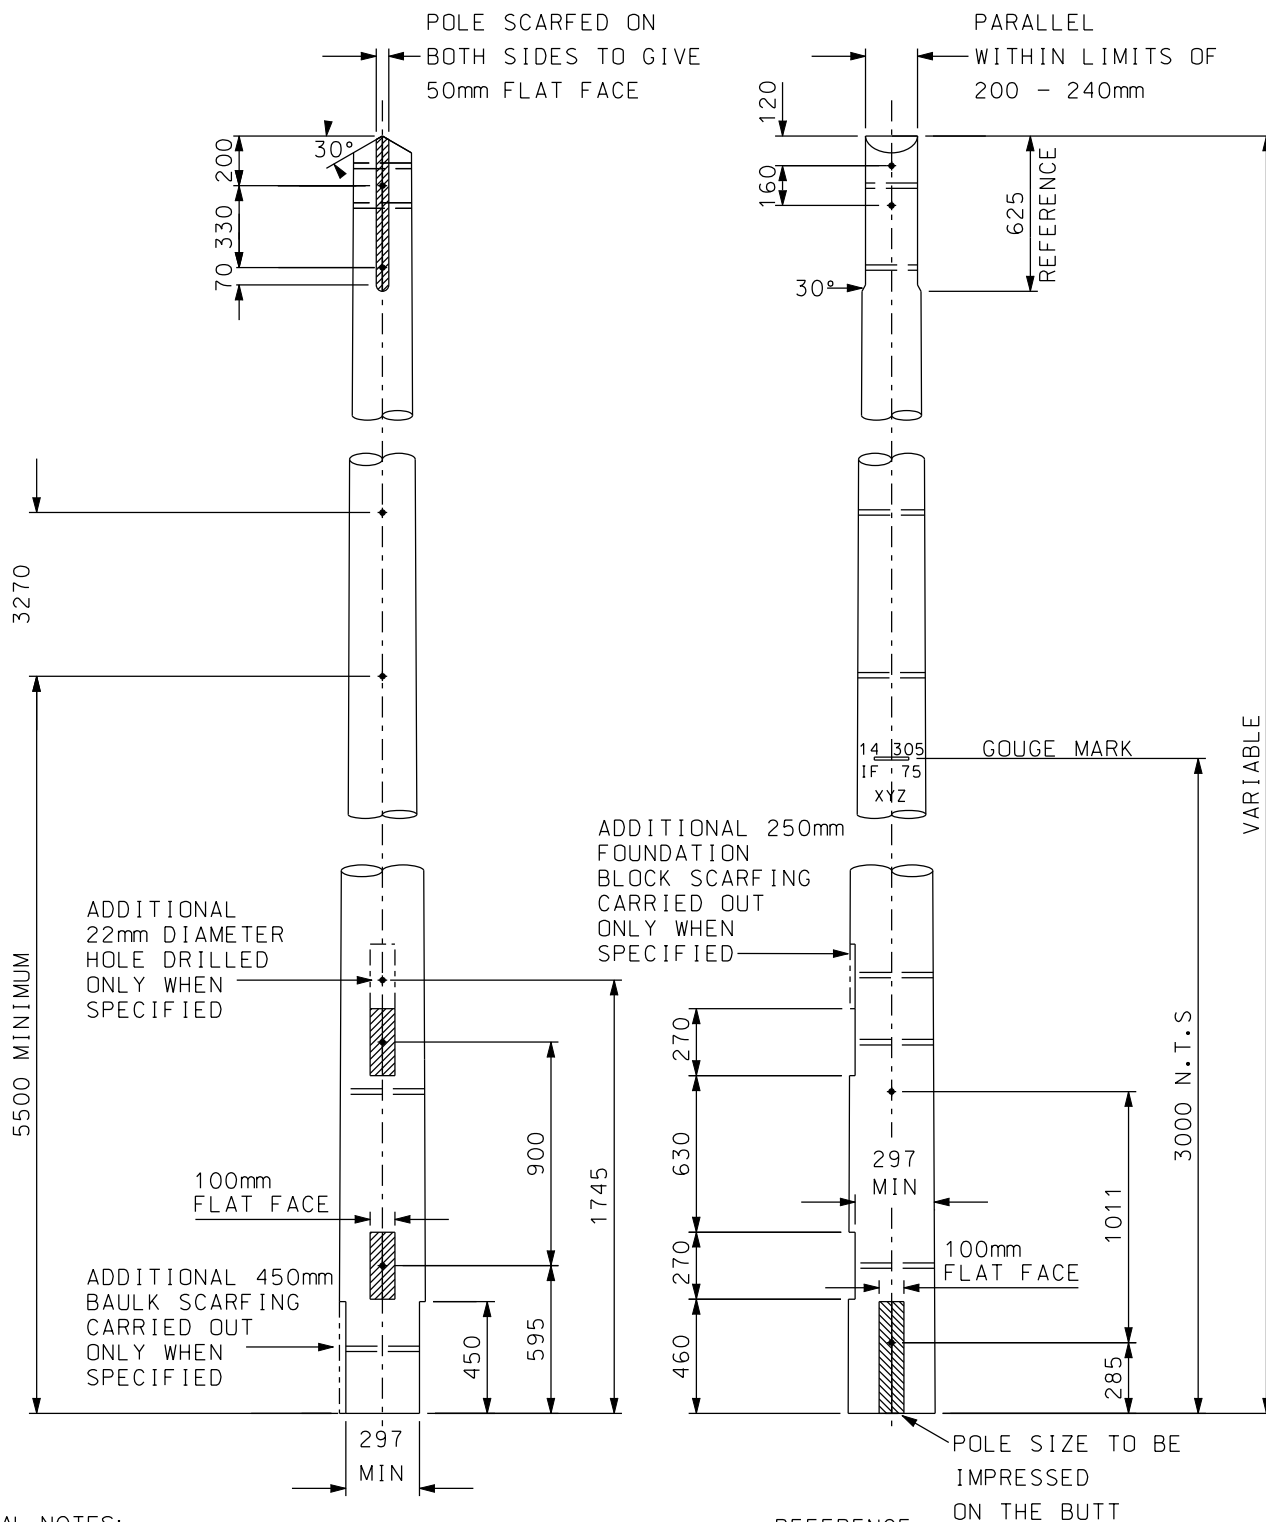

GENERAL NOTES:

- ALL DIMENSIONS ARE IN mm, UNLESS NOTED
- ALL DRILLINGS TO BE 22mm DIAMETER HOLES
- POLE SIZES BASED ON BS1990, EXTRA STOUT POLES RANGE
LENGTH = 10.5m - 16m REFER TO PROJECT SPECIFICATION
MINIMUM TOP DIAMETER = 200mm*
MAXIMUM TOP DIAMETER = 265mm
MINIMUM DIAMETER 1.5m FROM BUTT = 305mm
* VALUE AMENDED FROM THAT SHOWN ON BS1990

REFERENCE

- 14 - POLE LENGTH
305 - POLE DIAMETER AT 1.5m FROM BUTT
IF - IMPORTED REDFIR
75 - YEAR OF CREOSOTING
XYZ - SUPPLIERS NAME OR MARK
GOUGE MARK 6 WIDE x 6 DEEP 3m FROM POLE BUTT

CLIENT
SSE POWER DISTRIBUTION

PROJECT
TG-PS-525 STRUCTURE
SMALL PIECE DETAIL

TITLE
WOOD POLE SCARFING
FOR INTERMEDIATE
STRUCTURES

SCALE 1:30
(UNLESS OTHERWISE STATED)
DATE 02/08/04
DRAWN JN
DRAWING NUMBER LSTC_STD_PAR_33

ORIGINAL SIZE A4
CHECKED GS
APPROVED PP
REV 1



Yorkshire House
York Road
Little Driffield
East Yorkshire
YO25 5XA
Tel 01377 253617
Fax 01377 259555