


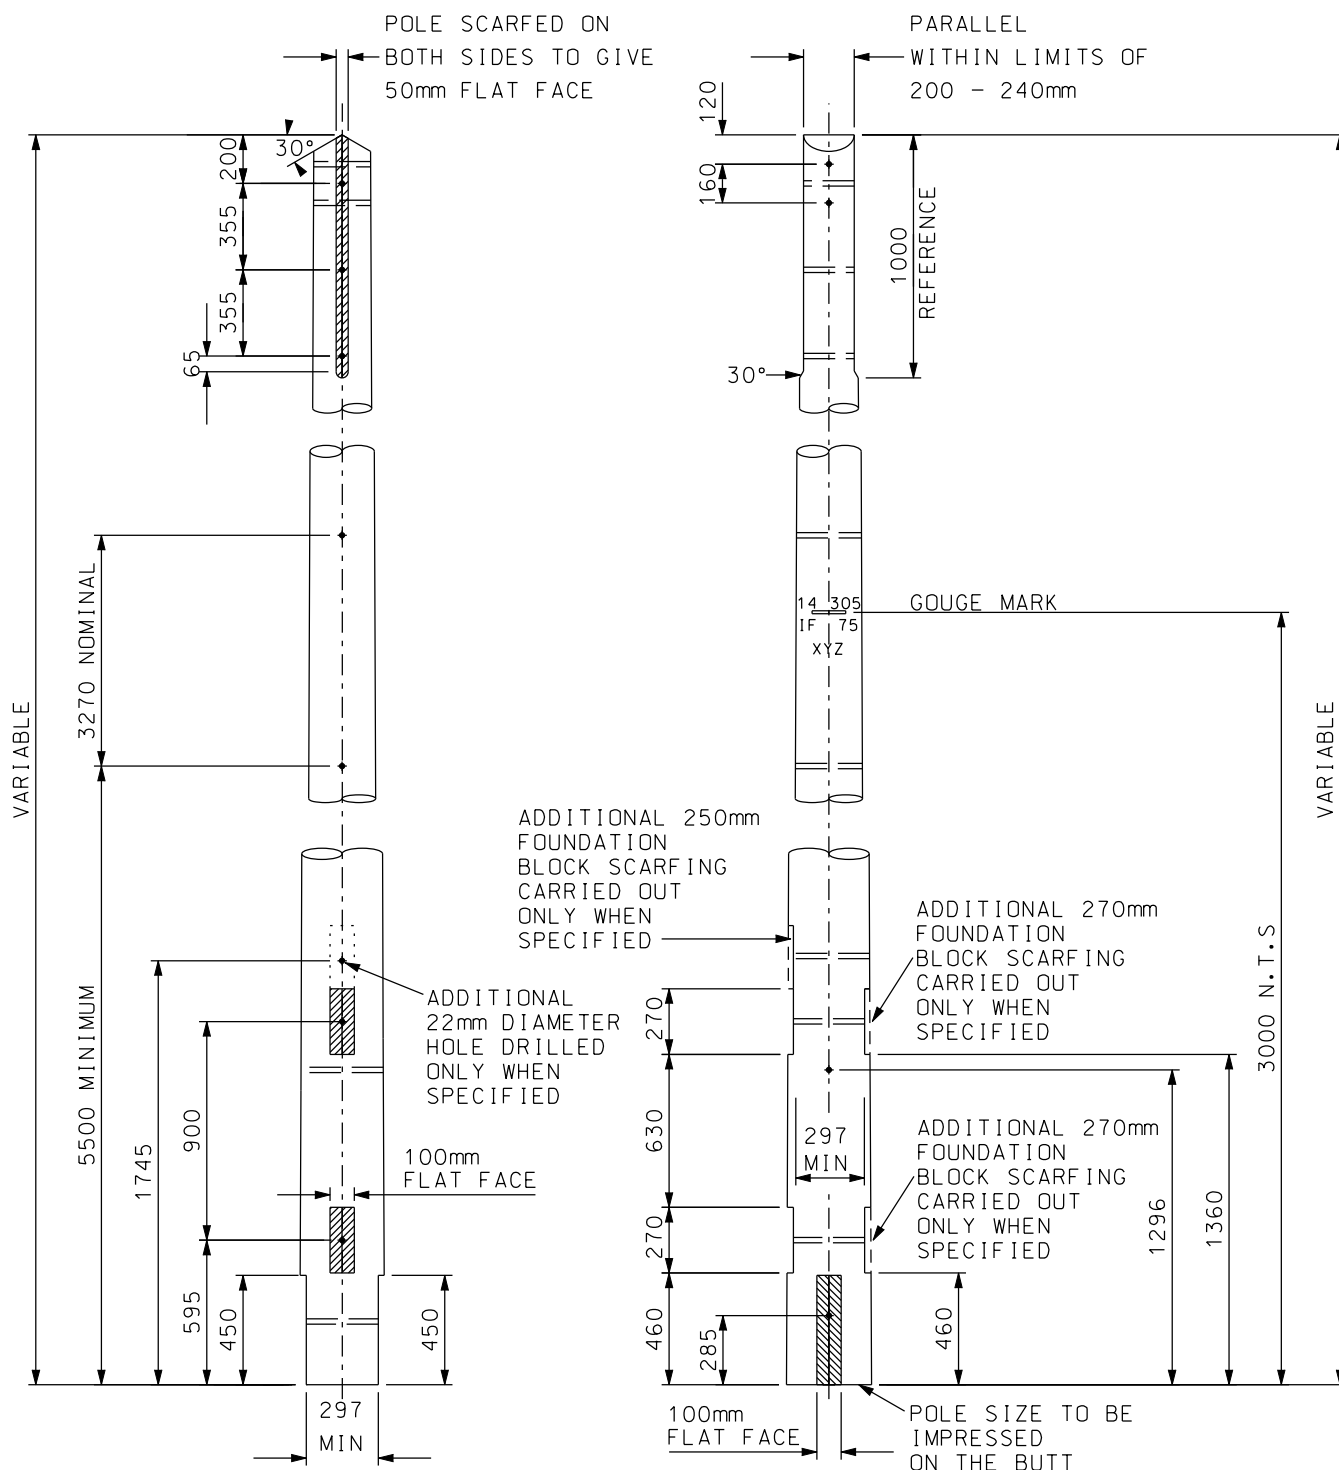

GENERAL NOTES:

1. ALL DIMENSIONS ARE IN mm, UNLESS NOTED
2. ALL DRILLINGS TO BE 22mm DIAMETER HOLES
3. POLE SIZES BASED ON BS1990, EXTRA STOUT POLES RANGE
LENGTH = 11m - 13m - REFER TO PROJECT SPECIFICATION
MINIMUM TOP DIAMETER = 200mm *
MAXIMUM TOP DIAMETER = 265mm
MINIMUM DIAMETER 1.5m FROM BUTT = 305mm
* VALUE AMENDED FROM THAT SHOWN ON BS1990

REFERENCE

- 14 - POLE LENGTH
305 - POLE DIAMETER AT 1.5m FROM BUTT
IF - IMPORTED REDFIR
75 - YEAR OF CREOSOTING
XYZ - SUPPLIERS NAME OR MARK
GOUGE MARK 6 WIDE x 6 DEEP
3m FROM POLE BUTT

CLIENT	TITLE	SCALE	ORIGINAL SIZE	 Yorkshire House York Road Little Driffield East Yorkshire YO25 5XA Tel 01377 253617 Fax 01377 259555
SSE POWER DISTRIBUTION	WOOD POLE SCARFING UNBRACED ANGLED STRUCTURES	(UNLESS OTHERWISE STATED)	A4	
PROJECT		DATE	CHECKED	
IG-PS-525 STRUCTURE		02/08/04	GS	
SMALL PIECE DETAIL		DRAWN	APPROVED	
		JN	PP	
		DRAWING NUMBER	REV	
		LSTC_STD_PAR_50	1	