


H POLE
FOUNDATION TIMBER BAULK
300x150x3500
(net weight 135kg)

DESCRIPTION		DRAFT ISSUE			
REV	DATE	BY	CHKD	APPD	PP
1	23/11/04	JN	GS		

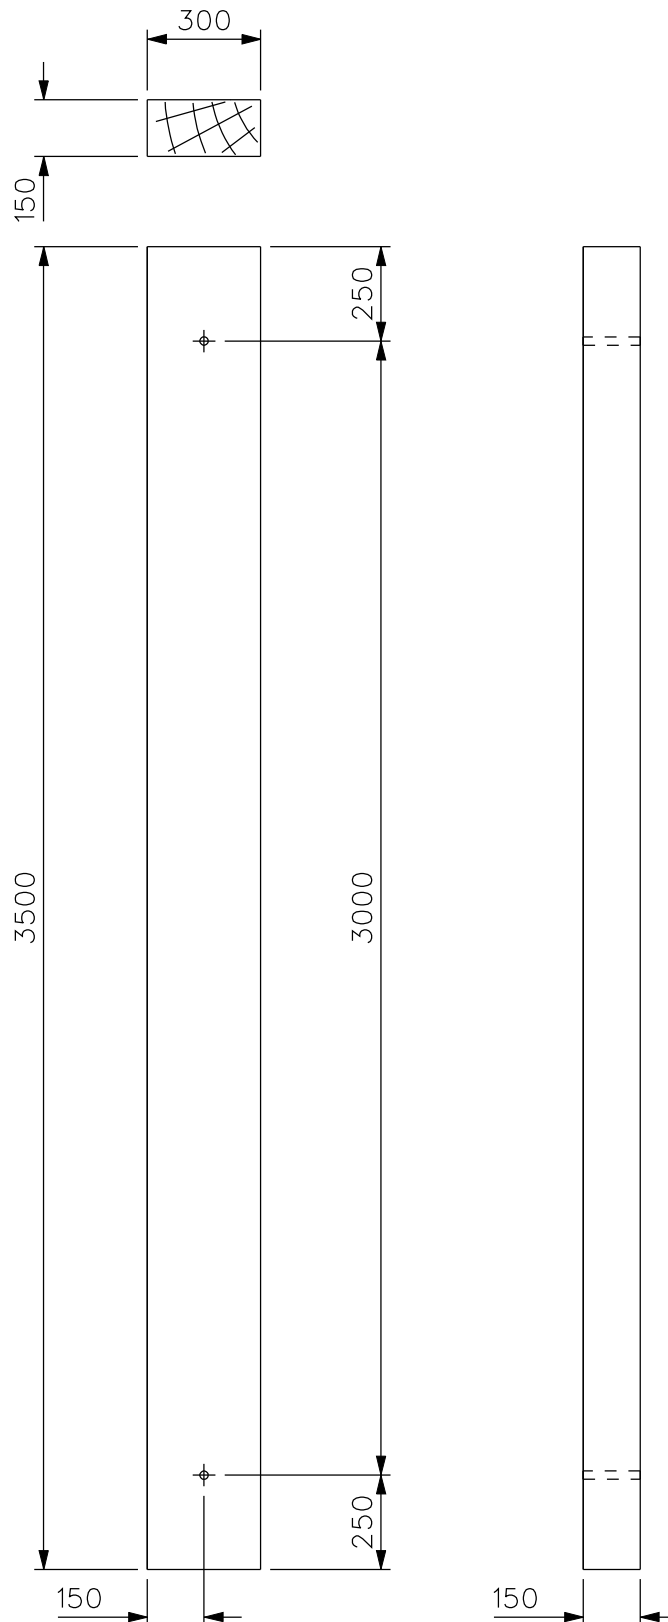

GENERAL NOTES:

1. ALL DIMENSIONS IN MILLIMETERS (mm)
2. ALL HOLES 22mm DIAMETER (unless noted)
3. MEMBER TO BE CLEARLY MARKED WITH
PREFIX 'TE' AND ITEM NUMBER FOR
SITE IDENTIFICATION

BAR MARK / ITEM NUMBER
TE601

CLIENT PowerSystems	TITLE SMALL PIECE DETAIL H POLE FOUNDATION TIMBER BAULK	SCALE 1 : 20 (UNLESS OTHERWISE STATED)	ORIGINAL SIZE A4	LS TRANSMISSION CONSULTANCY LIMITED Yorkshire House York Road Little Driffield East Yorkshire YO25 5XA 01377 253617	
		DATE 23/11/04	CHECKED GS		
PROJECT NEW TRIDENT DESIGN		DRAWN JN	APPROVED PP		
		DRAWING NUMBER LSTC/STD/PAR/601			REV 1