
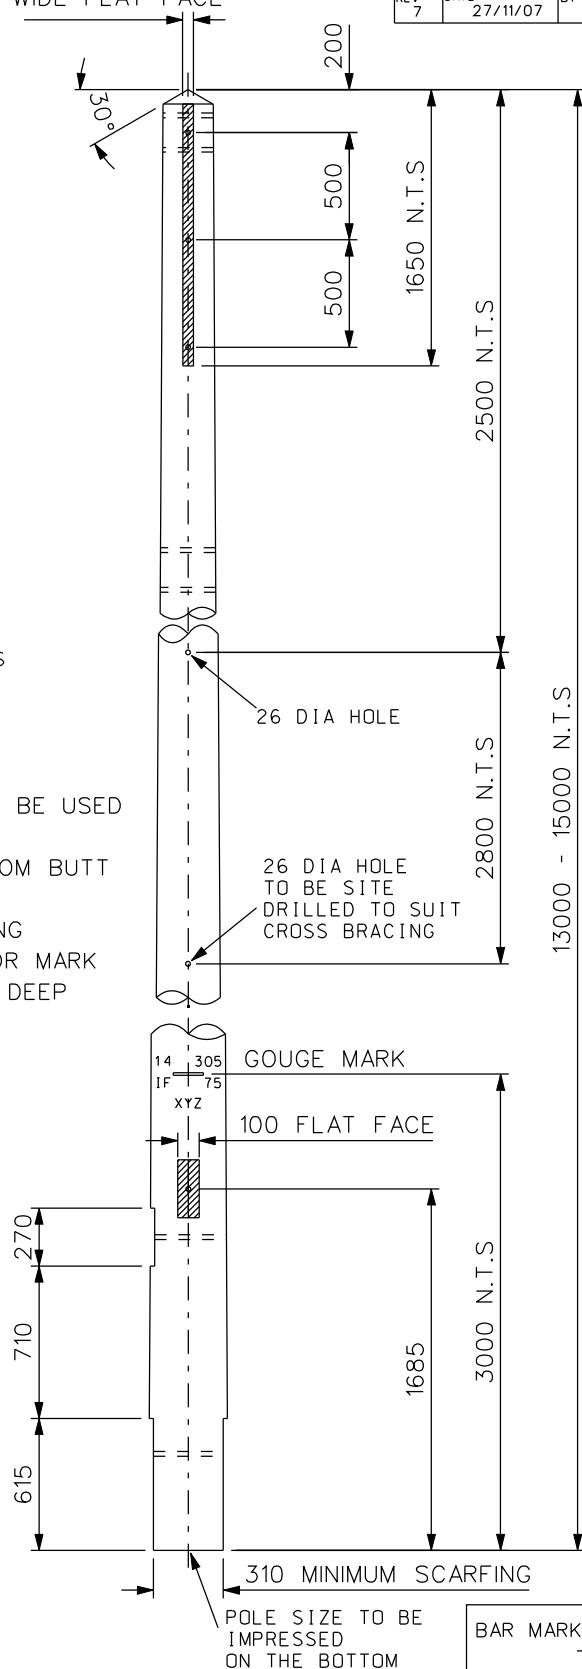


USED ON LSTC/STD/GNA/542

POLE SCARFED PARALLEL ON BOTH SIDES TO GIVE 50mm WIDE FLAT FACE

| DESCRIPTION |          | FOR ISSUE |    |      |    |      |
|-------------|----------|-----------|----|------|----|------|
| REV         | DATE     | BY        | RF | CHKD | SP | APPD |
| 7           | 27/11/07 |           |    |      |    | GS   |

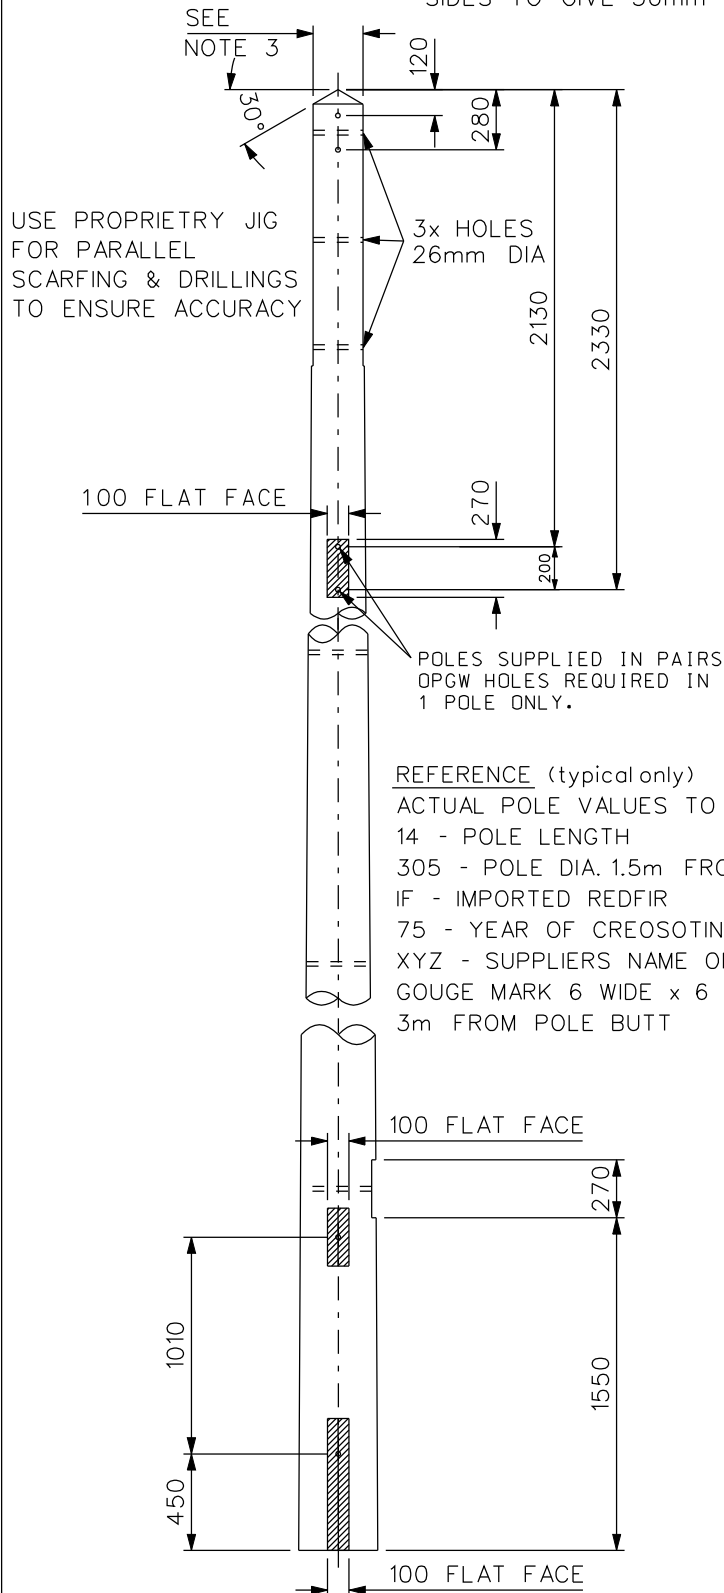

GENERAL NOTES:

1. ALL DIMENSIONS ARE IN mm, UNLESS NOTED
2. ALL DRILLINGS TO BE 24mm DIAMETER HOLES UNO.
3. POLE SIZES BASED ON BS1990, EXTRA STOUT POLES RANGE  
 LENGTH = 13m - 15m & PARALLEL WITHIN LIMITS  
 \* MINIMUM TOP DIST BETWEEN FLATS = 200mm  
 \* MAXIMUM TOP DIST BETWEEN FLATS = 265mm  
 MINIMUM DIAMETER 1.5m FROM BUTT = 305mm

SUPPLIER TO NOTE THESE DIMENSIONS ARE FOR GENERIC POLE DRILLING AND SCARFING ONLY TO SUIT A RANGE OF POLE SIZES, ACTUAL POLE MINIMUM DIMENSIONS TO BE SPECIFIED AT TIME OF ORDERING. ORDER VALUES WILL SUPERSEDE THESE STATED VALUES. MAXIMUM VALUE NOT TO BE EXCEEDED

BAR MARK / ITEM NUMBER  
TE650

|               |              |
|---------------|--------------|
| CLIENT        | PowerSystems |
| SPECIFICATION | OHL-03-132   |

|       |                                                                |
|-------|----------------------------------------------------------------|
| TITLE | PART -<br>WOOD POLE<br>SCARFING DETAILS -<br>SECTION STRUCTURE |
|-------|----------------------------------------------------------------|

|                |                                     |               |    |
|----------------|-------------------------------------|---------------|----|
| SCALE          | 1 : 35<br>(UNLESS OTHERWISE STATED) | ORIGINAL SIZE | A4 |
| DATE           | 17/01/05                            | CHECKED       | GS |
| DRAWN          | JN                                  | APPROVED      | PP |
| DRAWING NUMBER | LSTC/STD/PAR/650                    | REV           | 7  |

LS TRANSMISSION CONSULTANCY LIMITED  
 Yorkshire House  
 York Road  
 Little Driffield  
 East Yorkshire  
 YO25 5XA  
 01377 253617

