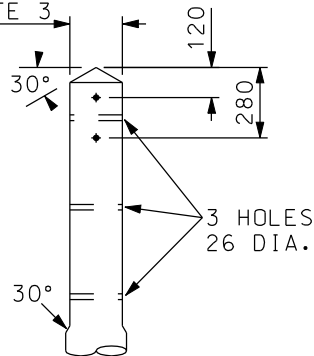
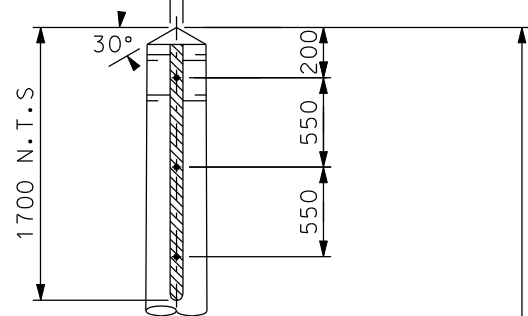
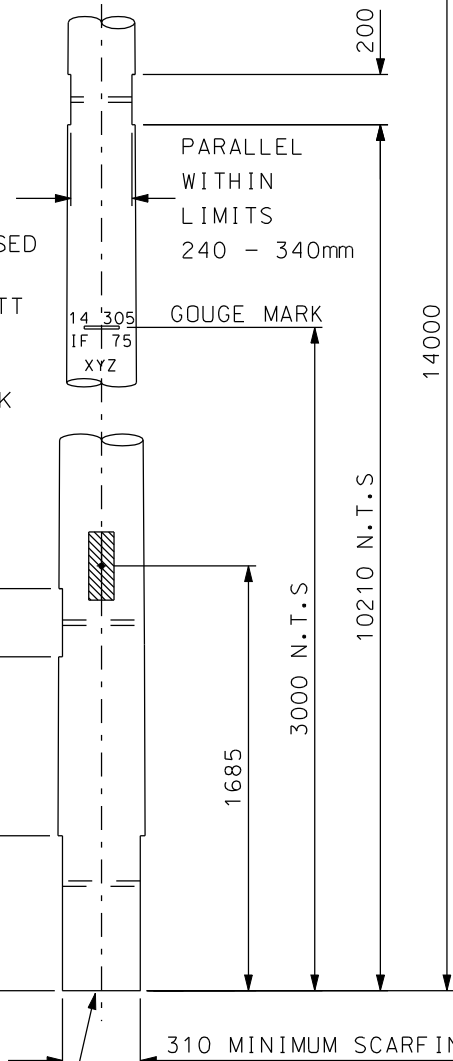
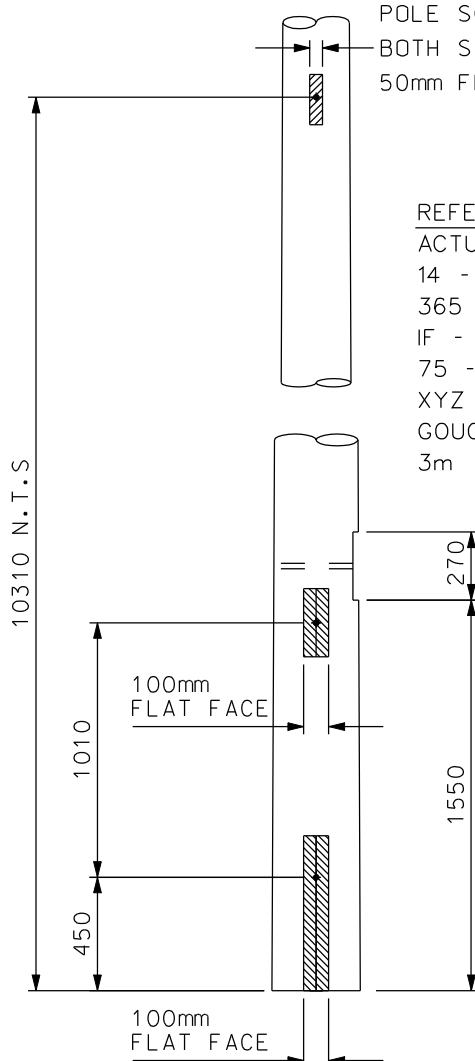


FOR
INFORMATIONPARALLEL SCARFED
USING
PROPRIETARY JIG* SEE
NOTE 3POLE SCARFED ON
BOTH SIDES TO GIVE
50mm FLAT FACEPOLE SCARFED ON
BOTH SIDES TO GIVE
50mm FLAT FACE

REFERENCE (typical only)
ACTUAL POLE VALUES TO BE USED
14 - POLE LENGTH
365 - POLE DIA. 1.5m FROM BUTT
IF - IMPORTED REDFIR
75 - YEAR OF CREOSOTING
XYZ - SUPPLIERS NAME OR MARK
GOUGE MARK 6 WIDE x 6 DEEP
3m FROM POLE BUTT

POLE SIZE TO BE
IMPRESSED
ON THE BUTTBAR MARK / ITEM NUMBER
TE710

GENERAL NOTES:

1. ALL DIMENSIONS ARE IN mm, UNLESS NOTED
2. ALL DRILLINGS TO BE 24mm DIAMETER HOLES
3. POLE SIZES BASED ON BS1990, EXTRA STOUT POLES

RANGE

LENGTH = 14m & PARALLEL WITHIN LIMITS

* MINIMUM TOP DIST BETWEEN FLATS = 200mm

* MAXIMUM TOP DIST BETWEEN FLATS = 265mm

MINIMUM DIAMETER 1.5m FROM BUTT = 305mm

SUPPLIER TO NOTE THESE DIMENSIONS ARE FOR GENERIC POLE
DRILLING AND SCARFING ONLY TO SUIT A RANGE OF POLE SIZES,
ACTUAL POLE MINIMUM DIMENSIONS TO BE SPECIFIED AT TIME
OF ORDERING. ORDER VALUES WILL SUPERSEDE THESE STATED
VALUES. MAXIMUM VALUE NOT TO BE EXCEEDED

CLIENT
PowerSystemsSPECIFICATION
OHL-03-132

TITLE
PART -
WOOD POLE SCARFING
4 POLE ENTRY TERMINAL
STRUCTURES
14m POLE

SCALE 1:30

(UNLESS OTHERWISE STATED)

DATE 27/01/05

DRAWN R.T.J

DRAWING NUMBER

LSTC/STD/PAR/710

ORIGINAL SIZE A4

CHECKED GS

APPROVED PP

REV 4

LS TRANSMISSION CONSULTANCY LIMITED
Yorkshire House
York Road
Little Driffield
East Yorkshire
YO25 5XA
01377 253617

