


DESCRIPTION		REV'D BAULK POSITIONS					
REV	DATE	BY	RF	CHKD	GS	APPD	PP
3	07/11/05						

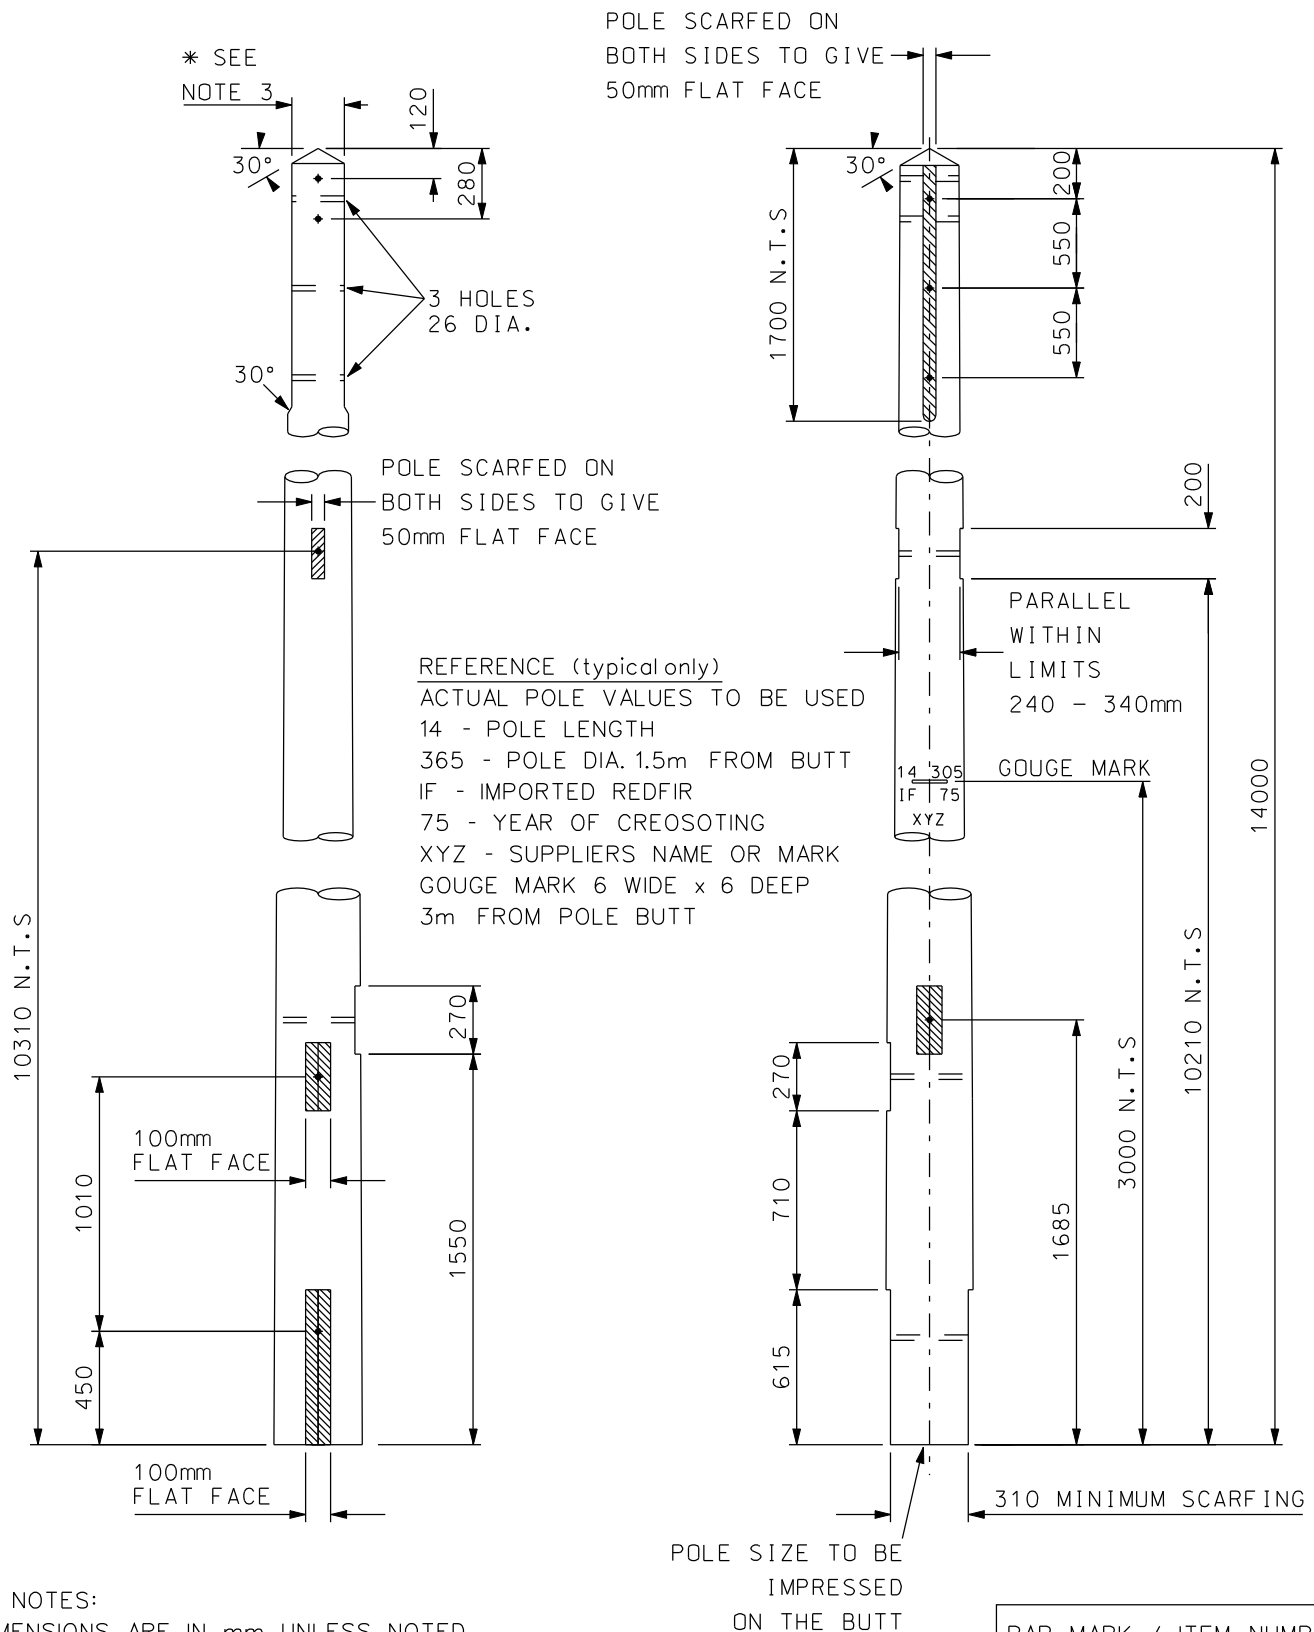

GENERAL NOTES:

- ALL DIMENSIONS ARE IN mm, UNLESS NOTED
- ALL DRILLINGS TO BE 22mm DIAMETER HOLES
- POLE SIZES BASED ON BS1990, EXTRA STOUT POLES

RANGE

LENGTH = 14m

* MINIMUM TOP DIST BETWEEN FLATS = 200mm

* MAXIMUM TOP DIST BETWEEN FLATS = 265mm

MINIMUM DIAMETER 1.5m FROM BUTT = 305mm

SUPPLIER TO NOTE THESE DIMENSIONS ARE FOR GENERIC POLE DRILLING AND SCARFING ONLY TO SUIT A RANGE OF POLE SIZES, ACTUAL POLE MINIMUM AND MAXIMUM DIMENSIONS TO BE SPECIFIED AT TIME OF ORDERING. ORDER VALUES WILL SUPERSEDE THESE STATED VALUES.

CLIENT PowerSystems	TITLE WOOD POLE SCARFING 4 POLE ENTRY TERMINAL STRUCTURES 14m POLE	SCALE 1:30 (UNLESS OTHERWISE STATED)	ORIGINAL SIZE A4	LS TRANSMISSION CONSULTANCY LIMITED Yorkshire House York Road Little Driffield East Yorkshire YO25 5XA 01377 253617
PROJECT NEW TRIDENT DESIGN		DATE 27/01/05	CHECKED GS	
		DRAWN R.T.J	APPROVED PP	
		DRAWING NUMBER LSTC/STD/PAR/710		