


H POLE
FOUNDATION TIMBER BAULK
300x150x4000
(net weight 154kg)

DESCRIPTION		DRAFT ISSUE			
REV	DATE	BY	CHKD	APPD	
1	06/05/2005	RF	GS	PP	

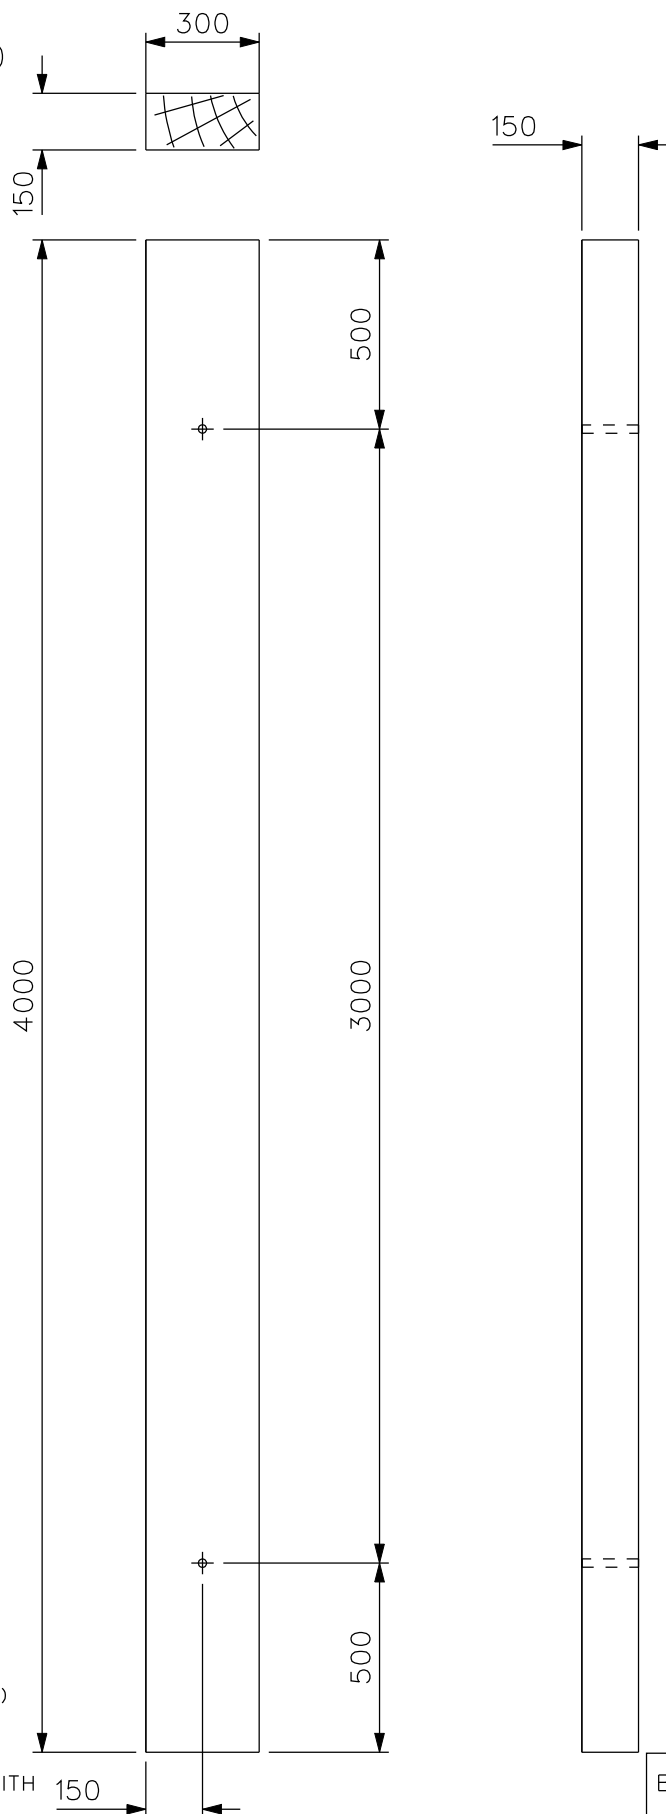

- GENERAL NOTES:
1. ALL DIMENSIONS IN MILLIMETERS (mm)
 2. ALL HOLES 22mm DIAMETER (unless noted)
 3. MEMBER TO BE CLEARLY MARKED WITH PREFIX 'TE' AND ITEM NUMBER FOR SITE IDENTIFICATION

BAR MARK / ITEM NUMBER
TE731

CLIENT PowerSystems	TITLE SMALL PIECE DETAIL H POLE FOUNDATION TIMBER BAULK	SCALE 1 : 20 (UNLESS OTHERWISE STATED)	ORIGINAL SIZE A4	 LS TRANSMISSION CONSULTANCY LIMITED Yorkshire House York Road Little Driffield East Yorkshire YO25 5XA 01377 253617
		DATE 06/05/2005	CHECKED GS	
DRAWN RF		APPROVED PP		
DRAWING NUMBER LSTC/STD/PAR/731		REV 1		
PROJECT NEW TRIDENT DESIGN				