
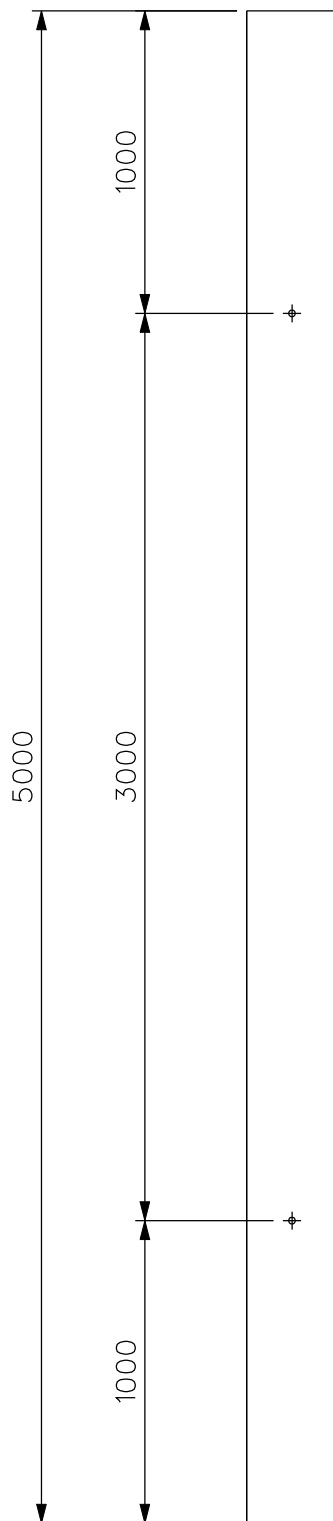


H POLE
FOUNDATION TIMBER BAULK
300x150x5000
(net weight 192.5kg)

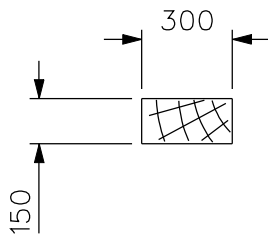

DESCRIPTION		FOR ISSUE				
REV	DATE	BY	MA	CHKD	SP	APPD
2	23/07/07					PP

GENERAL NOTES:

1. ALL DIMENSIONS IN MILLIMETERS (mm)
2. ALL HOLES 22mm DIAMETER
(unless noted)
3. MEMBER TO BE CLEARLY MARKED WITH
PREFIX 'TE' AND ITEM NUMBER FOR
SITE IDENTIFICATION

BAR MARK / ITEM NUMBER
TE738

CLIENT PowerSystems	TITLE PART - H POLE FOUNDATION TIMBER BAULK	SCALE 1 : 25 (UNLESS OTHERWISE STATED)	ORIGINAL SIZE A4	LS TRANSMISSION CONSULTANCY LIMITED Yorkshire House York Road Little Driffield East Yorkshire YO25 5XA 01377 253617 
		DATE 09/05/2005	CHECKED GS	
SPECIFICATION OHL-03-132		DRAWN RF	APPROVED PP	
		DRAWING NUMBER LSTC/STD/PAR/738	REV 2	