


DESCRIPTION		FOR ISSUE			
REV	DATE	BY	CHKD	APPD	
1	29/08/07	JR	GS	PP	

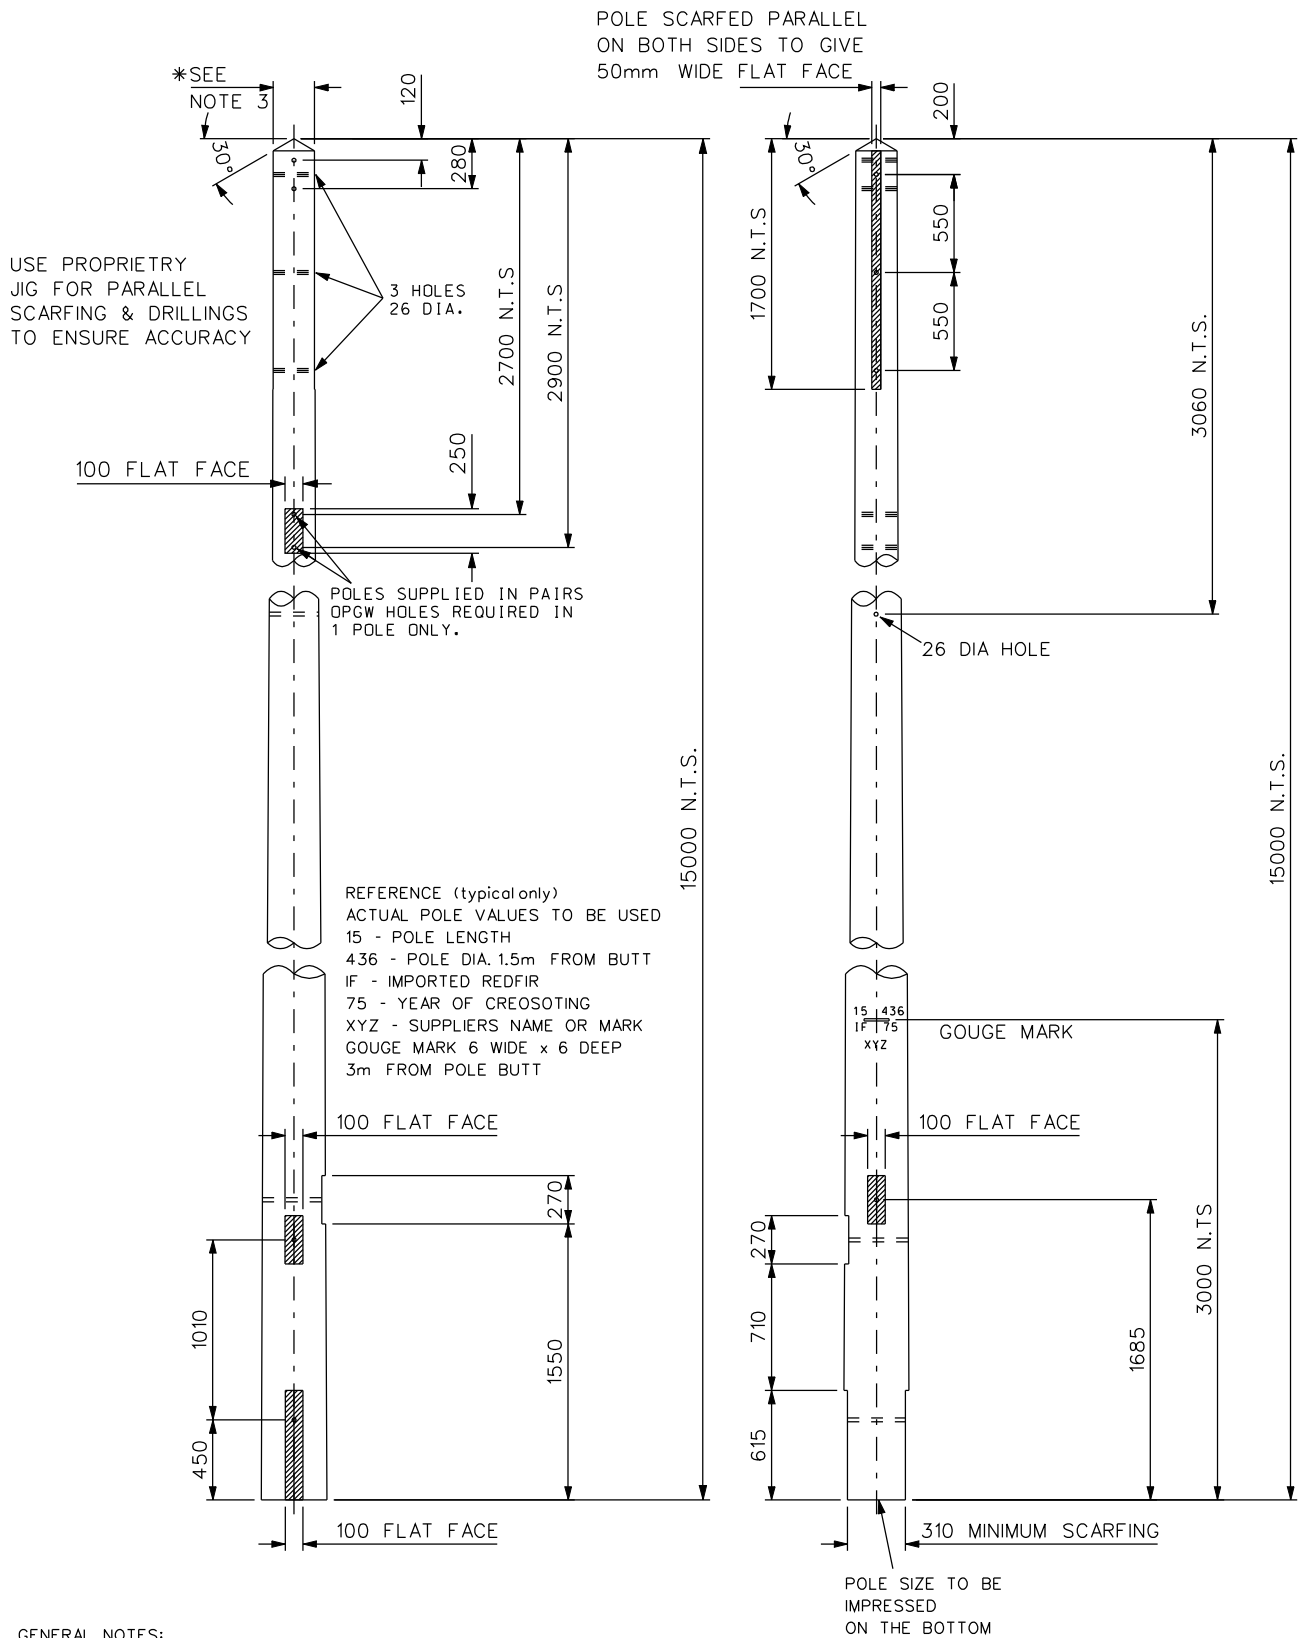

GENERAL NOTES:

- ALL DIMENSIONS ARE IN mm, UNLESS NOTED
- ALL DRILLINGS TO BE 24mm DIAMETER HOLES - UNO
- POLE SIZES BASED ON BS1990, EXTRA STOUT POLES RANGE
 LENGTH = 15m
 * MINIMUM TOP DIST BETWEEN FLATS = 233mm
 * MAXIMUM TOP DIST BETWEEN FLATS = 265mm
 MINIMUM DIAMETER 1.5m FROM BUTT = 436mm

SUPPLIER TO NOTE THESE DIMENSIONS ARE FOR GENERIC POLE DRILLING AND SCARFING ONLY TO SUIT A RANGE OF POLE SIZES, ACTUAL POLE MINIMUM DIMENSIONS TO BE SPECIFIED AT TIME OF ORDERING. ORDER VALUES WILL SUPERSEDE THESE STATED VALUES. MAXIMUM VALUE NOT TO BE EXCEEDED

BAR MARK / ITEM NUMBER
TE846

CLIENT PowerSystems	TITLE MG53 SCARFING DETAILS	SCALE 1:30 (UNLESS OTHERWISE STATED)	ORIGINAL SIZE A3	 LSTC North Yorkshire House York Road Little Driffield East Yorkshire YO25 5XA Tel 01377 253617 Fax 01377 259555 LSTC South Bourne House Office 21 475 Godstone Road Whyteleafe Surrey CR3 0BL Tel 01883 621114	
		DATE 29/08/07	CHECKED GS		
PROJECT OHL-03-132		DRAWN JR	APPROVED PP		
		DRAWING NUMBER LSTC/STD/PAR/846			REV 1