


POLE SCARFED PARALLEL ON BOTH
SIDES TO GIVE 50mm WIDE FLAT FACE

DESCRIPTION		FOR ISSUE			
REV	DATE	BY	CHKD	APPD	JKS
1	20/12/07	JR	SP		

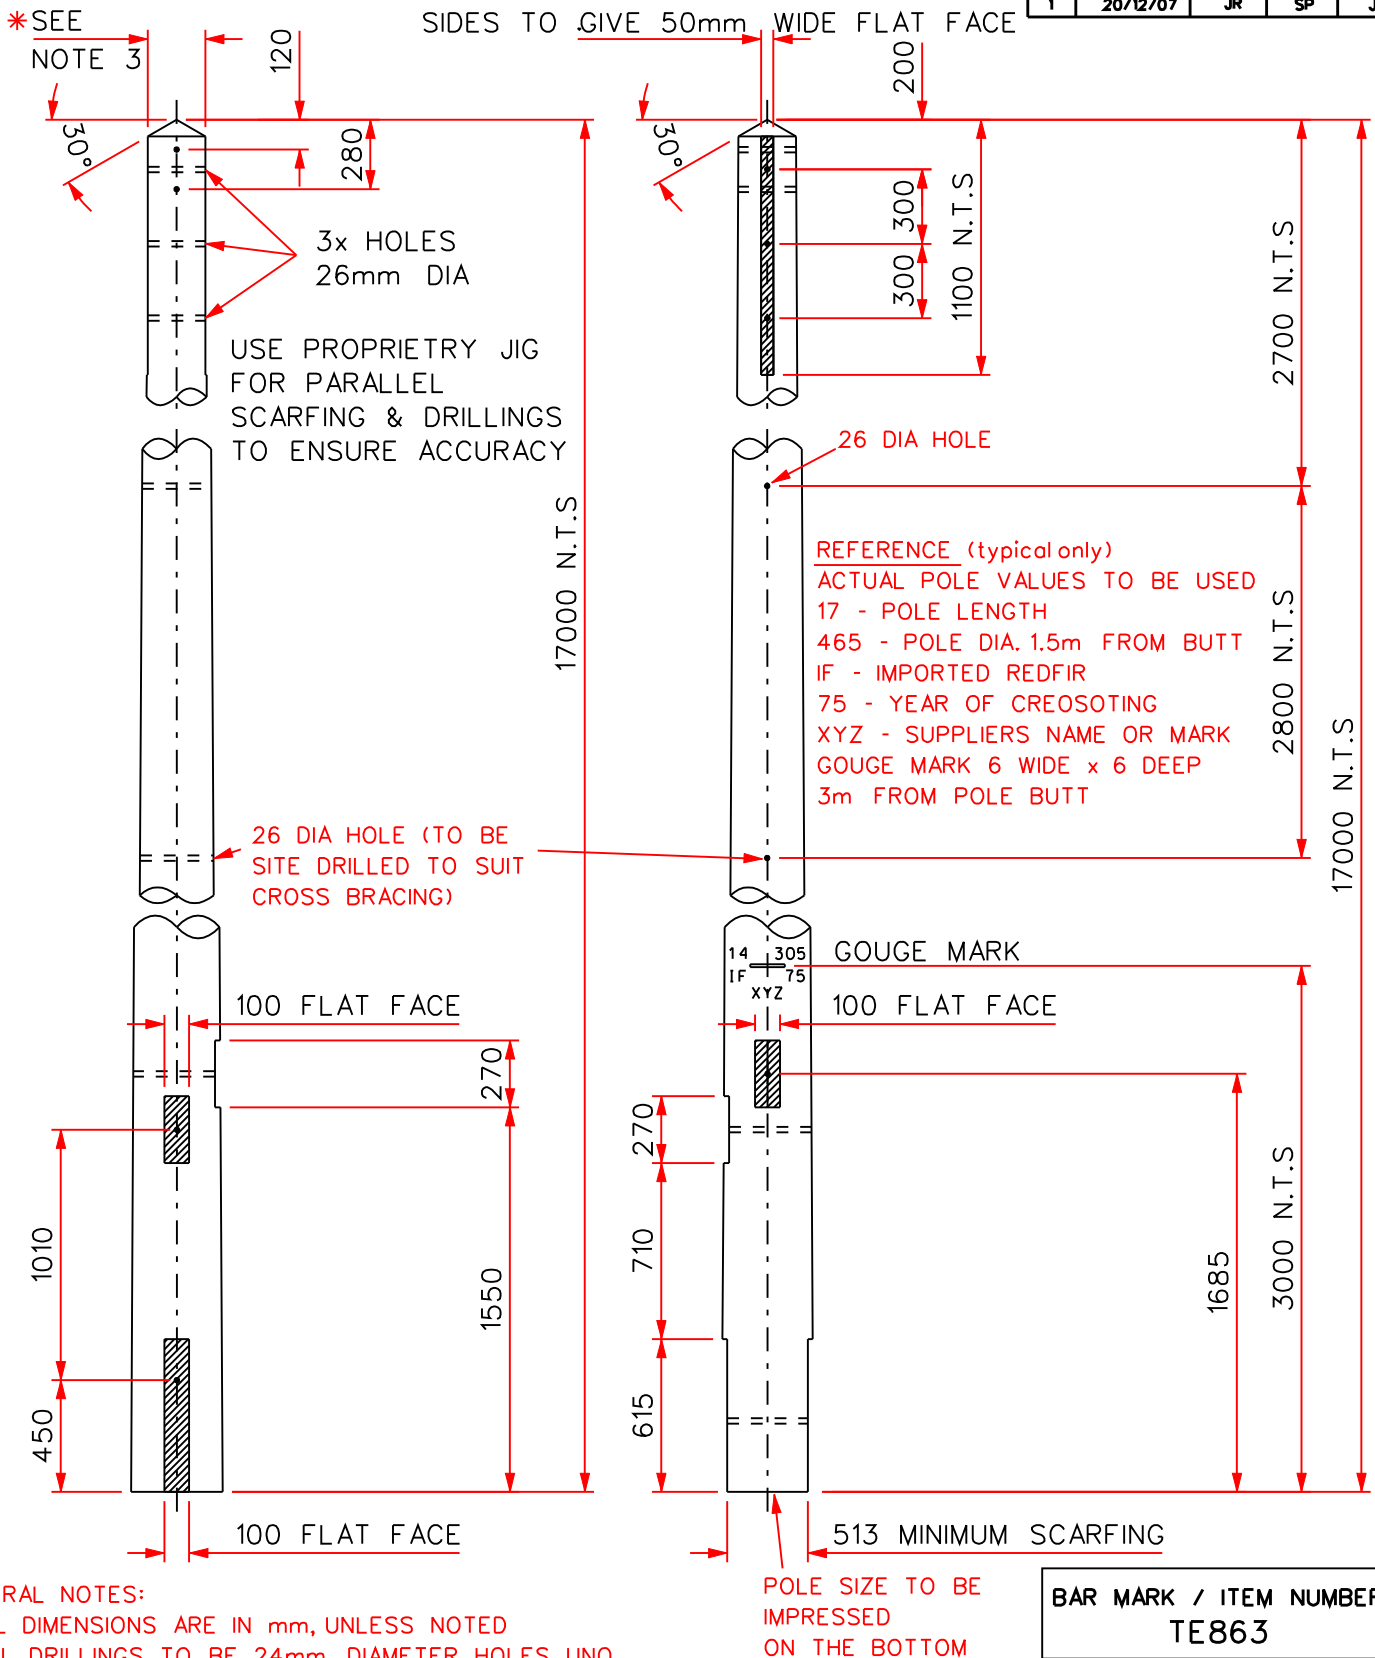

GENERAL NOTES:

1. ALL DIMENSIONS ARE IN mm, UNLESS NOTED
2. ALL DRILLINGS TO BE 24mm DIAMETER HOLES UNO.
3. POLE SIZES BASED ON BS1990, EXTRA EXTRA STOUT POLES RANGE

LENGTH = 17m & PARALLEL WITHIN LIMITS

*MINIMUM TOP DIST BETWEEN FLATS = 260mm

*MAXIMUM TOP DIST BETWEEN FLATS = 270mm

MINIMUM DIAMETER 1.5m FROM BUTT = 500mm

BAR MARK / ITEM NUMBER
TE863

SUPPLIER TO NOTE THESE DIMENSIONS ARE FOR GENERIC POLE DRILLING AND SCARFING ONLY TO SUIT A RANGE OF POLE SIZES, ACTUAL POLE MINIMUM DIMENSIONS TO BE SPECIFIED AT TIME OF ORDERING. ORDER VALUES WILL SUPERSEDE THESE STATED VALUES. MAXIMUM VALUE NOT TO BE EXCEEDED.

CLIENT	TITLE MG32 SCARFING DETAILS	SCALE 1 : 30 (UNLESS OTHERWISE STATED)	ORIGINAL SIZE A4	LS TRANSMISSION CONSULTANCY LIMITED Yorkshire House York Road Little Driffield East Yorkshire YO25 5XA 01377 253617
PowerSystems		DATE 20/12/07	CHECKED SP	
SPECIFICATION		DRAWN JR	APPROVED JKS	
		DRAWING NUMBER LSTC/STD/PAR/863		
OHL-03-132				