


DESCRIPTION		FOR ISSUE			
REV	DATE	BY	CHKD	APPD	PP
1	05/09/07	JR	GS		

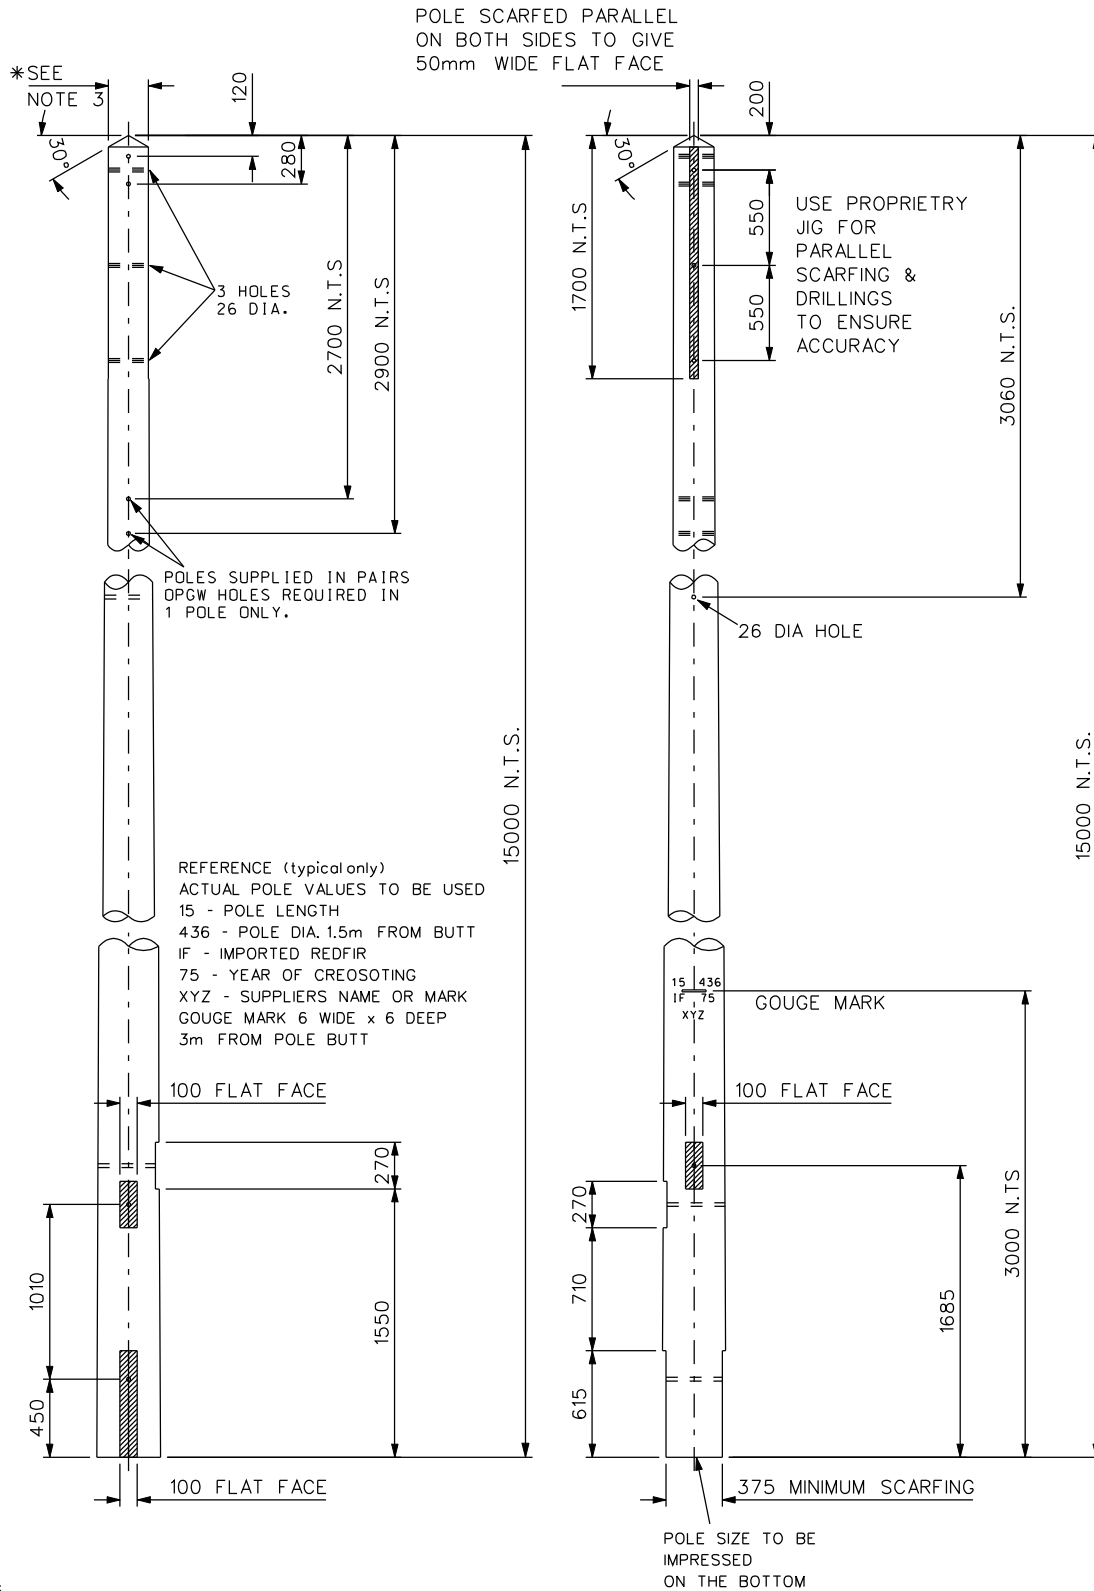

GENERAL NOTES:

- ALL DIMENSIONS ARE IN mm, UNLESS NOTED
- ALL DRILLINGS TO BE 22mm DIAMETER HOLES - UNO
- POLE SIZES BASED ON BS1990, EXTRA STOUT POLES RANGE
 LENGTH = 15m
 * MINIMUM TOP DIST BETWEEN FLATS = 233mm
 * MAXIMUM TOP DIST BETWEEN FLATS = 265mm
 MINIMUM DIAMETER 1.5m FROM BUTT = 436mm

SUPPLIER TO NOTE THESE DIMENSIONS ARE FOR GENERIC POLE DRILLING AND SCARFING ONLY TO SUIT A RANGE OF POLE SIZES, ACTUAL POLE MINIMUM AND MAXIMUM DIMENSIONS TO BE SPECIFIED AT TIME OF ORDERING. ORDER VALUES WILL SUPERSEDE THESE STATED VALUES.

BAR MARK / ITEM NUMBER
TE850

CLIENT PowerSystems	TITLE MG13 SCARFING DETAILS	SCALE 1:30 (UNLESS OTHERWISE STATED)	ORIGINAL SIZE A3
		DATE 05/09/07	CHECKED GS
PROJECT OHL-03-132		DRAWN JR	APPROVED PP
		DRAWING NUMBER LSTC/STD/PAR/850	REV 1



LSTC North
Yorkshire House
York Road
Little Driffield
East Yorkshire
YO25 5XA
Tel 01377 253617
Fax 01377 259555

LSTC South
Bourne House
Office 21
475 Godstone Road
Whyteleafe
Surrey
CR3 0BL
Tel 01883 621114