
DESCRIPTION				
DRAFT ISSUE				
REV B	DATE 22/07/04	BY JN	CHKD GS	APPD PP
DESCRIPTION				
DRAFT ISSUE - REDESIGN OF FOUNDATIONS				
REV C	DATE 29/07/04	BY JN	CHKD GS	APPD PP

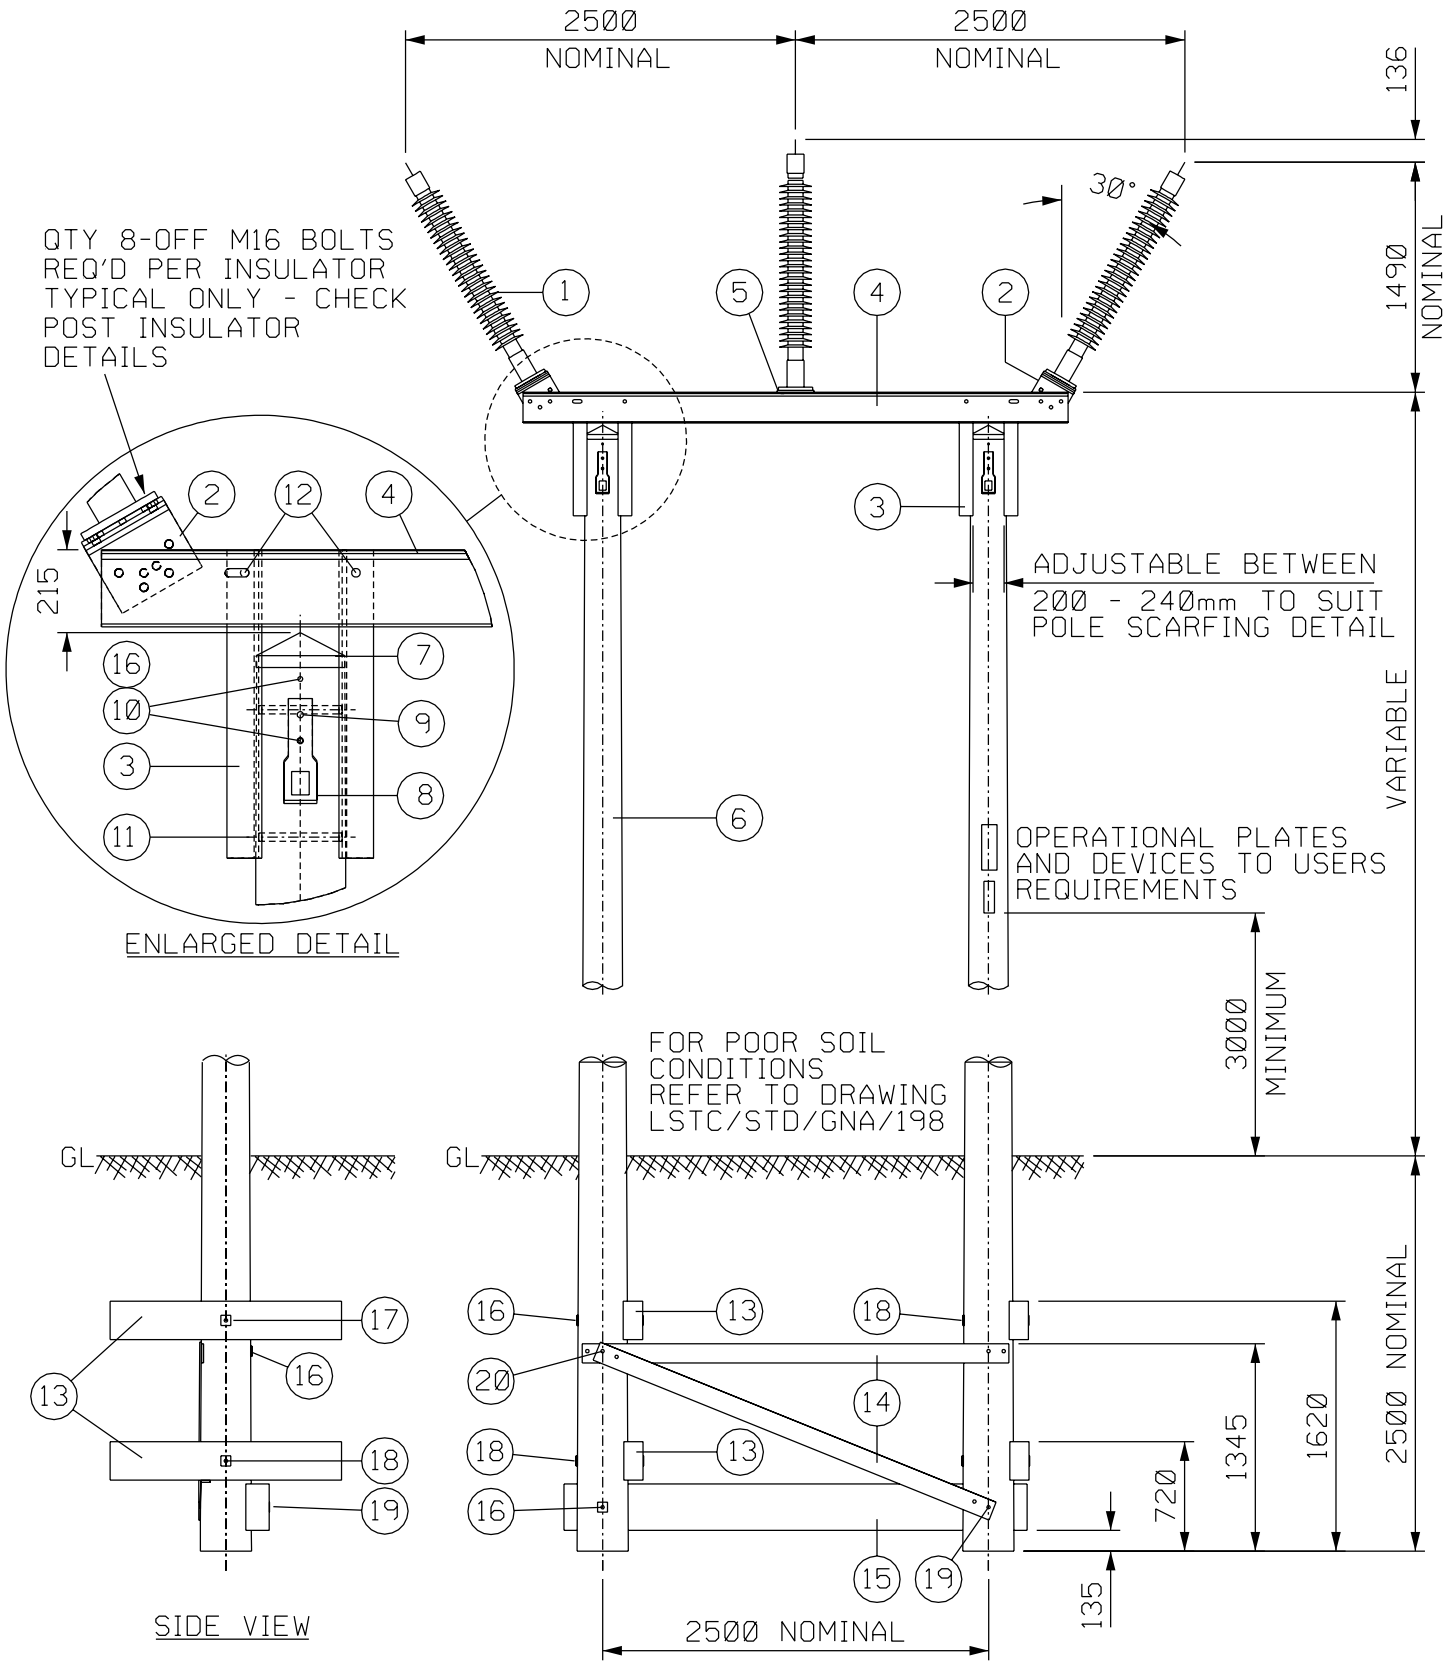

GENERAL NOTES:

1. ALL STEELWORK TO BE PROTOTYPE CHECK ERECTED BEFORE MASS PRODUCTION.
2. SAFETY SIGNS INSTALLED TO SSE POWER DISTRIBUTION PROCEDURE PR-PS-325
3. DETAILS OF POSITIONS AND MOUNTING HEIGHTS FOR SIGNS AND PLATES TO SSE POWER DISTRIBUTION DRG HO/39/4400 & 4401.
4. FOR MATERIAL LIST SEE LSTC/STD/GNA/02

CLIENT: SSE POWER DISTRIBUTION	TITLE: TRIDENT 2 POLE INTERMEDIATE STRUCTURE	SCALE: 1:50 (UNLESS OTHERWISE STATED)	ORIGINAL SIZE: A4
PROJECT: 132kV SINGLE CIRCUIT UNEARTHED OVERHEAD LINE		DATE: 14/04/04	CHECKED: GS
		DRAWN: JN	APPROVED: PP
		DRAWING NUMBER: LSTC/STD/GNA/01	REV: C

LS TRANSMISSION CONSULTANCY LIMITED
PADDOCK HOUSE
10 MIDDLE STREET SOUTH
DRIFFIELD
EAST YORKSHIRE YO25 6PT
TEL: 01377 240047