


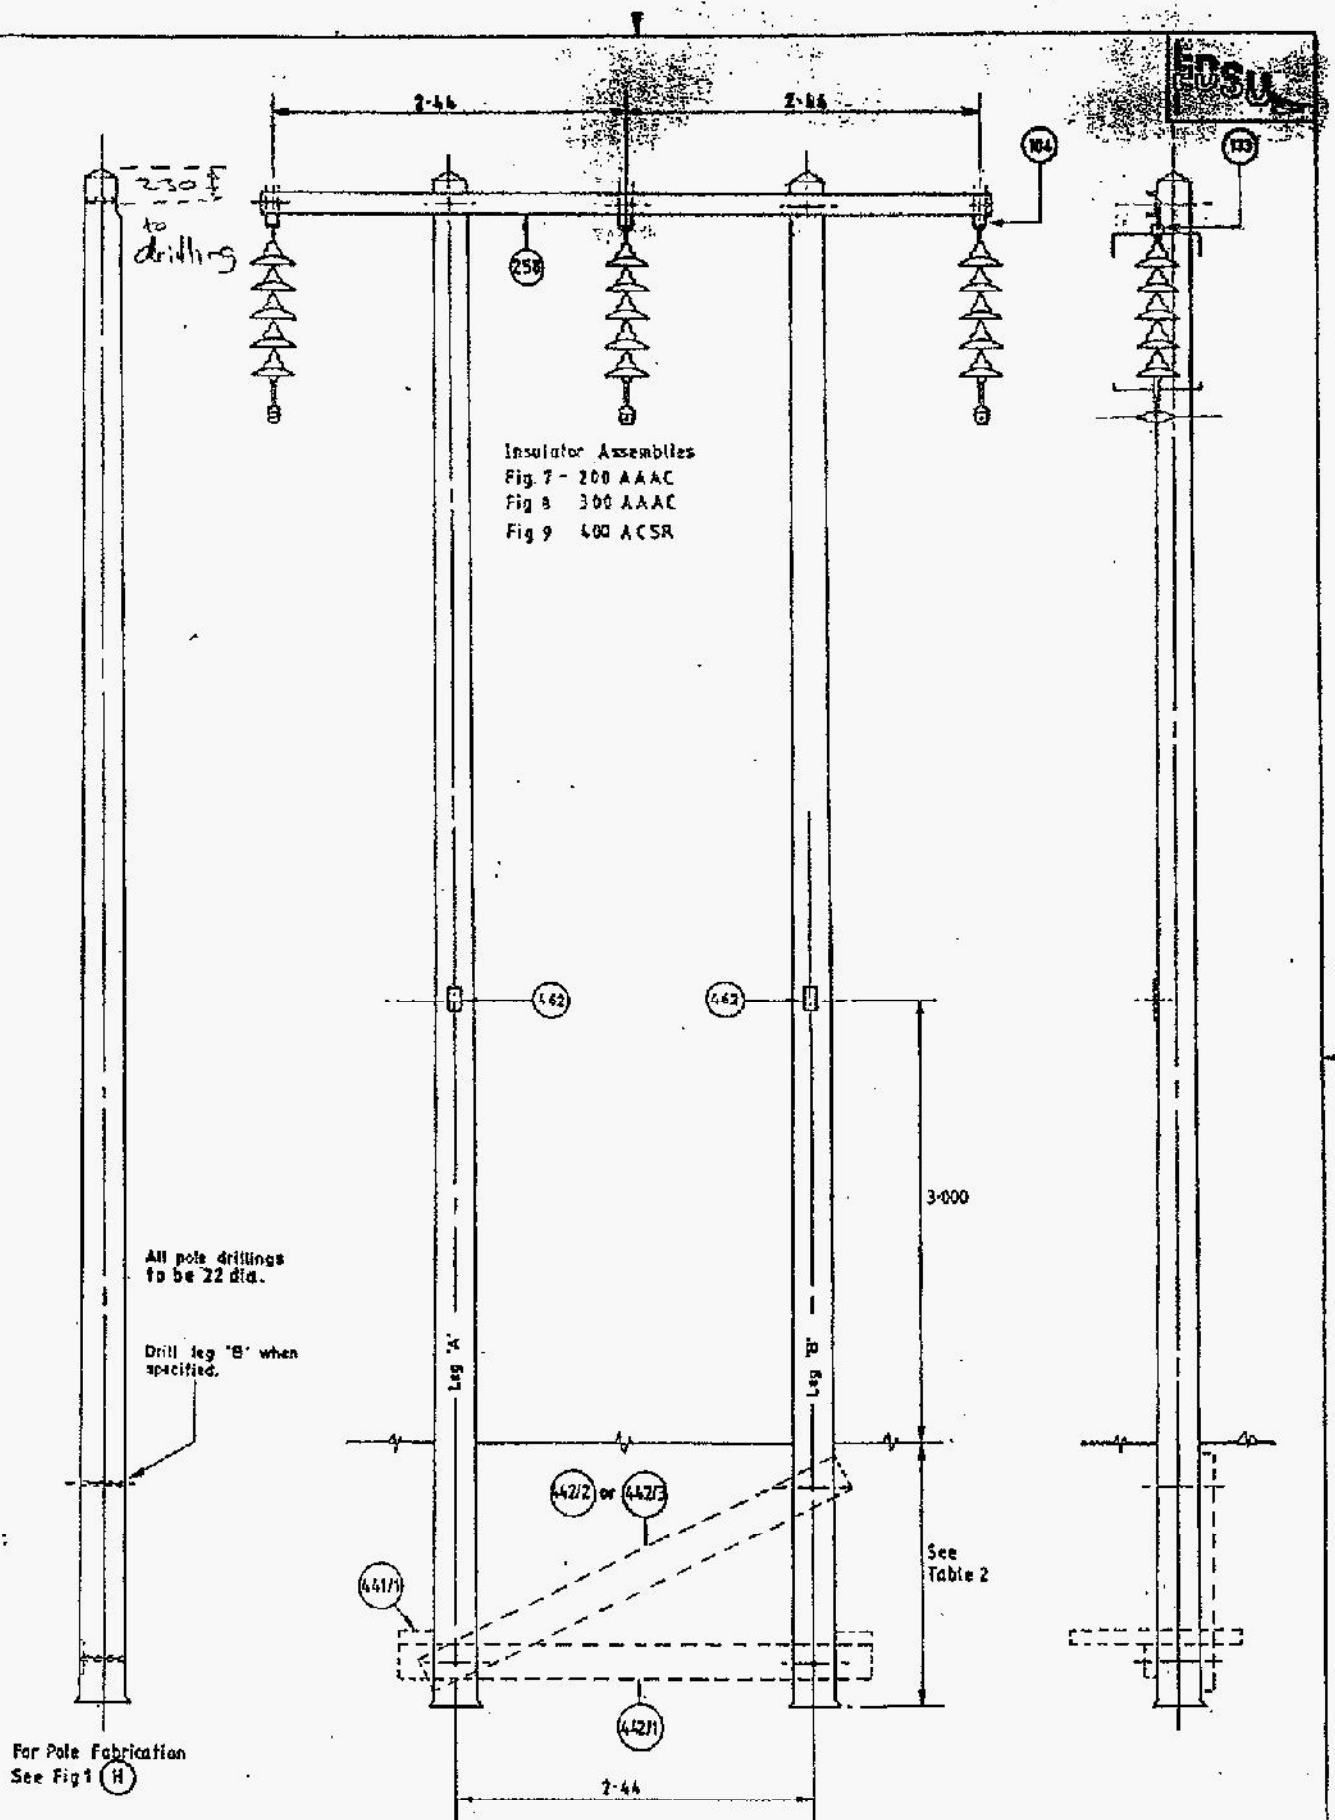

AS DRG HP 14/1

66kV CONSTRUCTION
H SUSPENSION ST. LINE & THROUGH
ANGLES UP TO 3°

SCALE	
DATE	27.5.92
DRAWN	W. B.
TRACED	P. G.
CHECKED	
APPROVED	

MEB
Midlands Electricity plc

FIG. 2.

MATERIAL SCHEDULE FIG 2 (REV 14/1)

ITEM	MEN	QUANTITY
Pole (size to be specified - see table 2)	3453—	2
Crossarm 200 AAAC Conductors	3451000	)
300 AAAC Conductors)		1
400 AAAC Conductors)	3452580	)
'U' link	3451041	3
Ball Ended Eye Link 70KN MFL	3451330	3
Disc Insulator Porcelain 70KN MFL	3450851	)
Glass 70KN MFL	3450852	) 15
Socket Tongue 70KN MFL	3450880	3
Suspension Clamp 300 AAAC Conductor	3454931	)
300 AAAC Conductor	3454932	) 3
400 ACSR Conductor	3454933	)
Arc Horn Live End	3450891	3
Dead End	3450892	3
Safety Sign Divs 3, 5 and 8	3454621	)
Divs 1, 4 and 7	3454622	) 2
Foundation Blocks (if required)		
1.25m x 250 x 100	3454411	2
3.5m x 250 x 100	3454421	1
3.23m x 250 x 100 Poles up to 14m	3454422	)
3.38m x 250 x 100 Poles over 14m	3454423	) 1
Assembly Bolts M20 x 45	3453661	6
Pole Bolt - Crossarm - M20 x 260	3453633	2
Foundation Bolts (if required)		
M20 x 450	3453636	)
M20 x 530	3453637	)
M20 x 610	3453638	) 5
M20 x 760	3453639	)
Square Flat Washer - M20 x 65	3453170	2-12*
* With Foundation Blocks		