


RENO	REVISION NOTE	DATE	SIGNATURE	CHECKED

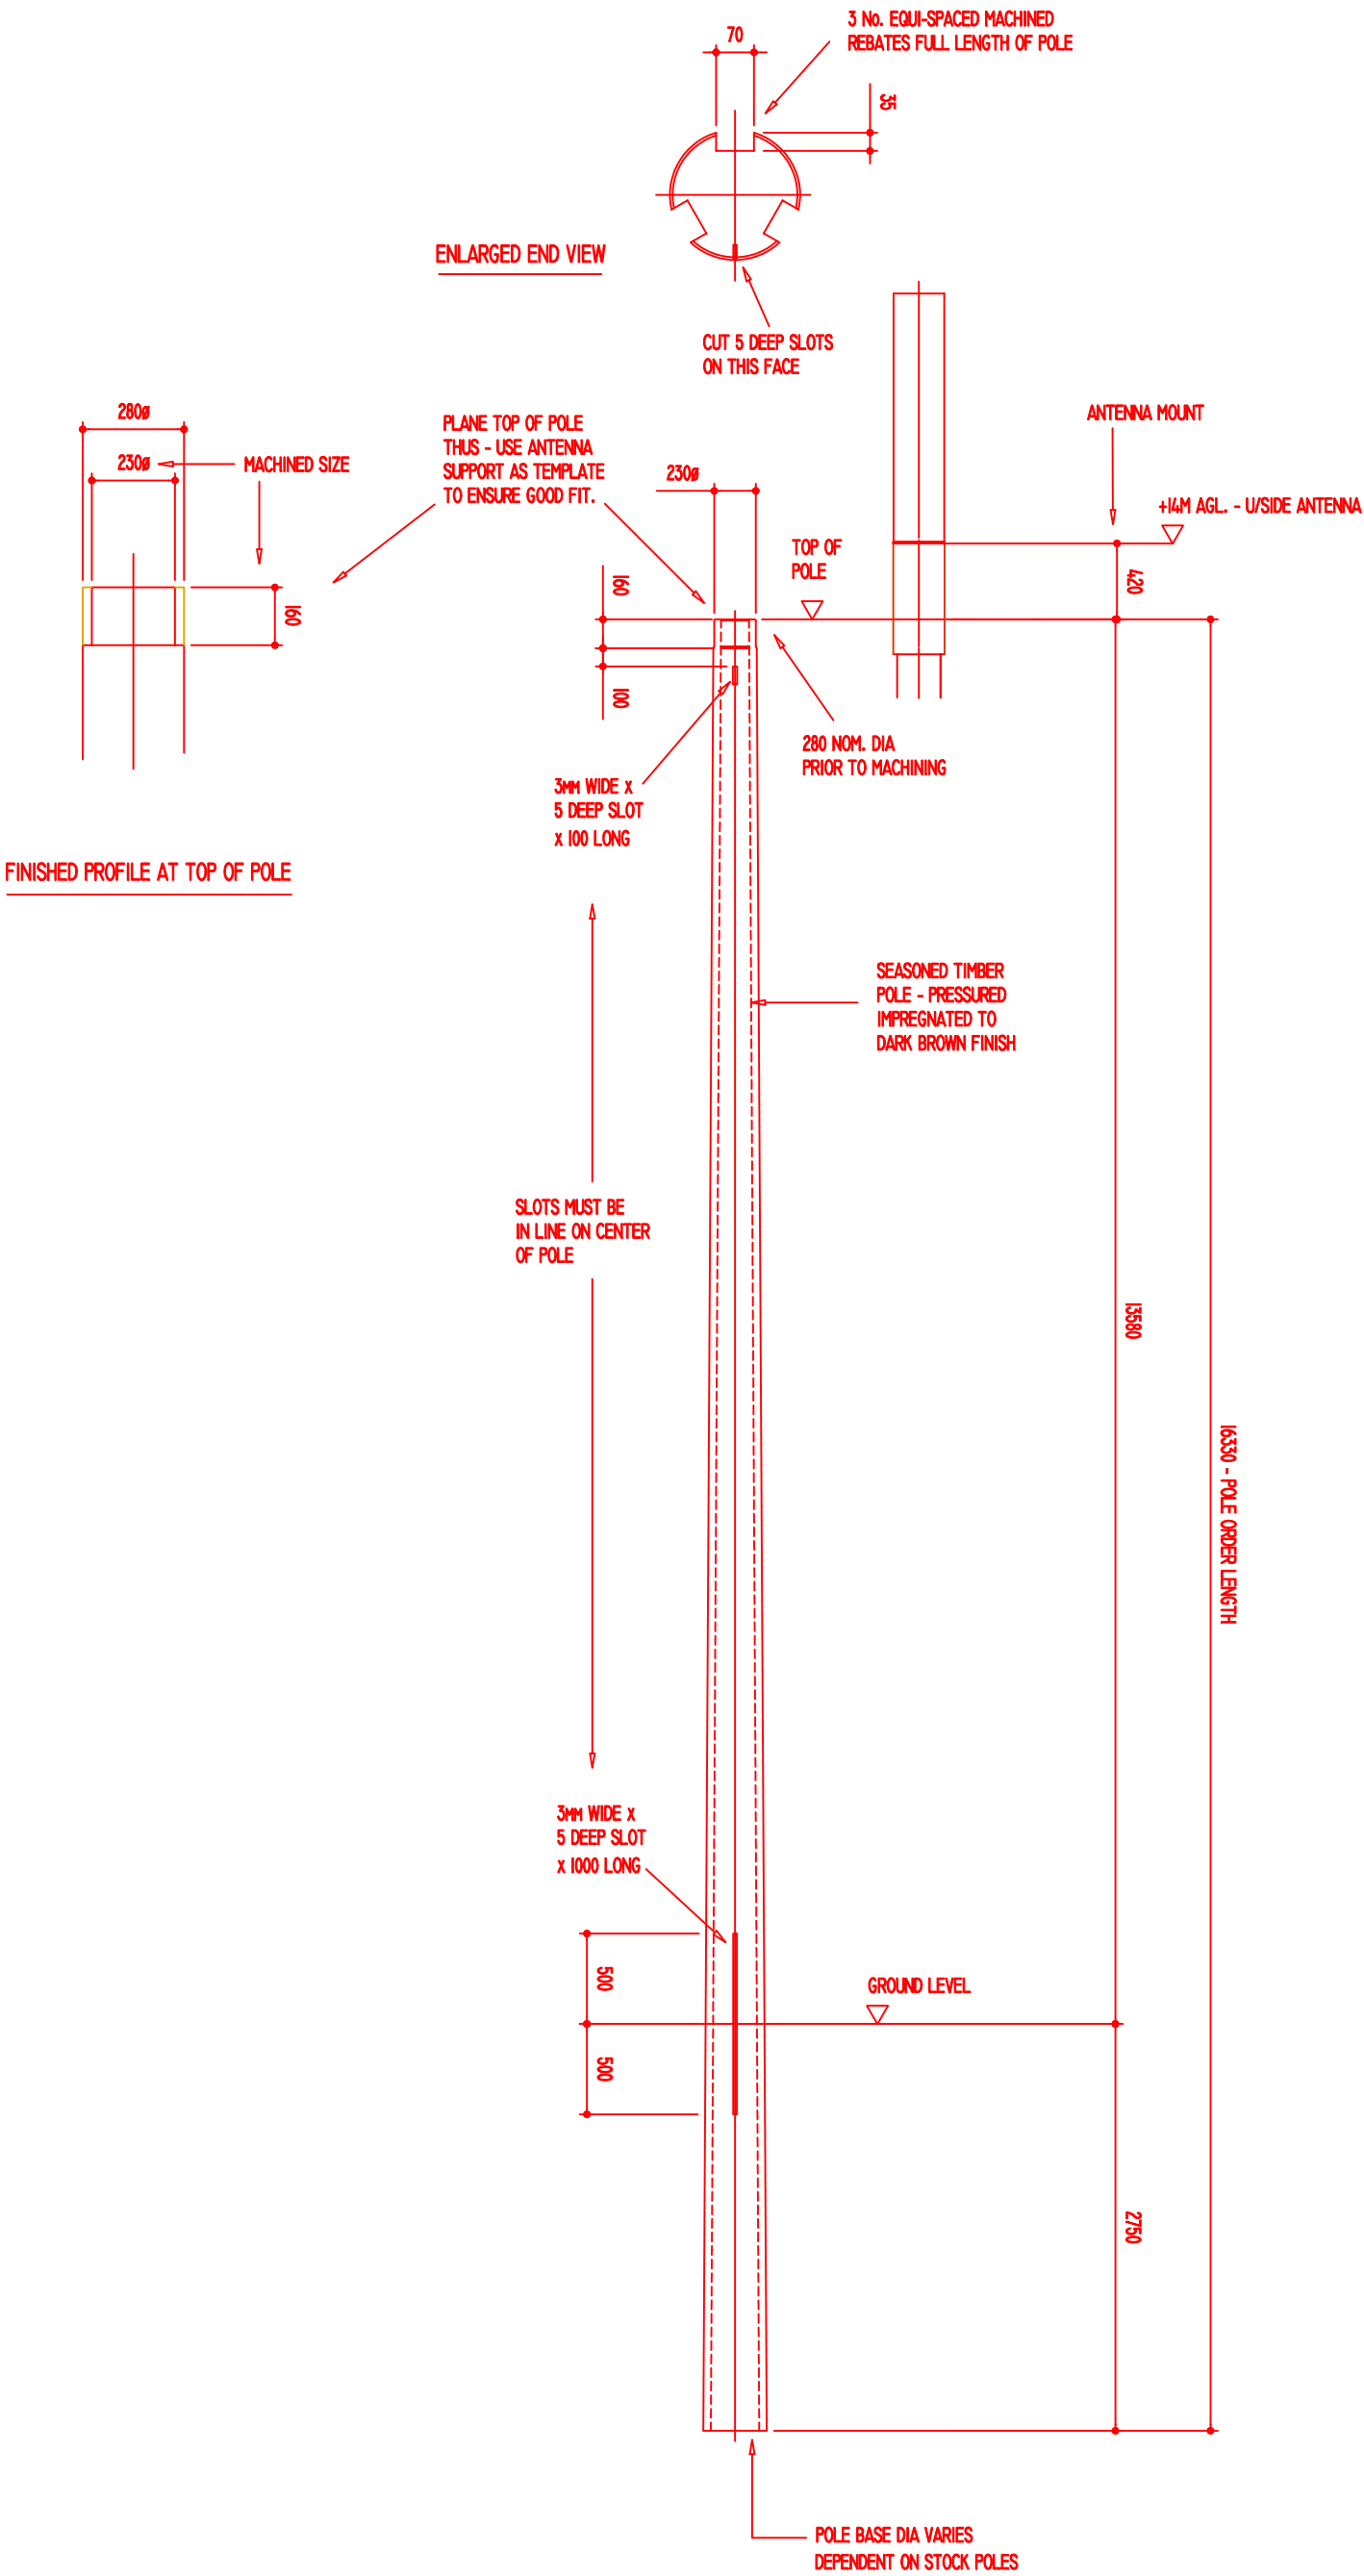

TITLE/NAME, DESIGNATION, MATERIAL, DIMENSION ETC				ARTICLE NO./REFERENCE	
ITEM/REF	QUANTITY	CHECKED BY	APPROVED BY - DATE	FILENAME	DATE
DRAWN BY MC		GH	RV.10025.01	10.11.06	
MASTS TOWERS & ANTENNAS LTD. THE OLD POWER STATION, THE SLADE, TONBRIDGE, KENT. TN9 1HR TEL. 01732 770813 FAX. 01732 368067				CS. 10025 NAUNTON PARK - CHELTENHAM MACHINING DETAILS OF 14M TIMBER POLE	
TITLE				MTA/RV/10025/01	
ORIGINAL DRG. SIZE				REV. A	

2006 COPYRIGHT MTA LTD

A3