


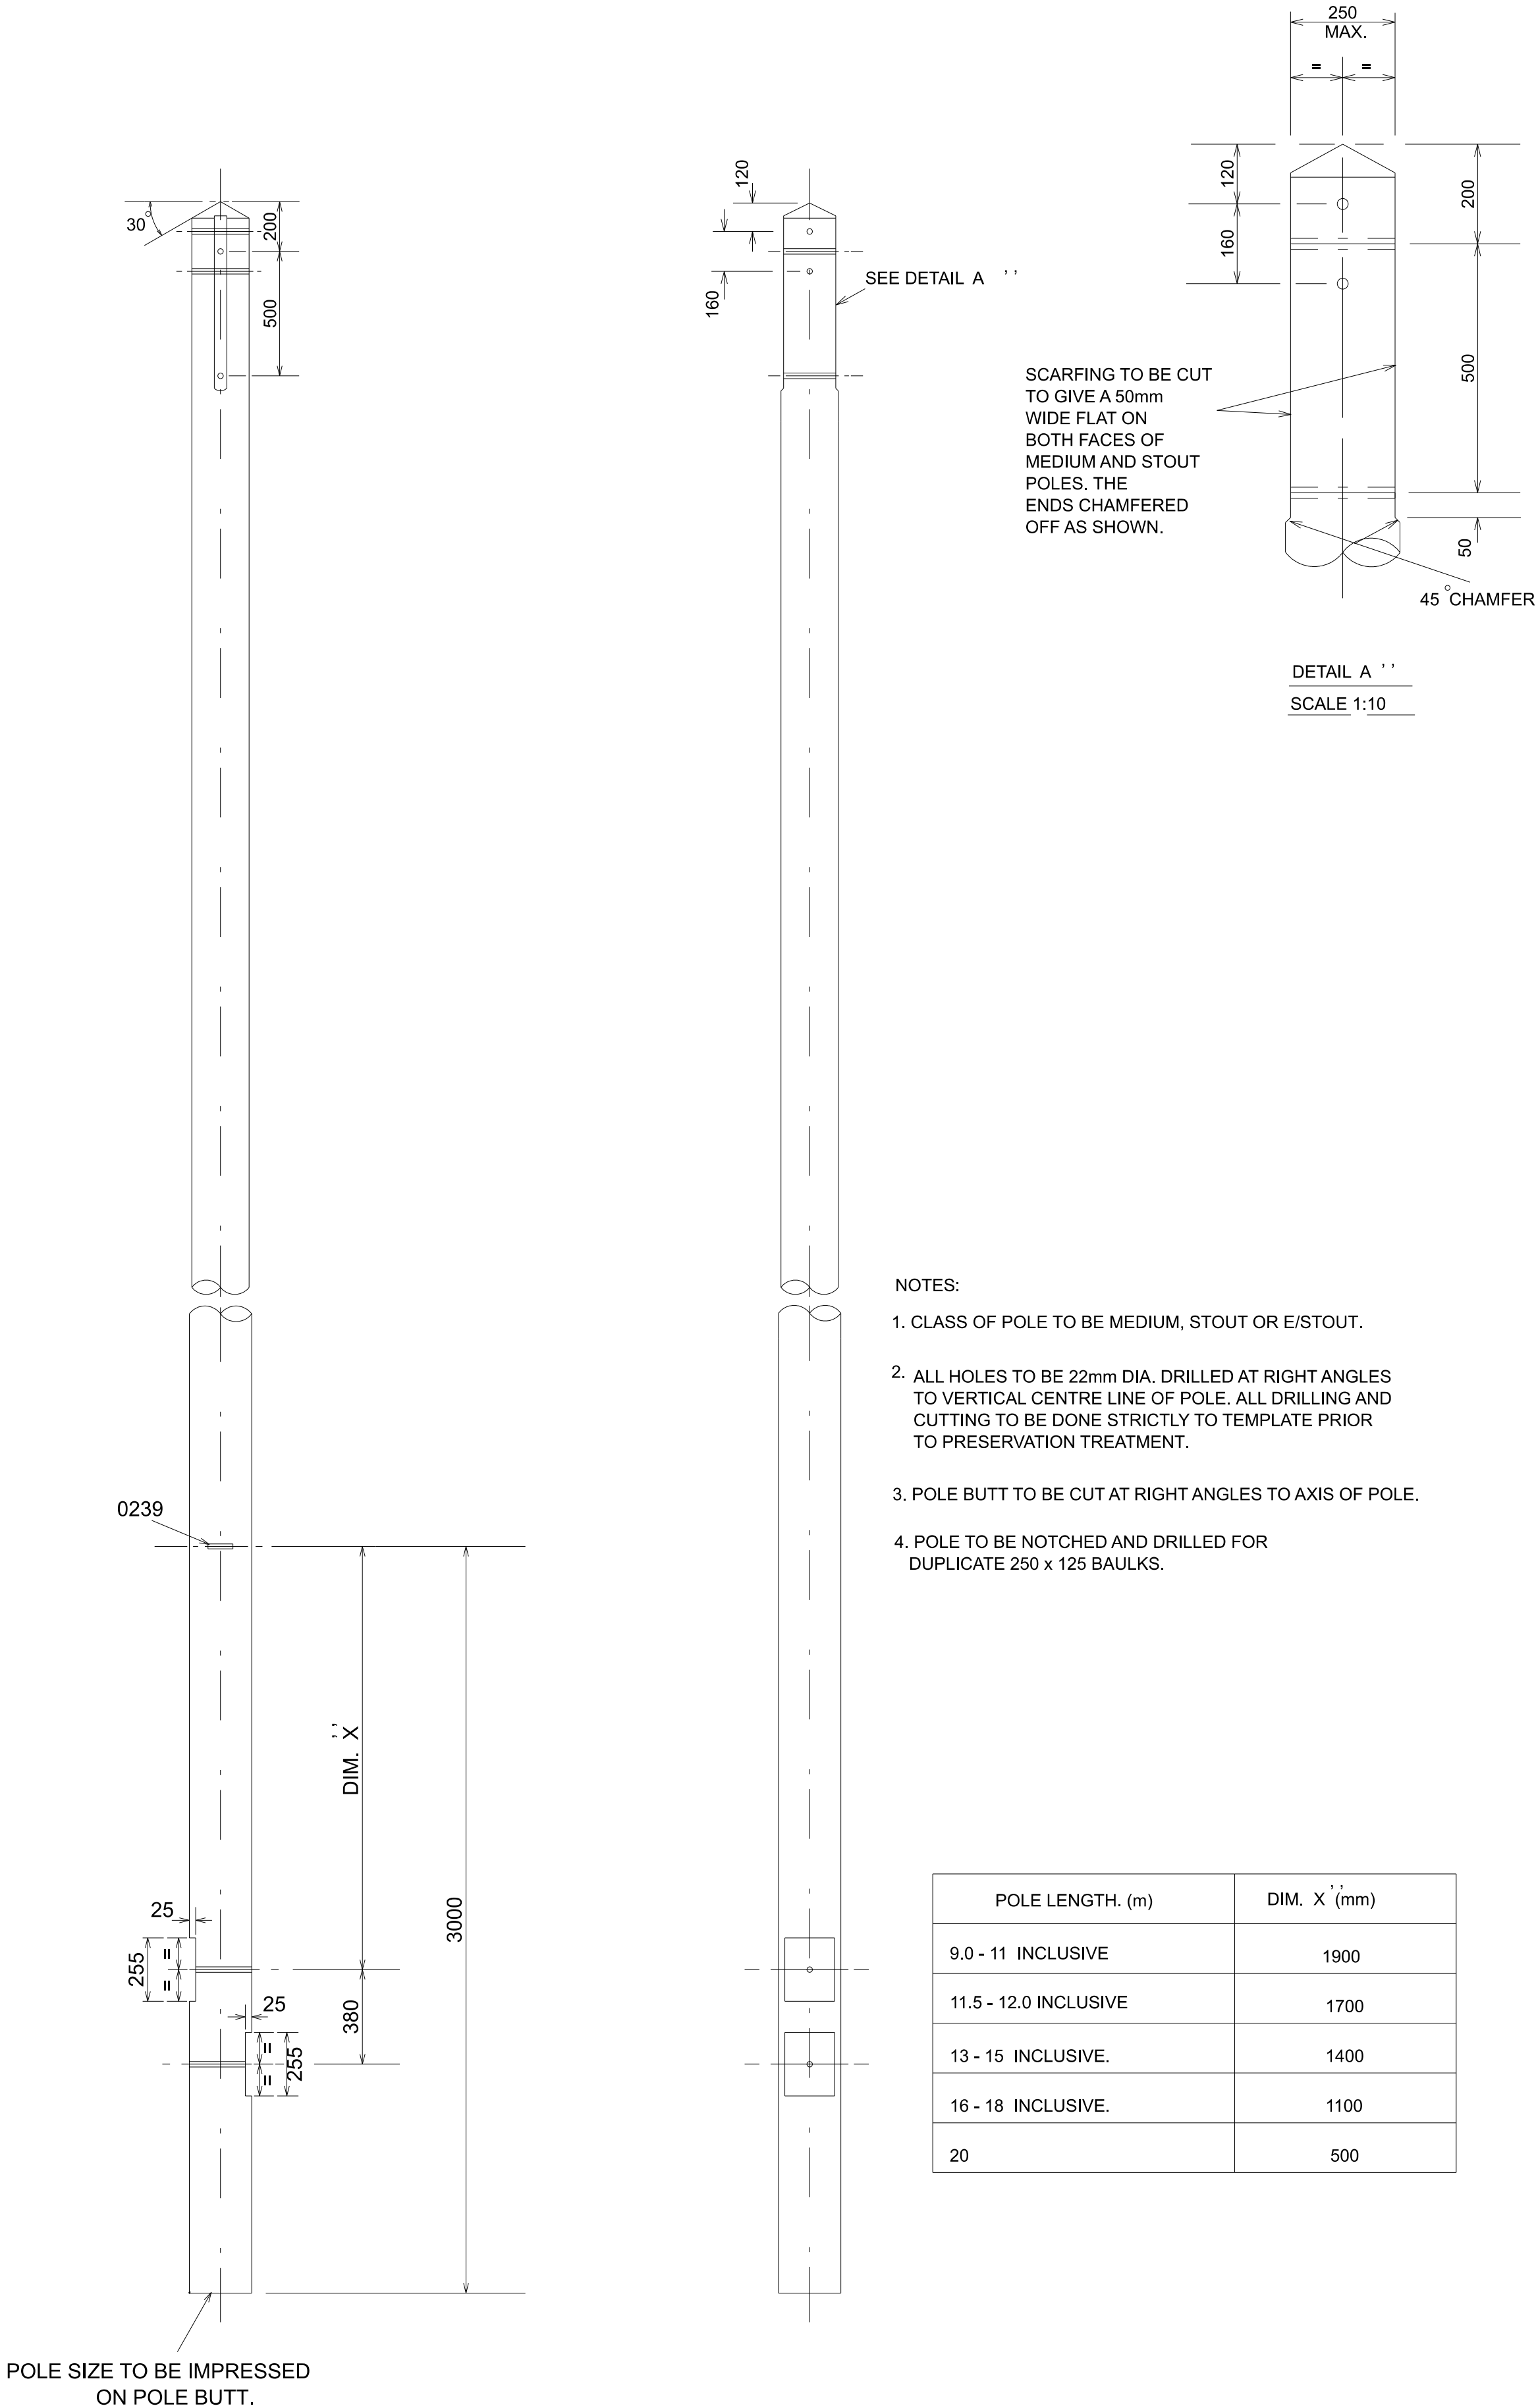

 NORTHERN POWERGRID		Lloyds Court, 78 Grey Street, Newcastle Upon Tyne, NE1 6AF		
Manufacturer Details		HV OVERHEAD LINES SINGLE POLE FABRICATION FOR ARRANGEMENTS TO ESI 43-40		
Sheet No. 1	Scale 1:20	Type PLANNING SYSTEM		
Prepared By W7Brian.James	Grid Reference	Ref No. C1004131	Historic Drg.No.	1000434001
Revised 31/03/26	Checked By G HAMMEL	Revision A Notes 11.5 INSERTED TO 12.0		
Date Issued 06/12/11				