

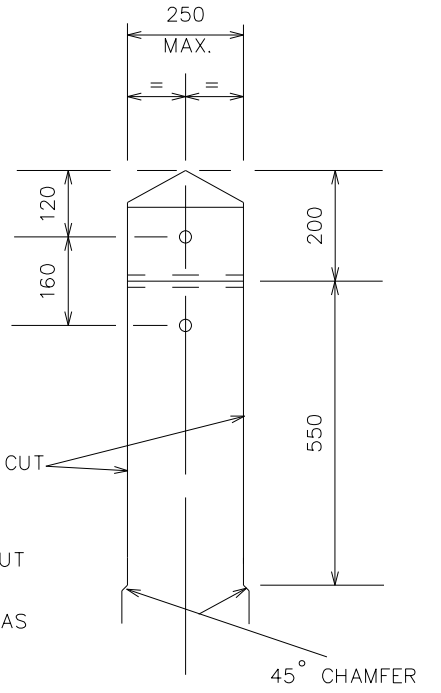
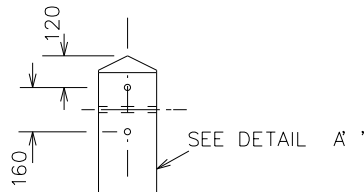
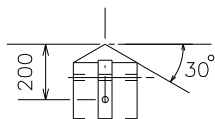
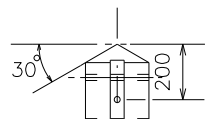


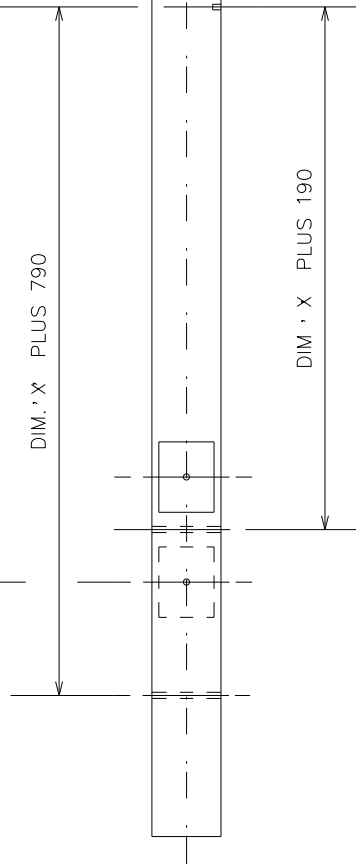

DETAIL A '
SCALE 1:10

NOTES:

1. CLASS OF POLE TO BE 'STOUT.'
2. 'STOUT' CLASS POLES TO HAVE MINIMUM DIA. OF 210mm AT TOP.
3. POLES TO BE MATCHED.
4. ALL HOLES TO BE 22mm DIA. DRILLED AT RIGHT ANGLES TO VERTICAL CENTRE LINE OF POLE. ALL DRILLING AND CUTTING TO BE DONE STRICTLY TO TEMPLATE PRIOR TO PRESERVATION TREATMENT.
5. POLE BUTT TO BE CUT AT RIGHT ANGLES TO AXIS OF POLE.
6. POLE TO BE NOTCHED AND DRILLED FOR DUPLICATE 250 x 125 BAULKS.

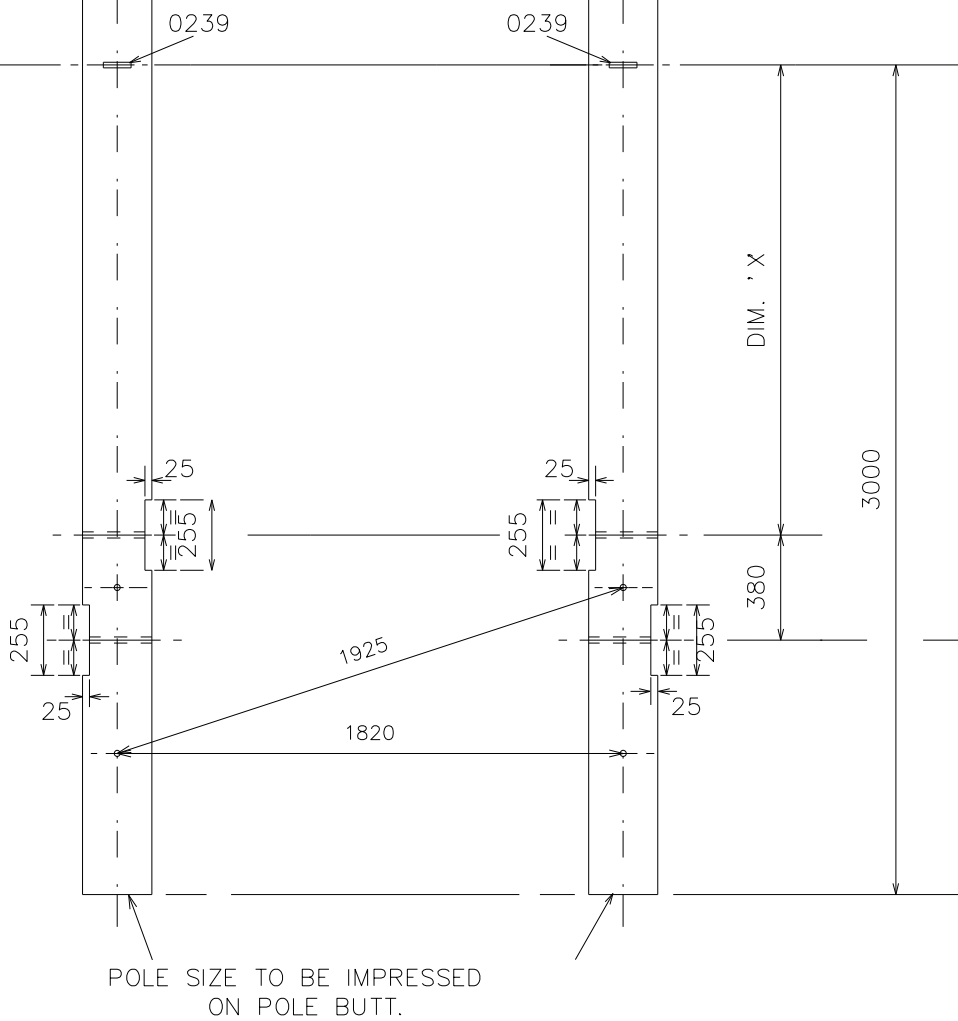

POLE LENGTH. (m)	DIM. 'X' (mm)
9.0 - 11 INCLUSIVE.	1900
11.5 - 12.0 INCLUSIVE	1700
13 - 15 INCLUSIVE.	1400
16 - 18 INCLUSIVE.	1100
20	500

 NORTHERN POWERGRID	Lloyds Court, 78 Grey Street, Newcastle Upon Tyne, NE1 6AF		
	H.V OVERHEAD LINES 'H' POLE FABRICATION		
	Manufacturer Details		
	Sheet No. 1	Scale 1:20 & 10	
Prepared By J L WEBB	Type		
Revised 01.10.2001	Grid Reference	Ref No. C319351	Historic Drg.No. 1.00.043.4002
Date Issued 01/12/1987	Checked By G. HAMMEL	Revision 'E' Notes - 11.5 INSERTED TO 12.0	