


Document reference	NSP/004/042				
Version:-	1.0	Date of Issue:-	Jan 07	Page	46 of 113

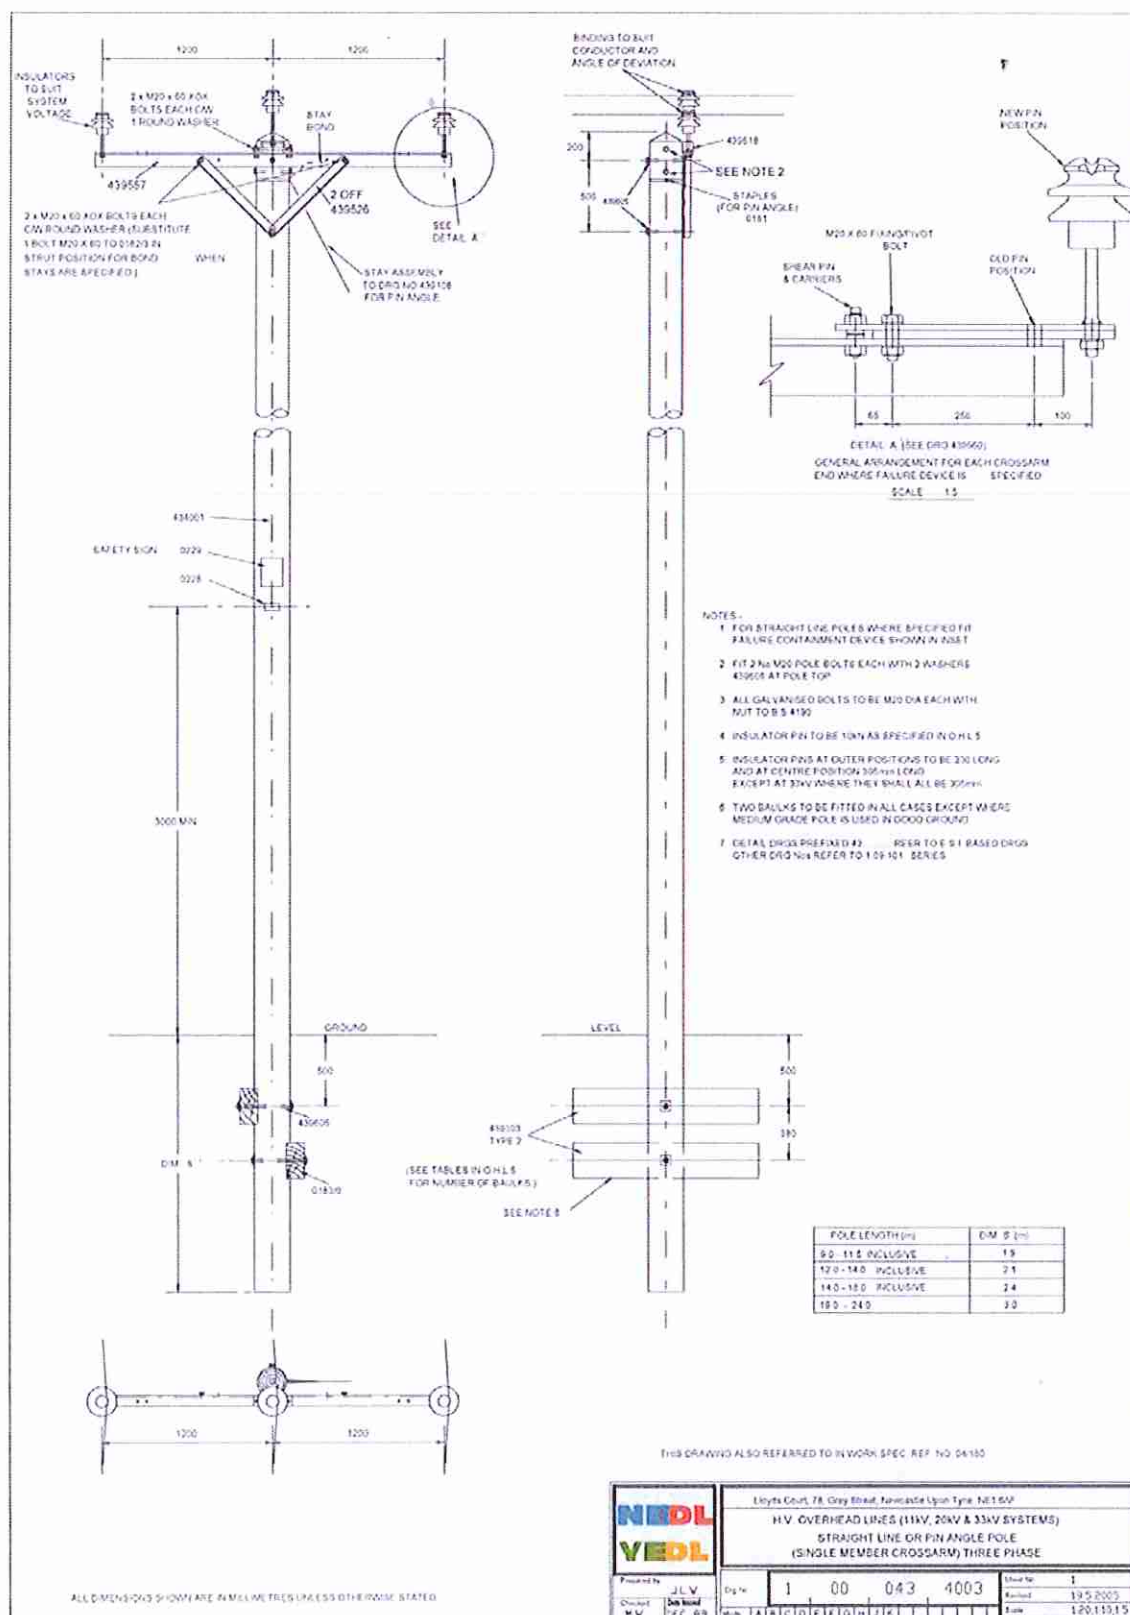

ALL DIMENSIONS SHOWN ARE IN MILLIMETRES UNLESS OTHERWISE STATED

THIS DRAWING ALSO REFERRED TO IN WORK SPEC REF NO 04100

NEDL VEDL		Lloyds Court, 78, Gray Street, Newcastle Upon Tyne, NE1 6AV H.V. OVERHEAD LINES (11kV, 20kV & 33kV SYSTEMS) STRAIGHT LINE OR PIN ANGLE POLE (SINGLE MEMBER CROSSARM) THREE PHASE	
Project No JLV Client M.V.	Date 06.09.07	Dwg No 1 00 043 4003	Issue No 1 Revised 19.5.2005 Date 12.01.15