
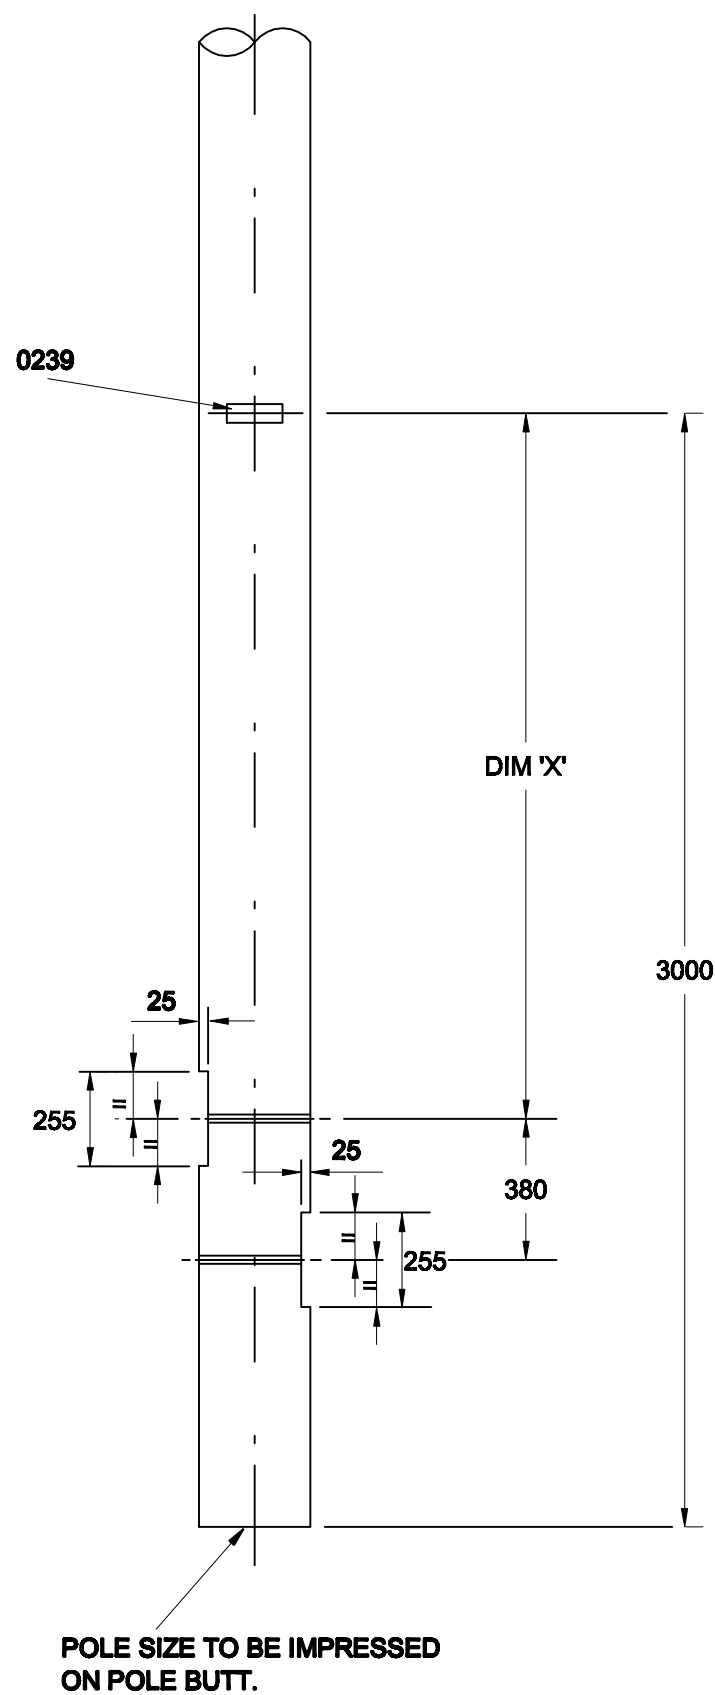
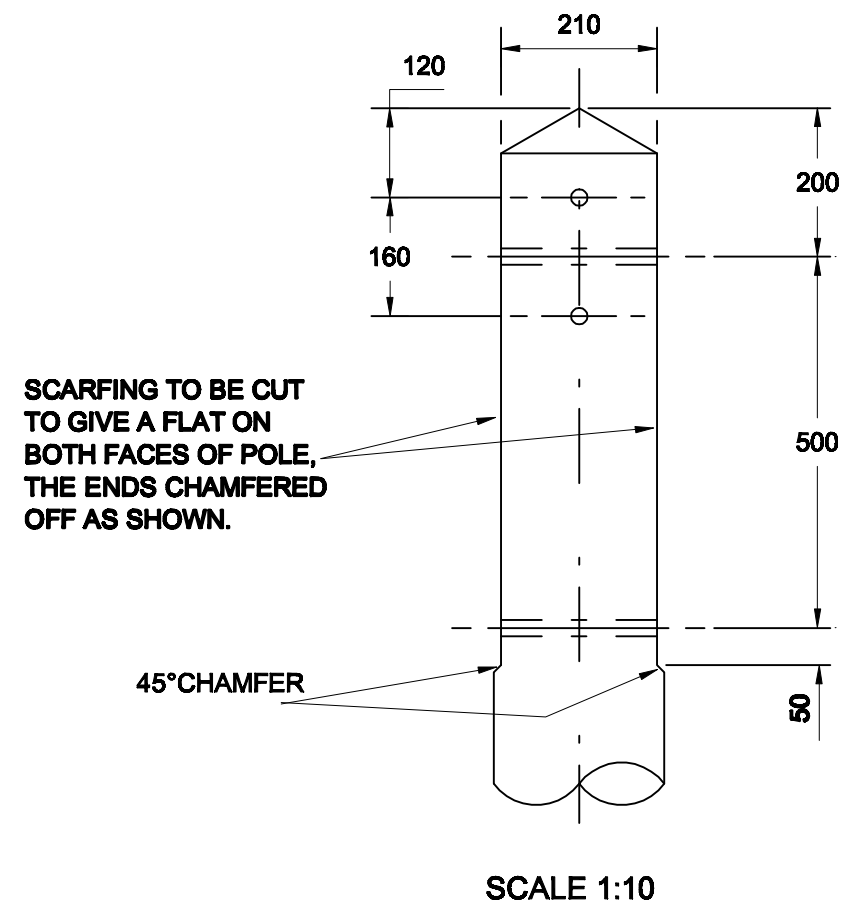
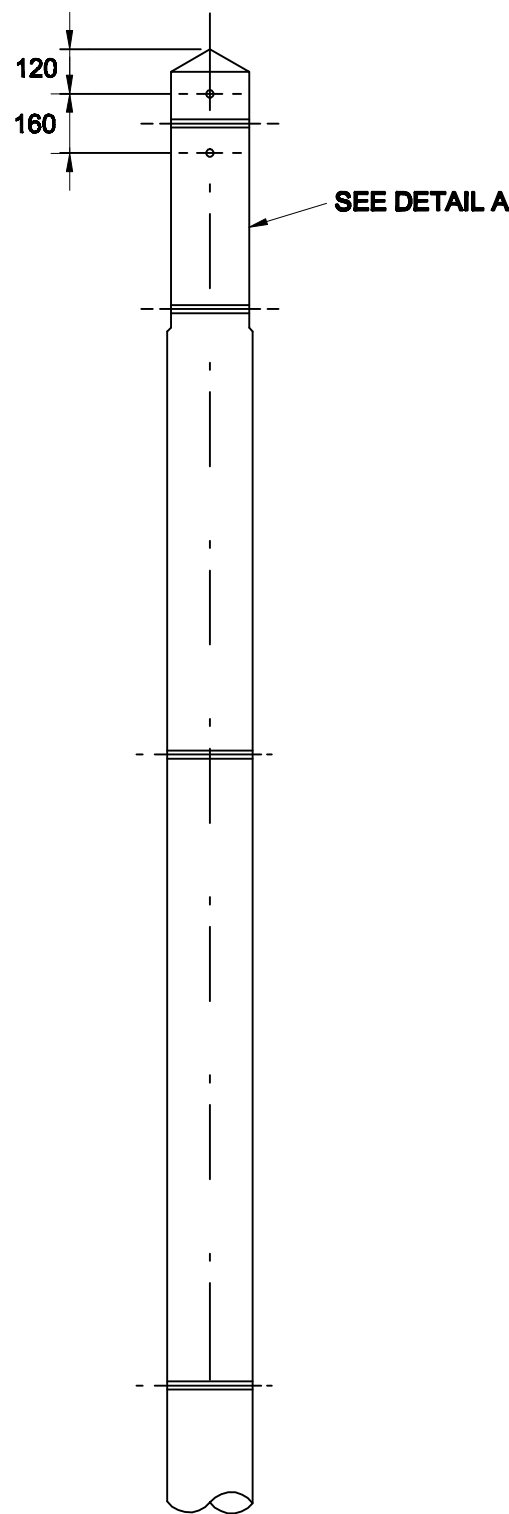


NOTES.

- 1.CLASS OF POLE TO BE STOUT,POLE TOP TO BE 210mm.AFTER FABRICATION.
- 2.ALL HOLES TO BE 22mm.DIA.DRILLED AT RIGHT ANGLES TO VERTICAL CENTRE LINE OF POLE. UNLESS SPECIFIED OTHERWISE. ALL DRILLING AND CUTTING TO BE DONE STRICTLY TO TEMPLATE PRIOR TO PRESERVATIVE TREATMENT.
- 3.POLE BUTT TO BE CUT AT RIGHT ANGLES TO AXIS OF POLE.
- 4.POLE TO BE NOTCHED AND DRILLED FOR DUPLICATE 250 x 125 BAULKES.

POLE LENGTH (m)	DIM X (mm)
9.0 - 11.0 INCLUSIVE	1900
11.5 - 12.0 INCLUSIVE	1700
13.0 - 15.0 INCLUSIVE	1400
16.0 - 18.0 INCLUSIVE	1100

ALL DIMENSIONS SHOWN ARE IN MILLIMETRES UNLESS OTHERWISE STATED.

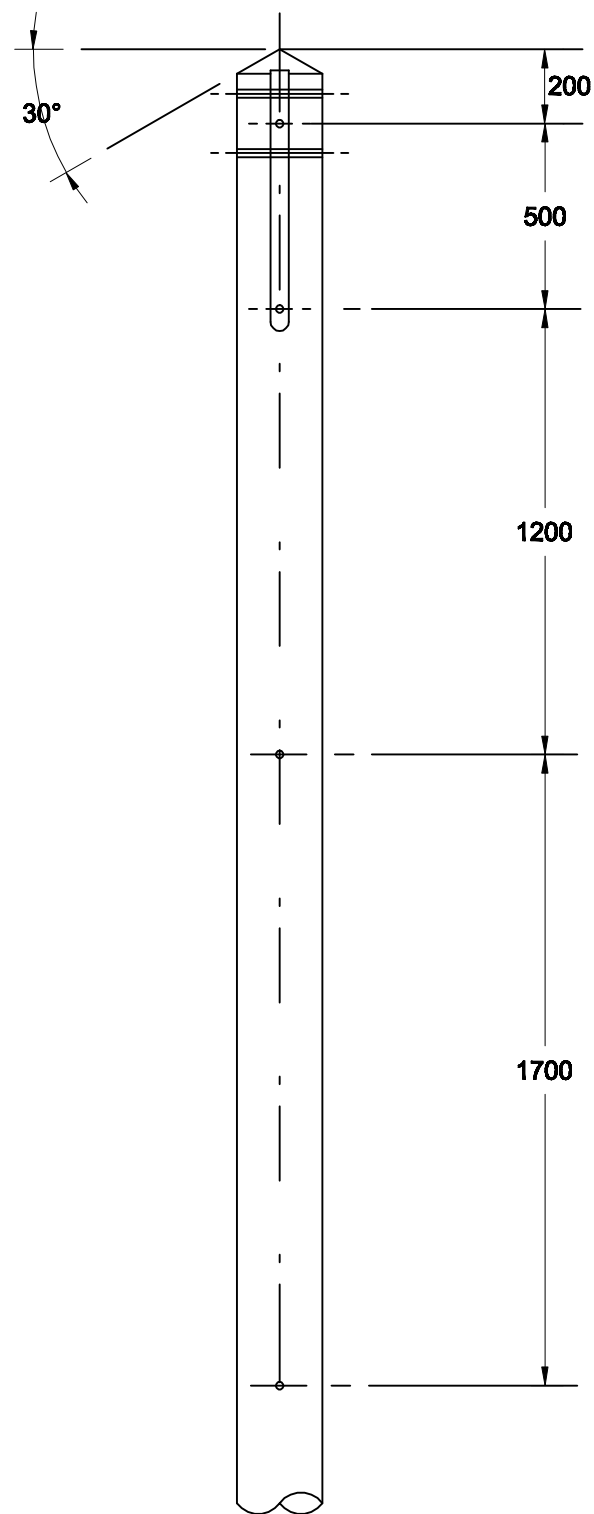

Manufacturer Details

Sheet No.
7

Scale
1:20

Prepared By
Barbara.Gordon

Revised
01/10/14

Date Issued
01/10/14

Grid Reference

Checked By
G HAMMEL

Lloyds Court, 78 Grey Street, Newcastle Upon Tyne, NE1 6AF

HV OVERHEAD LINES
FABRICATION FOR SINGLE POLE TERMINAL
DRG. NO. 1.00.043.4010 SHEET 6

Type

OVERHEAD

LINES

Ref No.

C1040649

Historic
Drg.No.

1000434010

Revision A

Notes