
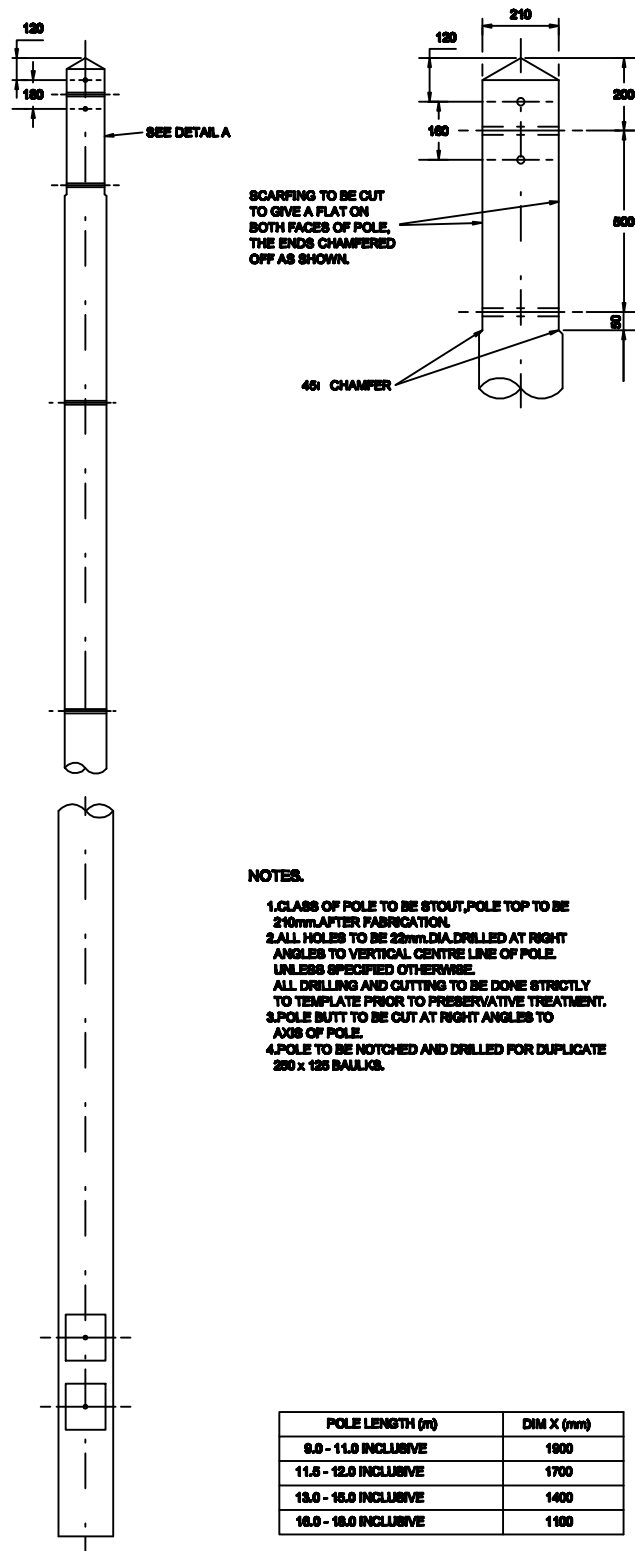


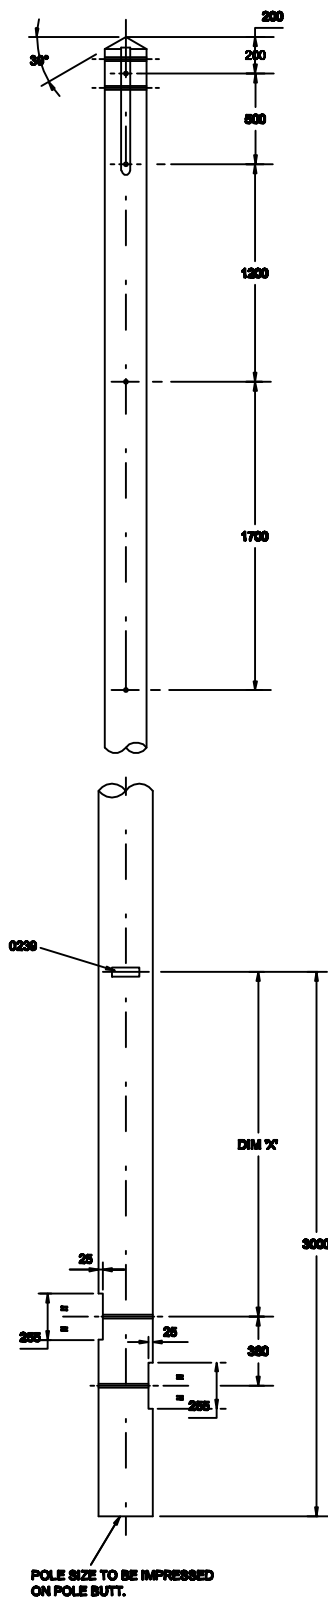

NOTES.

1. CLASS OF POLE TO BE STOUT, POLE TOP TO BE 210mm AFTER FABRICATION.
2. ALL HOLES TO BE 22mm DIA DRILLED AT RIGHT ANGLES TO VERTICAL CENTRE LINE OF POLE, UNLESS SPECIFIED OTHERWISE. ALL DRILLING AND CUTTING TO BE DONE STRICTLY TO TEMPLATE PRIOR TO PRESERVATIVE TREATMENT.
3. POLE BUTT TO BE CUT AT RIGHT ANGLES TO AXIS OF POLE.
4. POLE TO BE NOTCHED AND DRILLED FOR DUPLICATE 250 x 125 BALKS.

POLE LENGTH (m)	DIM X (mm)
9.0 - 11.0 INCLUSIVE	1800
11.5 - 12.0 INCLUSIVE	1700
13.0 - 15.0 INCLUSIVE	1400
16.0 - 18.0 INCLUSIVE	1100

ALL DIMENSIONS SHOWN ARE IN MILLIMETRES UNLESS OTHERWISE STATED.

		NEDL, Loyds Court, 78, Grey Street, Newcastle Upon Tyne, NE1 6AF	
		H.V. OVERHEAD LINES FABRICATION FOR SINGLE POLE TERMINAL DRG No 1.00.043.4010 SHEET 7	
Prepared by	J.L.W.	Dwg. No. 1 00 043 4010	Sheet No. 8
Checked	G.M.H.		Revised
Made Date		Made Date	Scale 1:20, 1:10 @ A2