
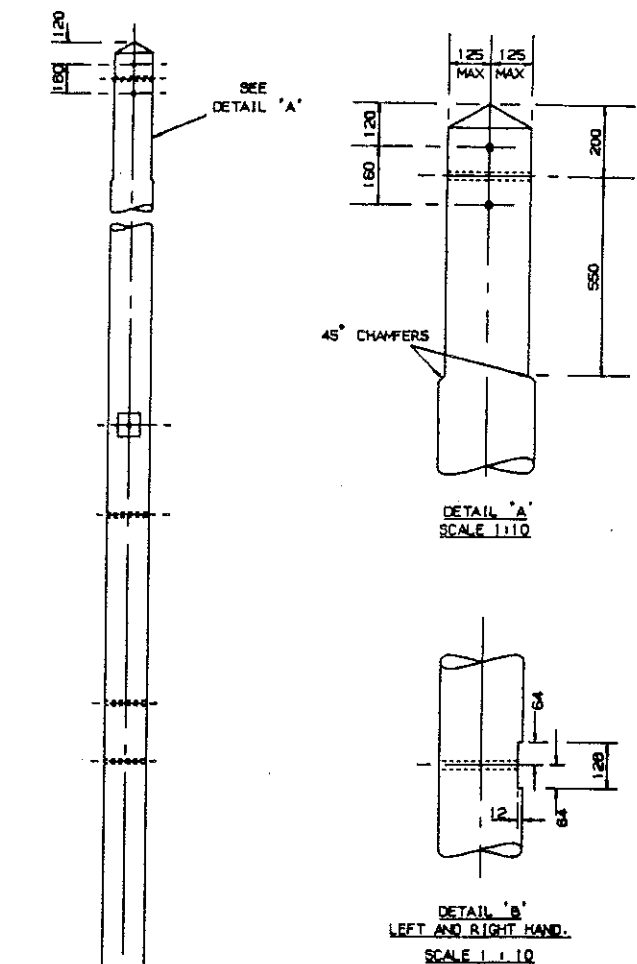


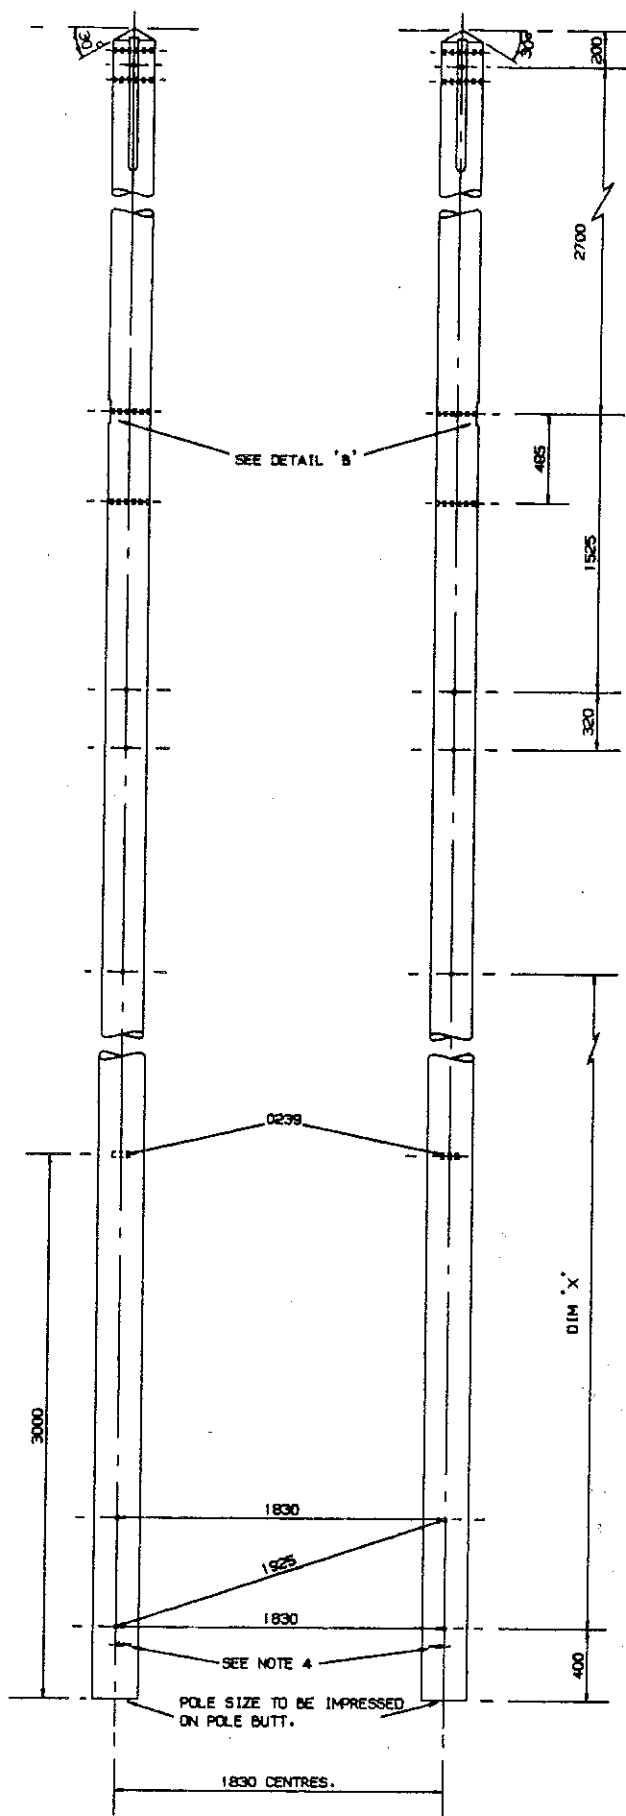

NOTES:

1. MINIMUM POLE LENGTH TO BE 11.5 METRES.
2. CLASS OF POLE TO BE 'STOUT'. POLE LEGS TO BE MATCHED. POLE TOPS TO BE 210mm MINIMUM AFTER FABRICATION.
3. ALL HOLES TO BE 22mm DIA. DRILLED AT RIGHT ANGLES TO VERTICAL CENTRE LINE OF POLE. ALL DRILLING AND CUTTING TO BE DONE STRICTLY TO TEMPLATE PRIOR TO CREOSOTING.
4. 50 X 6 X 6 DEEP ARROW MARK POINTING TOWARDS OPPOSITE POLE LEG TO BE GOUGED ON EACH POLE LEG.

POLE LENGTH m	DIM 'X' mm
11.5	5170
12.0	5670
13.0	6670
14.0	7670
15.0	8670
16.0	9670

ALL DIMENSIONS SHOWN ARE IN MILLIMETRES UNLESS OTHERWISE STATED.

NORTHERN ELECTRIC 		Operations Director's Dept., Central House Newcastle-upon-Tyne NE1 5NE H.V. OVERHEAD LINES. DRILLING, SCARFING AND MARKING FOR 'H' TERMINAL SUPPORT. SEE SHEET 4.	
Drawn J.A.B. Checked G.M.H.	Traced Date Issued DEC 89	Org. No. 1 00 043 4011	Sheet No. 5 No. of Sheets Scale 1:20 & 1:10