


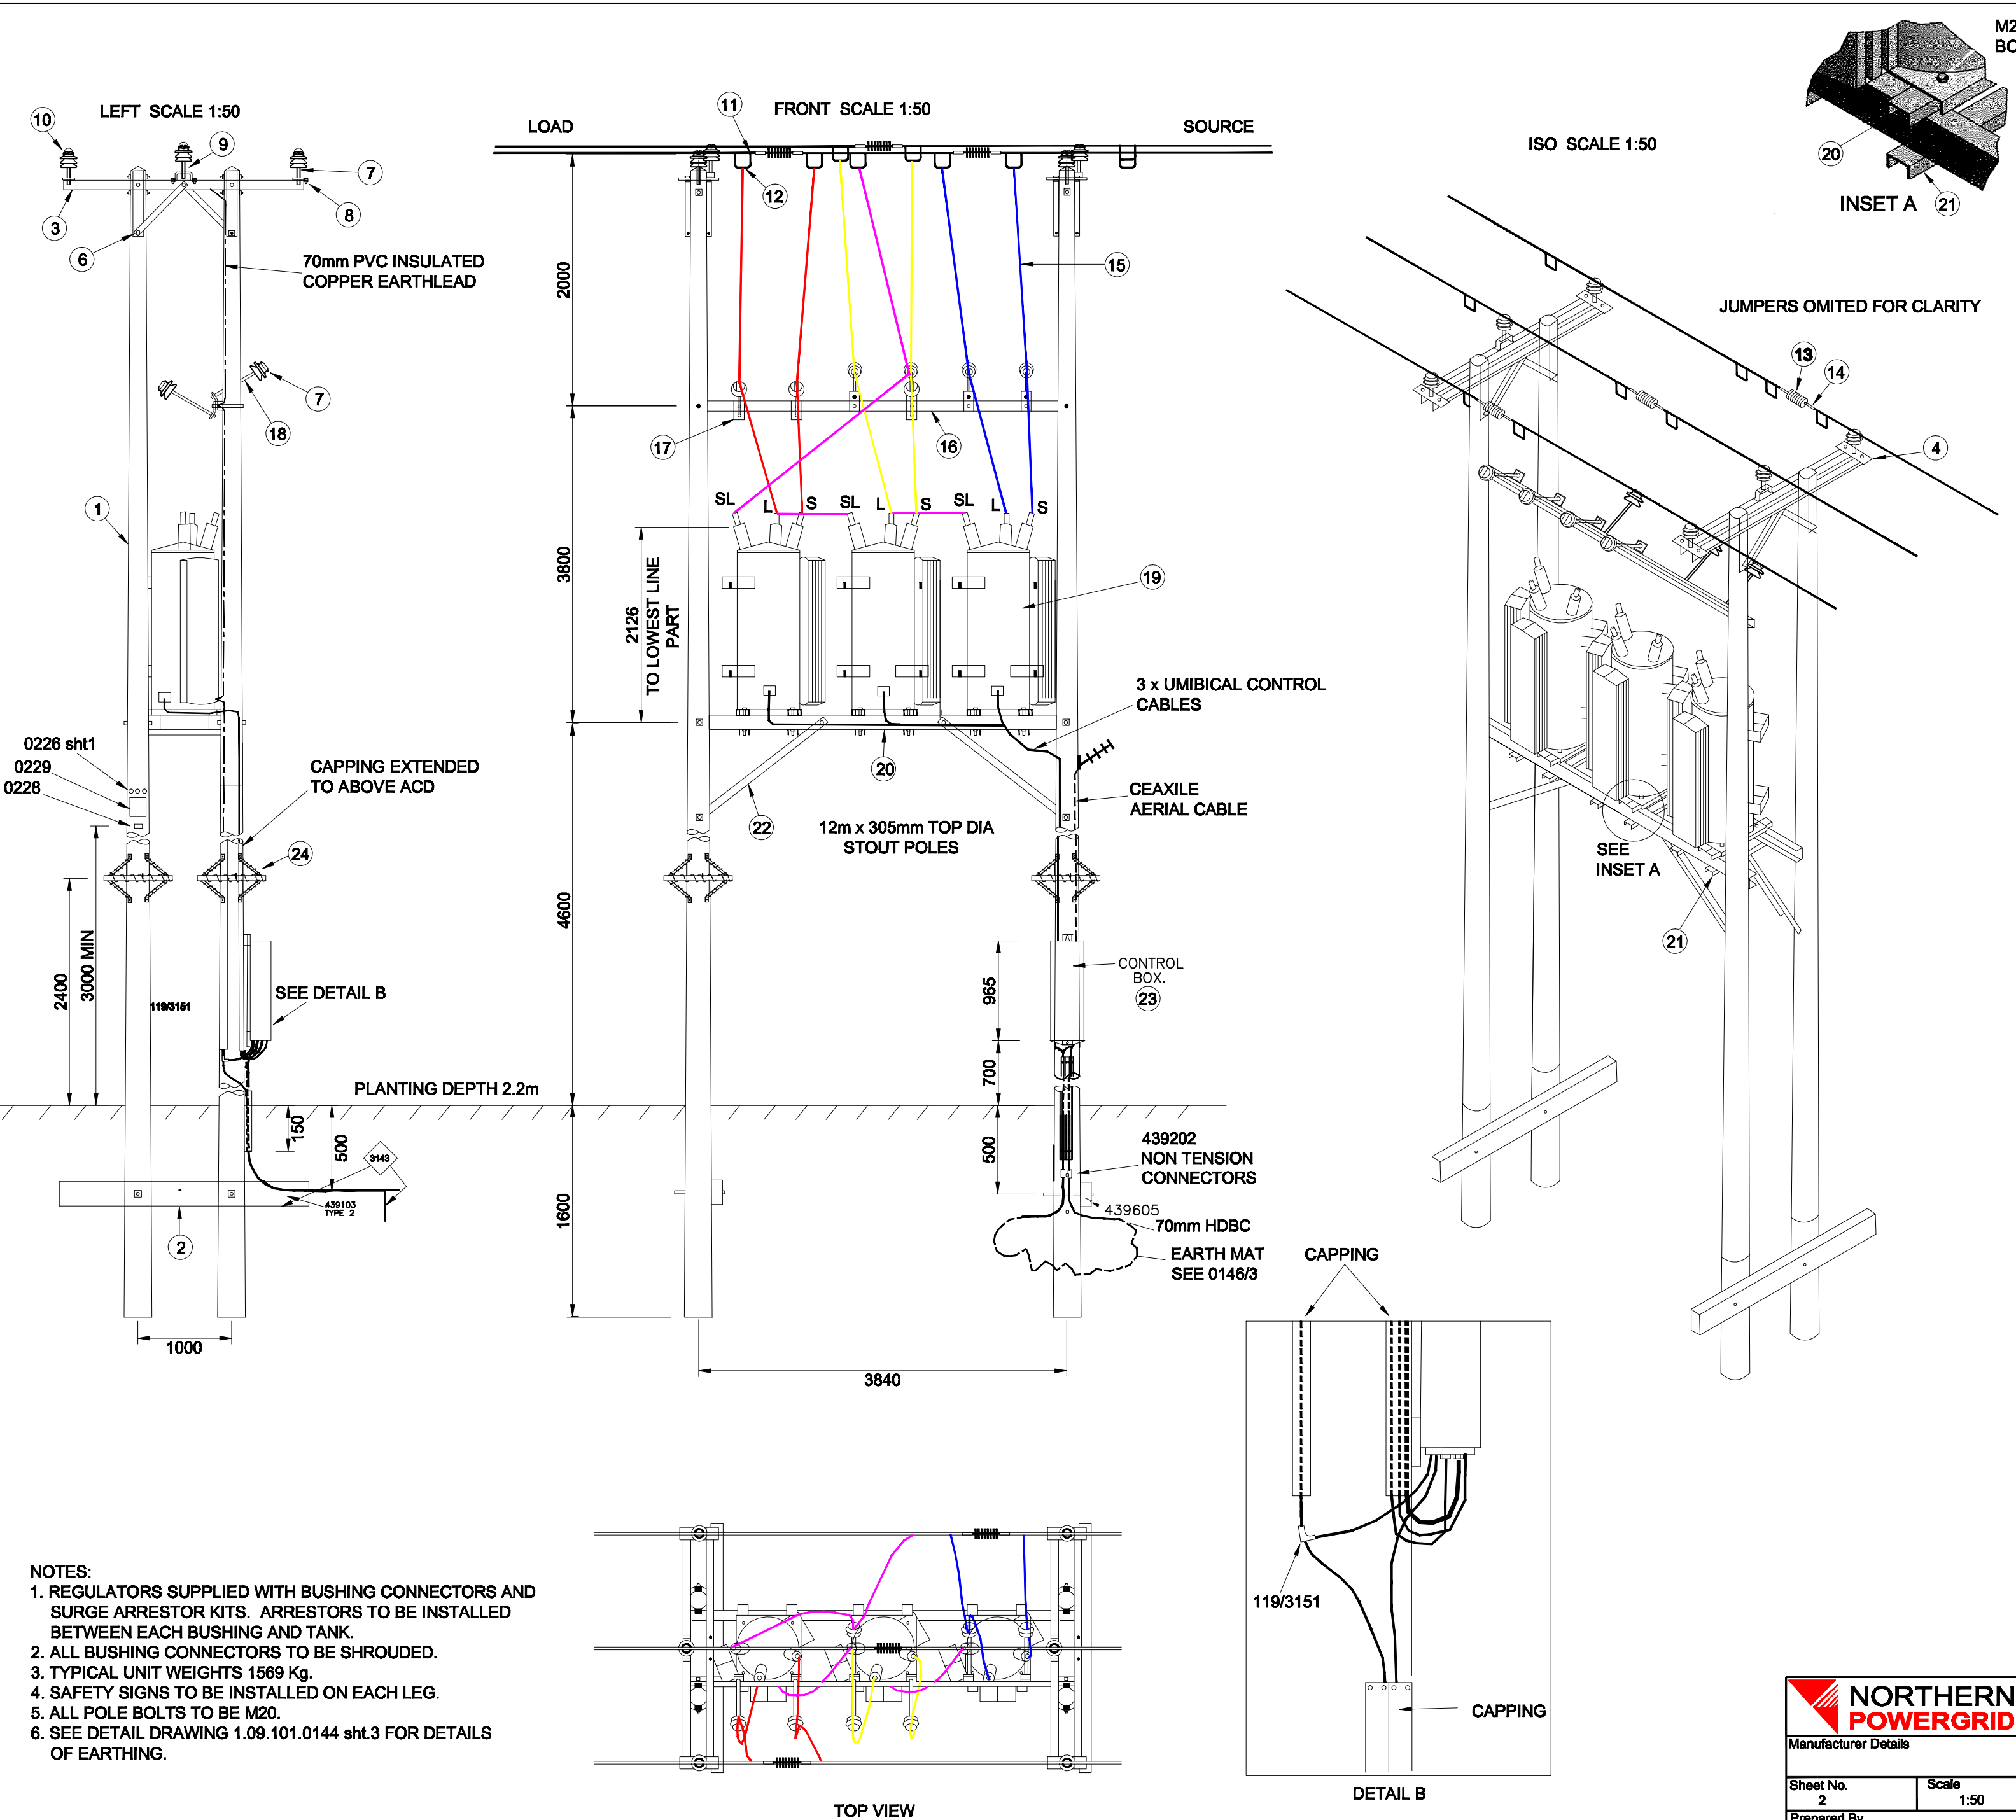

NOTES:
1. REGULATORS SUPPLIED WITH BUSHING CONNECTORS AND SURGE ARRESTOR KITS. ARRESTORS TO BE INSTALLED BETWEEN EACH BUSHING AND TANK.
2. ALL BUSHING CONNECTORS TO BE SHROUDED.
3. TYPICAL UNIT WEIGHTS 1569 Kg.
4. SAFETY SIGNS TO BE INSTALLED ON EACH LEG.
5. ALL POLE BOLTS TO BE M20.
6. SEE DETAIL DRAWING 1.09.101.0144 sht.3 FOR DETAILS OF EARTHING.

Item	Qty	Cat Number	Description	Drg Number
Pole And Founds				
1	1	233401	4 Pole H Arrangement for Pole mounted Regs	1091080800 sht.5
2	2	234704	Foundation Blocks - 1830mm - to be drilled at 1.0m centres	439112 sht.2
-	4	372815	Bolts, M20 x 530 XOX (Stout)	n/a
-	4	368063	Washer, Square, Flat	0183/6
-	4	368078	Washer, Square, Curved	439605
Crossarm Assembly				
3	4	251470	Intermediate Crossarm	439557
4	4	237609	Section Strap	439525
5	2	237539	Insulator Bracket	439518
6	4	237581	Crossarm Strut	439526
-	8	378794	Bolts, M20 x 300 (Stout)	n/a
-	14	378794	Bolts, M20 x 60	n/a
-	2	370504	Bolts, M20 x 60 (Earthing)	n/a
-	22	375616	Washers, Round, M20	n/a
Pin Insulators (as specified)				
7	6	253777 or	50kV Rating (11 and 20 kV)	n/a
7	6	253833	55kV Rating (20kV earthen poles)	n/a
8	4	261824	Insulator pins - 10kn - 230mm stalk	0527/1
9	2	261843	Insulator pins - 10kn - 305mm stalk	0527/2
10	6	to suit	Distribution Ties	660
Line connections				
11	7	268541	Live Line Bail	120/0012
12	7	268999	Live Line tap	121/0024
13	3	216135	11kV Live Line Section Insulator or	0485/9
13	3	253706	20kV Live Line Section Insulator	tba
14	6	To Suit	Compression Deacend	0102/10
15	35m	224808	70mm PVC Insulated Flexible Jumpers	n/a
Jumper Supports				
16	2	337073	Pilot Pin Support Channel - see kit	1091080800 sht.3 item 2
17	7	227074	39 deg. pilot mounting Brackets	1091080800 sht.4
-	2	378794	Bolts, M20 x 300 (Stout)	n/a
-	2	368078	Washer, Square, Curved	439605
-	16	375616	Washers, Round, M20	n/a
18	7	261909	Pilot Pins	0619/1
Pin Insulators (as specified)				
7	7	253777 or	50kV Rating (11 and 20 kV)	n/a
7	7	253833	55kV Rating (20kV earthen poles)	n/a
10	7	to suit	Distribution Ties	660
Voltage Reg support Steelwork				
19	3	to suit	Voltage regulators	n/a
20	2	see 337073	Voltage reg Support channel - see kit	1091080800 sht.3 item 1
21	12	see 337073	Voltage Reg Clamp Channel - see kit	1091080800 sht.3 item 4
22	4	see 337073	Voltage reg support channel strut - see kit	1091080800 sht.3 item 3
Voltage reg control Unit				
-	2	370504	Bolts, M20 x 60 (Earthing)	n/a
-	14	378794	Bolts, M20 x 300 (Stout)	n/a
-	14	375616	Washers, Round, M20	n/a
Earthing / Bonding				
6m	28258	70mm PVC Insulated Earthing Lead	n/a	
20m		70mm HDDB conductor - earth grading conductor	n/a	
5m	28241	32mm PVC Insulated Earthing Lead	n/a	
6	260376	Polyprop Clips - 70mm Earth Lead	119/3112	
15	248815	Polyprop Clips - 32mm Earth Lead	119/3112	
9	268842	Lug VPCL1.3 (14)	237	
4	370491	Bolt, M12x 40, Galvd (Earthing)	0162/2	
1	268804	Compression L tap	119.3151/2	
2	235548	Earthwire Casing	0149/3	
24	371738	Screw Nails 50mm x no10		
5	354249	Earth Rod	119.3143/1	
5	354338	Saddle Clamp	119.3143/2	
Anticlimbing Guard				
4	251362	Pre-wrapped Anti-climbing Guard	0408/8	
Notices				
	To suit	Number Plate	0228 Sht.3	
	243258	Base Plate	-	
4	363318	Safety Sign	229	

Manufacturer Details

Sheet No. 2

Scale 1:50

Prepared By Barbara Gordon

Revised 01/08/15

Date Issued 12/05/15

Grid Reference

Checked By G HAMMEL

Lloyds Court, 78 Grey Street, Newcastle Upon Tyne, NE1 6AF

4 POLE VOLTAGE REGULATOR GENERAL ARRANGEMENT

Type OVERHEAD

Ref No. C1047605

Revision

LINES

Historic Drg.No. 1091080800

Notes

