

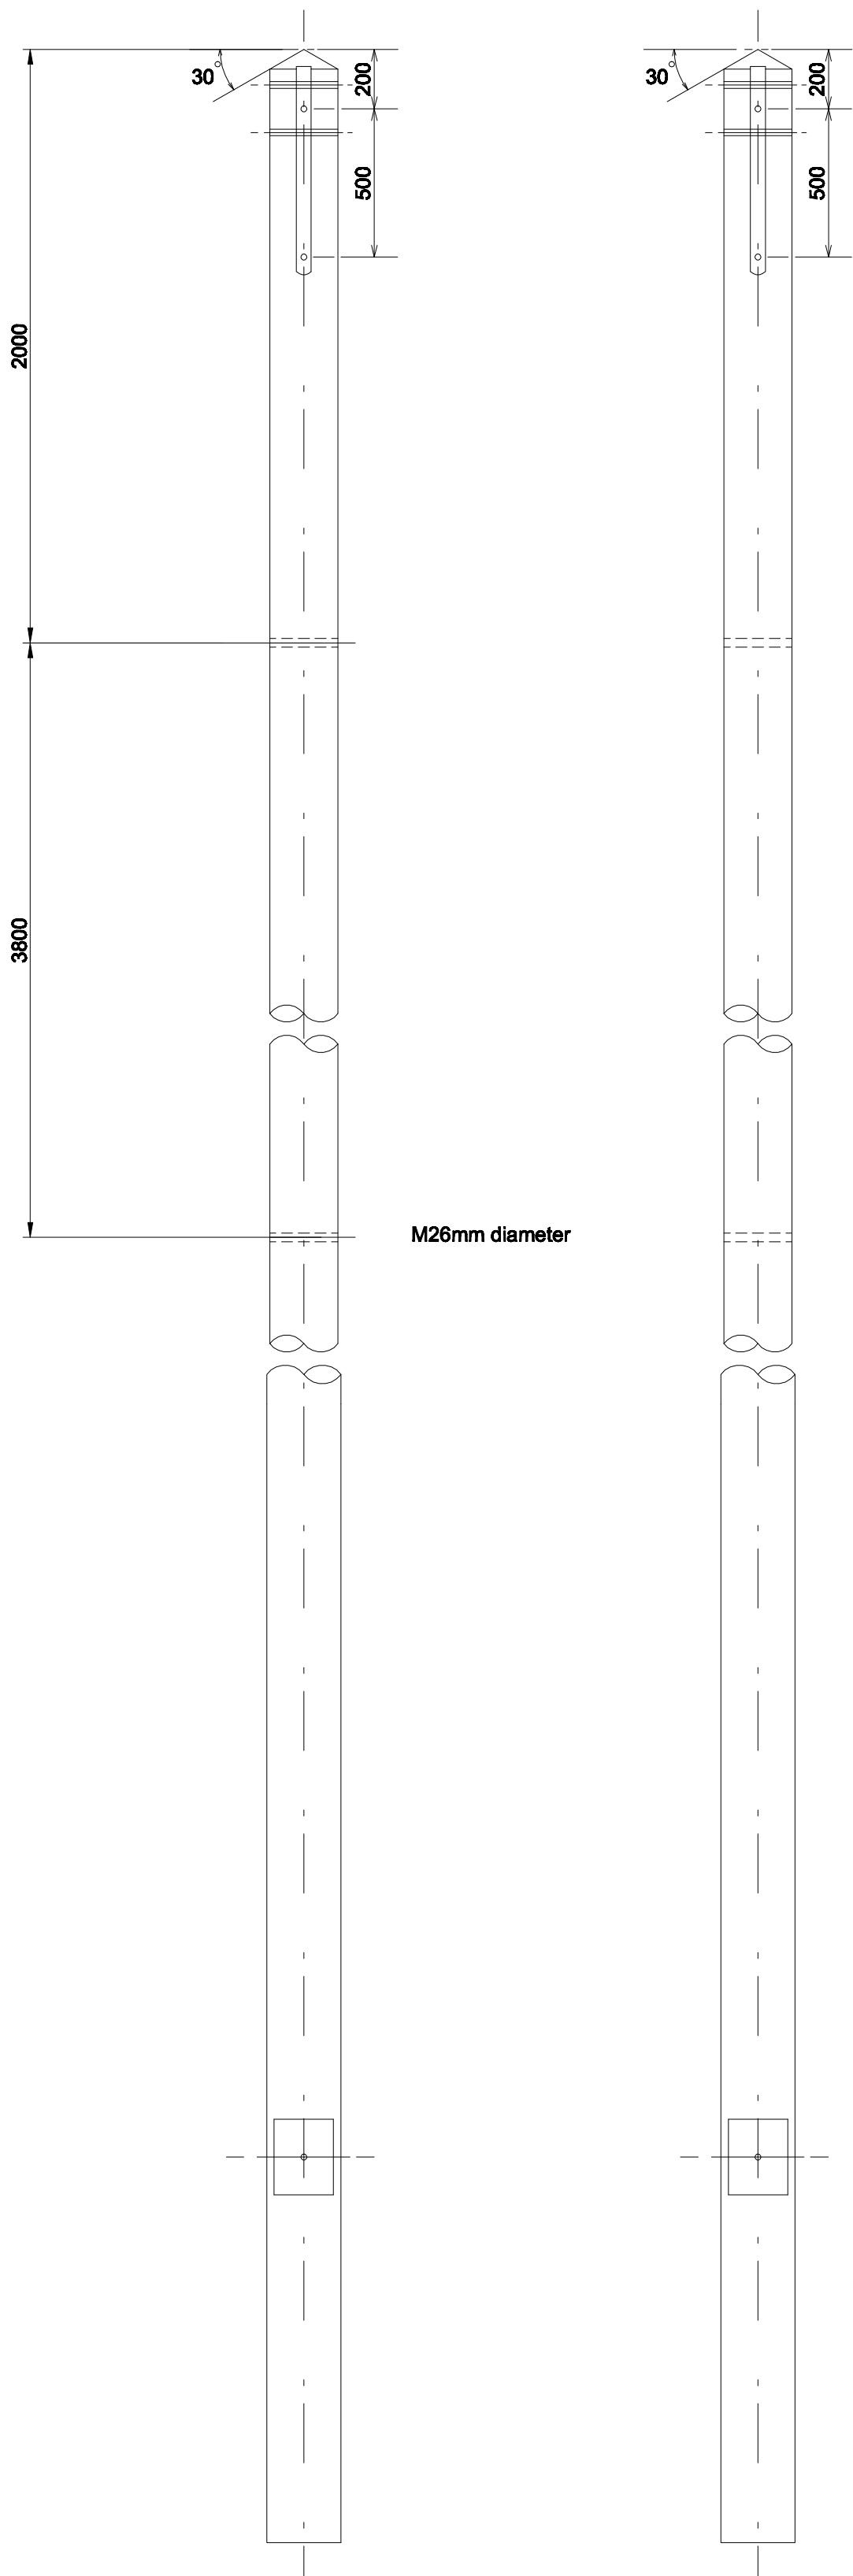


SCARFING TO BE CUT TO GIVE A 50mm WIDE FLAT ON BOTH FACES OF MEDIUM AND STOUT POLES. THE ENDS CHAMFERED OFF AS SHOWN.

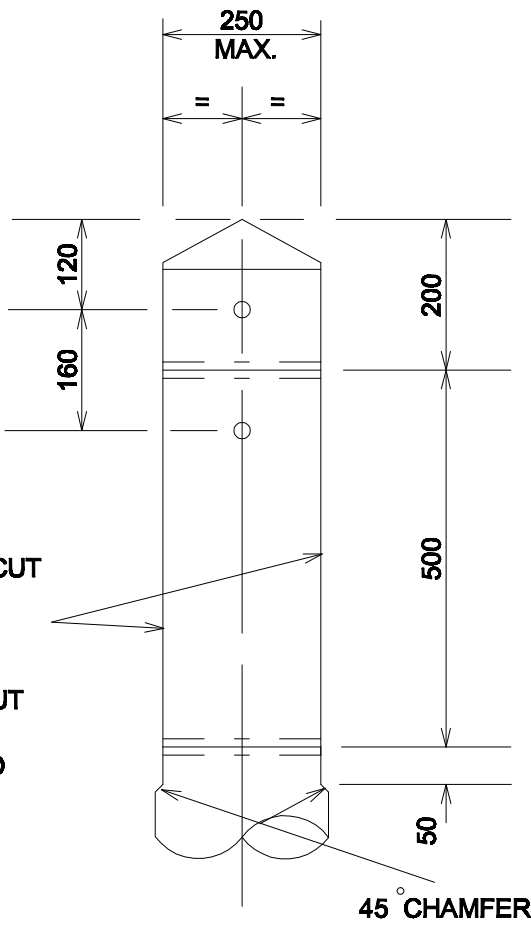

DETAIL A
SCALE 1:10

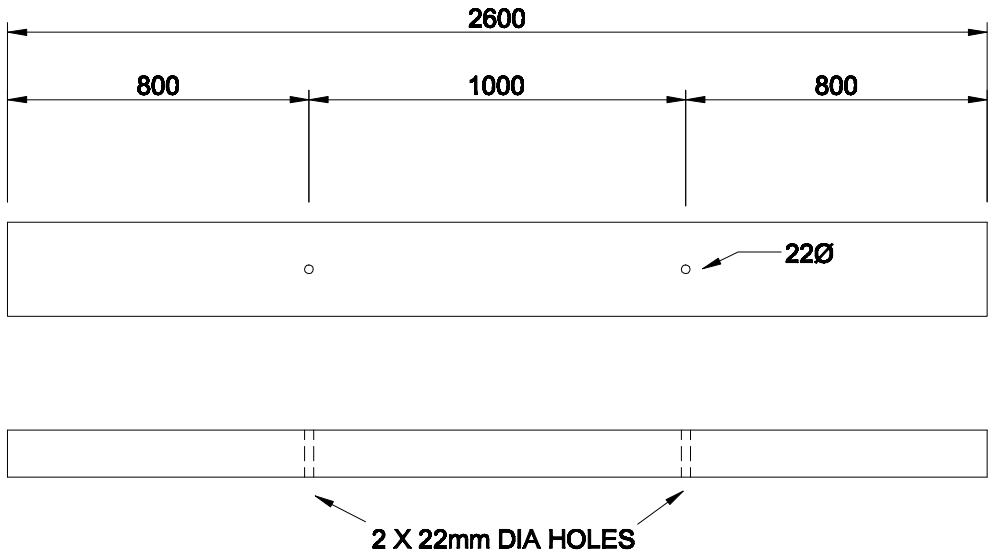

- NOTES:
1. CLASS OF POLE TO BE STOUT.
 2. STANDARD POLE HEIGHT 12m.
 3. ALL HOLES TO BE 22mm DIA, DRILLED AT RIGHT ANGLES TO VERTICAL CENTRE LINE OF POLE. ALL DRILLING AND CUTTING TO BE DONE STRICTLY TO TEMPLATE PRIOT TO CREASOTE PRESERVATION TREATMENT.
 4. PULL BOLT TO BE CUT AT RIGHT ANGLES TO AXIS OF POLE.
 5. POLE TO BE NOTCHED AND DRILLED FOR BLOCKS.
 6. A SINGLE STRUCTURE WILL CONSIST OF 2 x 1m CENTRED 'H' MATCHED POLES PLUS TWO WOOD BLOCKS.

POLE SIZE TO BE IMPRESSED ON POLE BUTT.

ALL DIMENSIONS IN MILLIMETRES UNLESS OTHERWISE STATED



Manufacturer Details	
Sheet No. 5	Scale 1:20
Prepared By Barbara.Rimmer	
Revised 24/01/18	Grid Reference
Date Issued 02/06/15	Checked By G HAMMEL

Lloyds Court, 78 Grey Street, Newcastle Upon Tyne, NE1 6AF			
4 POLE VOLTAGE REGULATOR FABRICATION DRAWING			
Type	OVERHEAD	LINES	
Ref No.	C1048468	Historic Drg.No.	1091080800
Revision	B	Notes	