


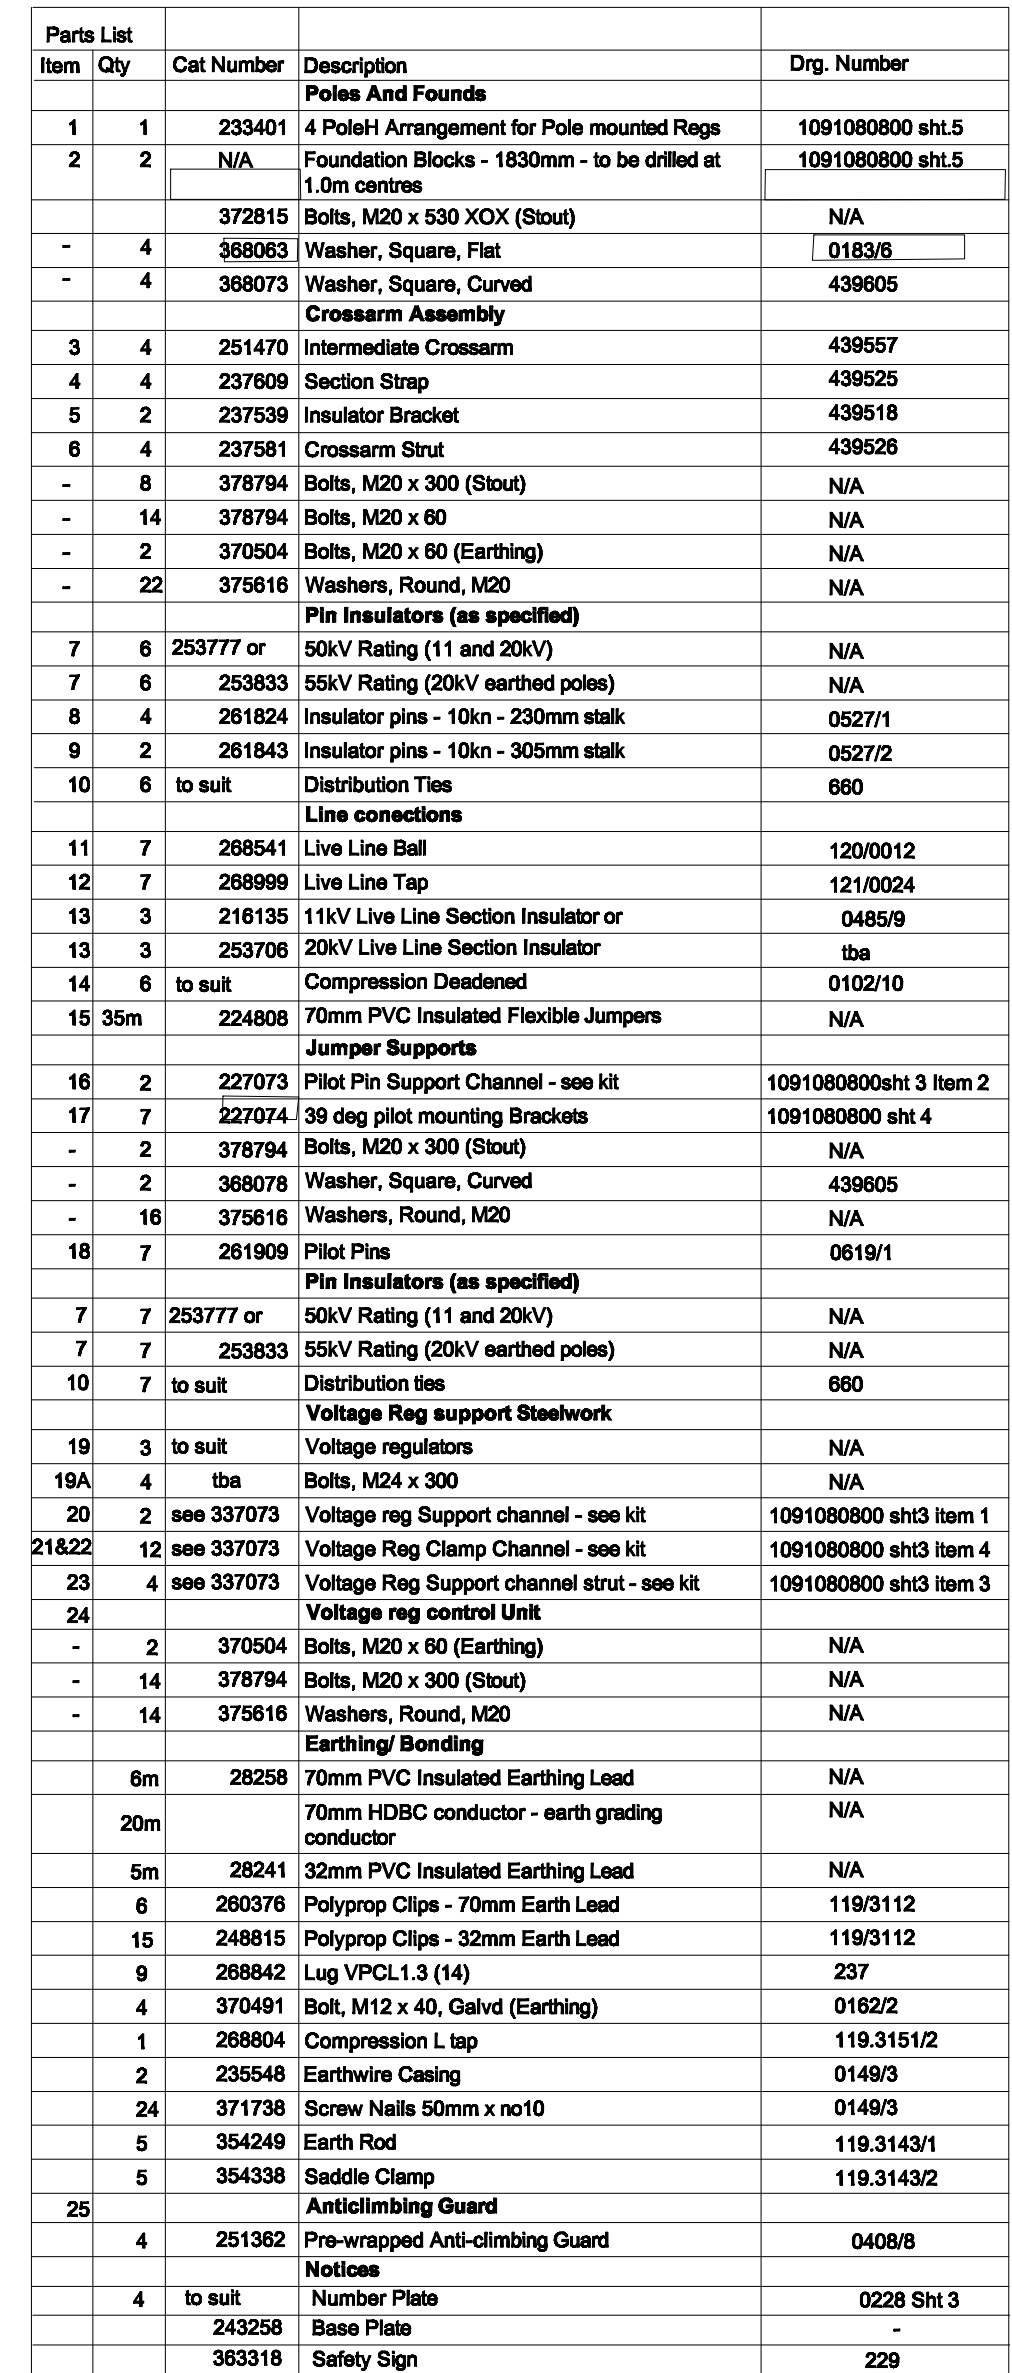

Lloyds Court, 78 Grey Street, Newcastle Upon Tyne, NE1 6AF			
4 POLE VOLTAGE REGULATOR GENERAL ARRANGEMENT 11KV 300 & 400A OR 20KV 200 & 300A			
Type			
OVERHEAD		LINES	
Ref No.	C1085082	Historic Drg. No.	1091080800
Revision	Notes		