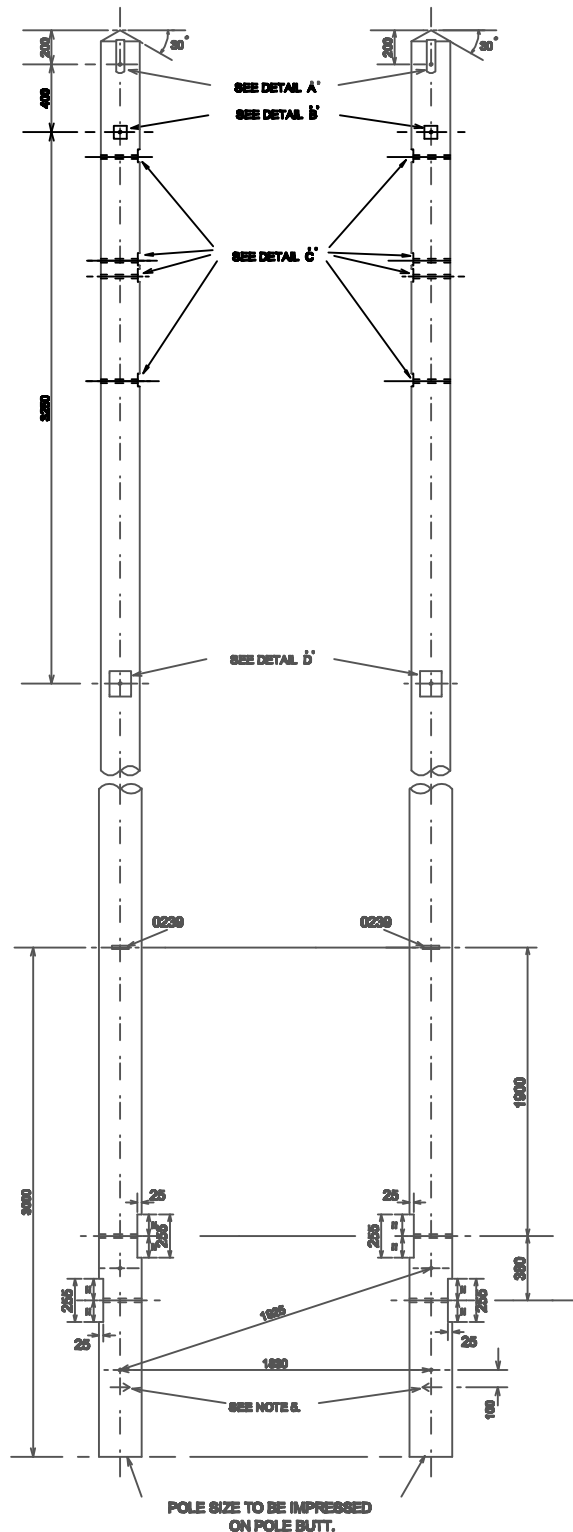
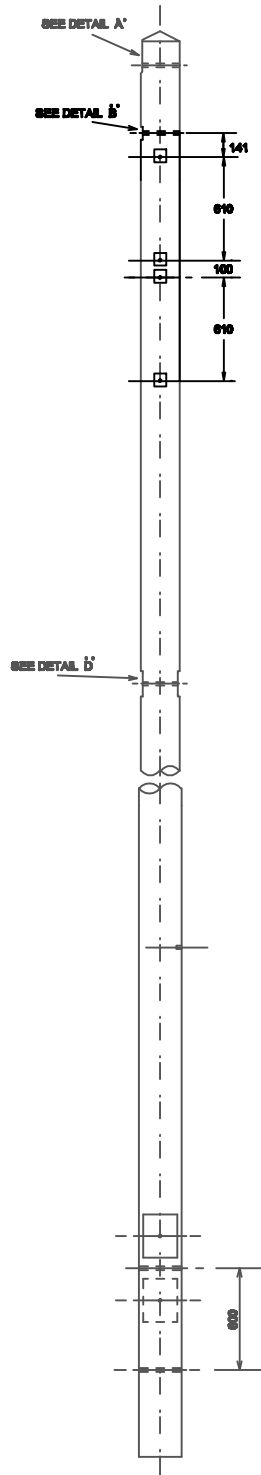


NOTES:

1. POLE LENGTH 11.0m OF STOUT CLAMIFICATION WITH MINIMUM POLE TOP DIAMETER OF 178mm.
2. POLE LEGS TO BE MATCHED.
3. ALL HOLES TO BE 22mm DIA. DRILLED AT RIGHT ANGLES TO VERTICAL CENTRE LINE OF POLE.
4. POLE TO BE NOTCHED AND DRILLED FOR 4 X 250 X 125 X 250 BOLLING.
5. 80 X 6 X 6 DEEP ARROW MARK POINTING TOWARDS OPPOSITE POLE LEG, TO BE MARKED ON THE POLE FACE.

ALL DIMENSIONS SHOWN ARE IN MILLIMETRES UNLESS OTHERWISE STATED.

		Lloyds Court, 78, Grey Street, Newcastle upon Tyne NE1 6AF									
		11KV AND 20KV OVERHEAD LINE									
DRILLING, SCARFING AND MARKING FOR		DRAWING No 1.08.108.0862 SHEET 1 AND 3									
Prepared by J.B.	Drawn by HA.J.	Date FEB 77	Sheet No. 2	Project 23.2.2005	Scale 1:20 & 10						