
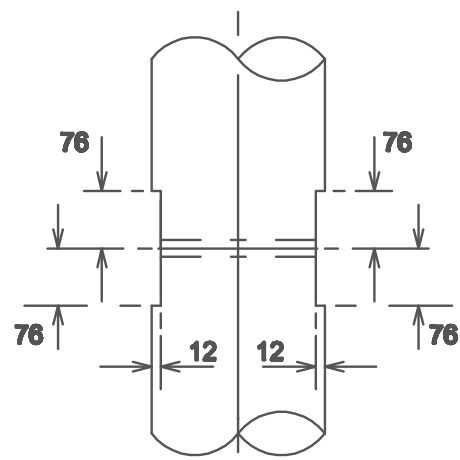



NOTES:

- 1.SHORT LEG - POLE LENGTH 9.0m, CLASSIFIED STOUT.
2. WHEN COMPLETE POLE ARRANGEMENTS TO DRG.No s 0864 SHT.1 & 2 ARE REQUIRED, THE ORDERS SHALL QUOTE FABRICATION TO 1.09.108.0864 SHT.3
3. WHERE A SHORT LEG ONLY IS REQUIRED TO CONVERT EXISTING SINGLE POLE ARRANGEMENTS TO 0864 SHT.1 OR 2, THE ORDERS SHALL QUOTE FABRICATION TO 1.09.108.0864 SHT.3
4. ALL HOLES SHALL BE 22mm DIA, DRILLED AT RIGHT ANGLES TO THE VERTICAL CENTRE LINE. ALL DRILLING AND CUTTING TO BE DONE STRICTLY TO TEMPLATE AND PRIOR TO CREOSOTING.
5. ALL UNUSED POLE BOLT HOLES TO BE PLUGGED.


CAT. No. 237473

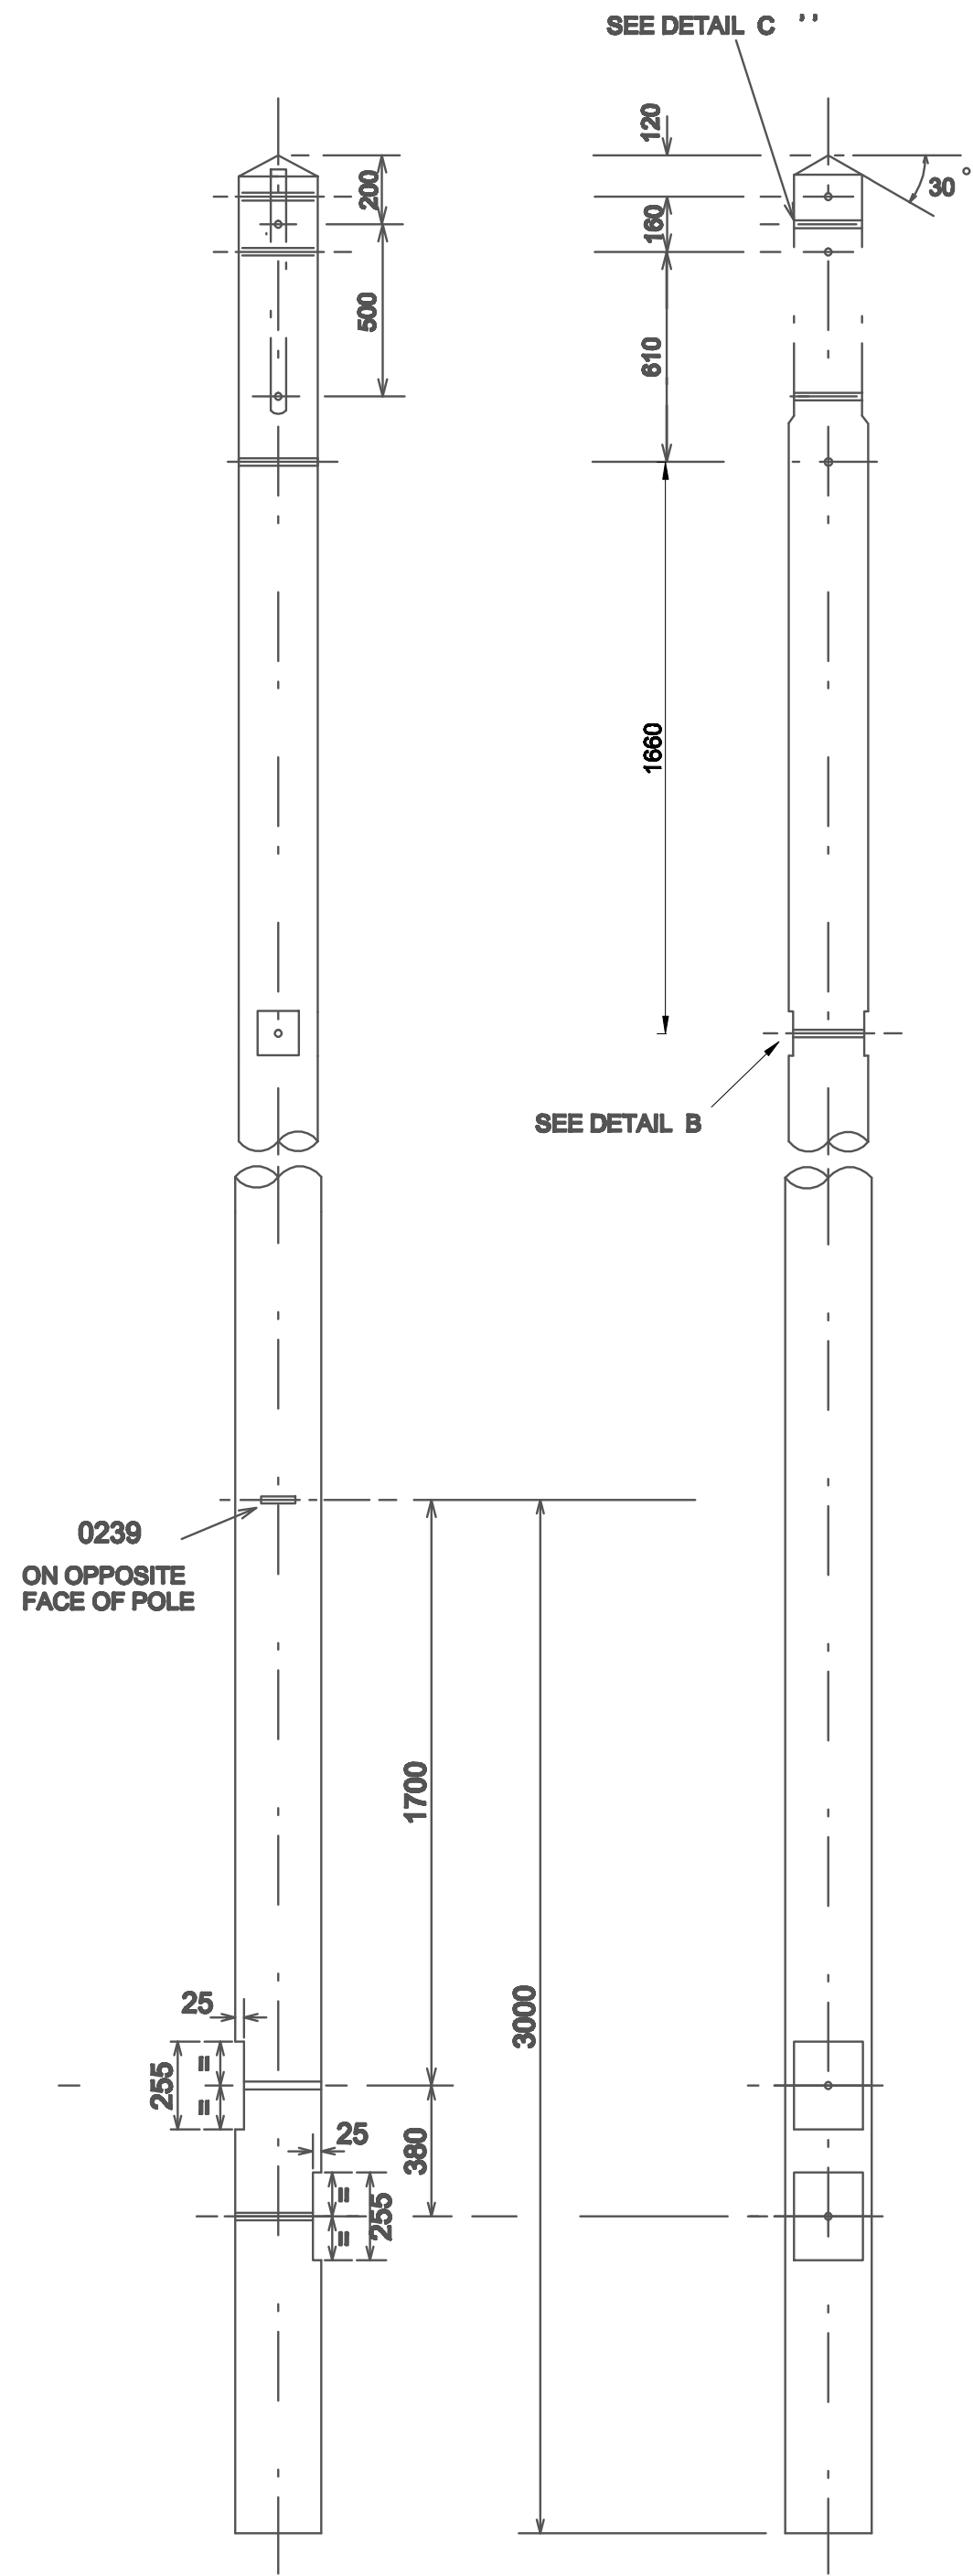

DETAIL B
SCALE 1:10

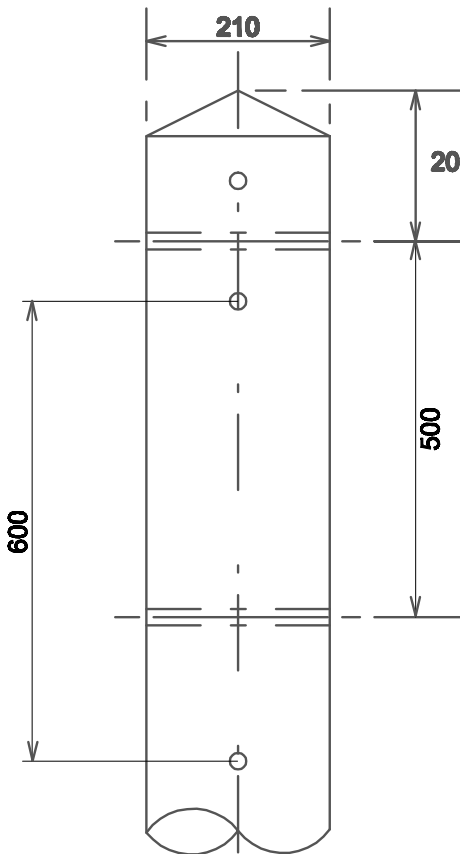

DETAIL C
SCALE 1:10

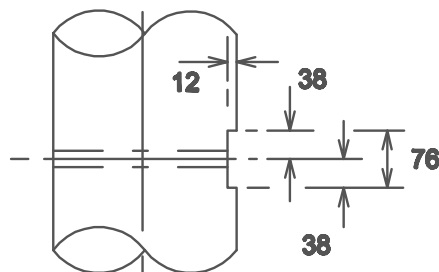

DETAIL D
SCALE 1:10

SHORT LEG

0864 SHEET 1 AND 2

ALL DIMENSIONS SHOWN ARE IN MILLIMETRES UNLESS OTHERWISE STATED.

 NORTHERN GRID Manufacturer Details	Lloyds Court, 78 Grey Street, Newcastle Upon Tyne, NE1 6AF	
	11 AND 20KV OVERHEAD LINES FABRICATION DETAILS FOR DRAWINGS 1.09.108.0864 SHEET 1 AND SHEET 2	
Sheet No. 3	Scale 1:20	Type OVERHEAD LINES
Prepared By Joan.Oakley	Grid Reference	Ref No. C1007482
Revised 16/04/13	Checked By G HAMMEL	Historic Drg.No. 1091080864
Date issued 19/03/12		Revision A Notes