

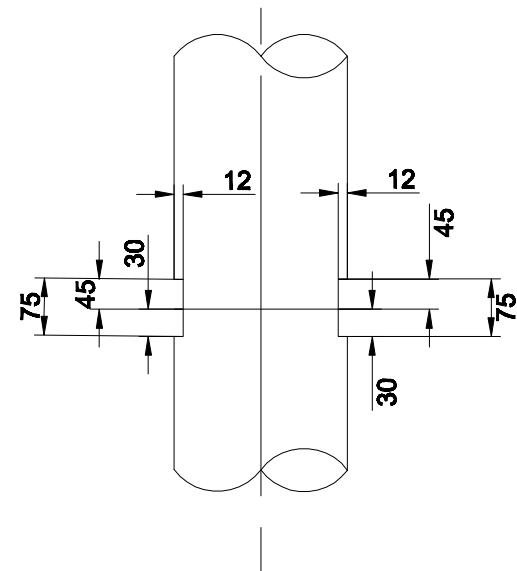


2 - 22mm DIA. HOLES

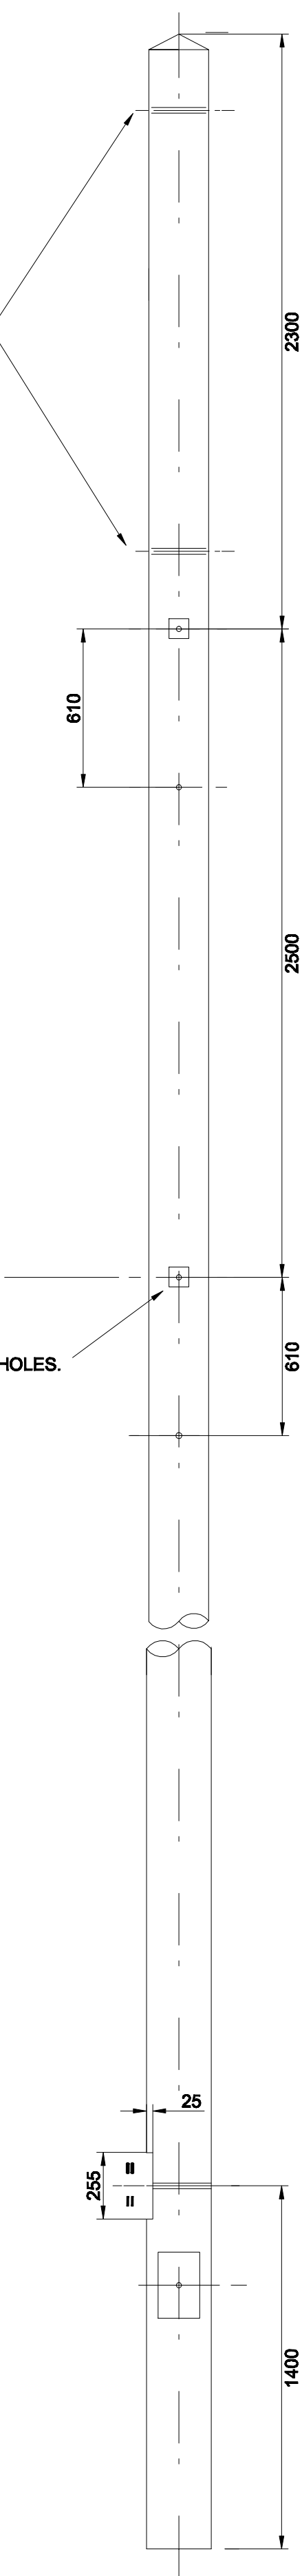

DETAIL 'A'
SCALE 1:10

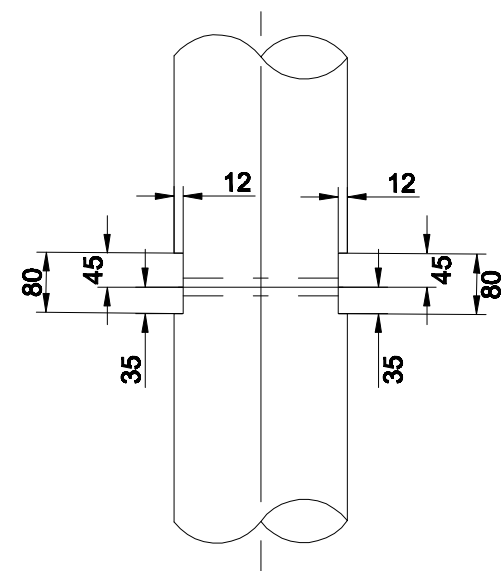

DETAIL 'B'
SCALE 1:10

- NOTES:
- POLE LENGTH 11.0m CLASSIFIED 'STOUT' .
 - UNLESS STATED OTHERWISE, ALL HOLES TO BE 22mm DIA. DRILLED AT RIGHT ANGLES TO THE VERTICAL CENTRE LINE OF THE POLE. ALL DRILLING AND CUTTING TO BE DONE STRICTLY TO TEMPLATE PRIOR TO PRESERVATION TREATMENT.
 - POLE BUTT TO BE CUT AT RIGHT ANGLES TO AXIS OF POLE.
 - POLE TO BE DRILLED AND NOTCHED FOR 250 X 125 BAULKS.

ALL DIMENSIONS SHOWN ARE IN MILLIMETRES UNLESS OTHERWISE STATED.

 NORTHERN POWERGRID		Lloyds Court, 78 Grey Street, Newcastle Upon Tyne, NE1 6AF	
Manufacturer Details		11KV & 20KV OVERHEAD LINES FABRICATION FOR THREE PHASE TOTEM POLE S.S. WITH HV FUSE UNITS & HV SUPPLY OFF U/G CABLE & U/G SUPPLY TO LV NETWORK (1.09.108.0865 SHT1)	
Sheet No. 2	Scale AS SHOWN	Type OVERHEAD STANDARDS	
Prepared By Barbara.Gordon	Grid Reference	Ref No. C996260	Historic Drg.No. 1091080865
Revised 27/07/15	Date Issued 10/03/11	Checked By S SLAKELD	Revision B Notes