


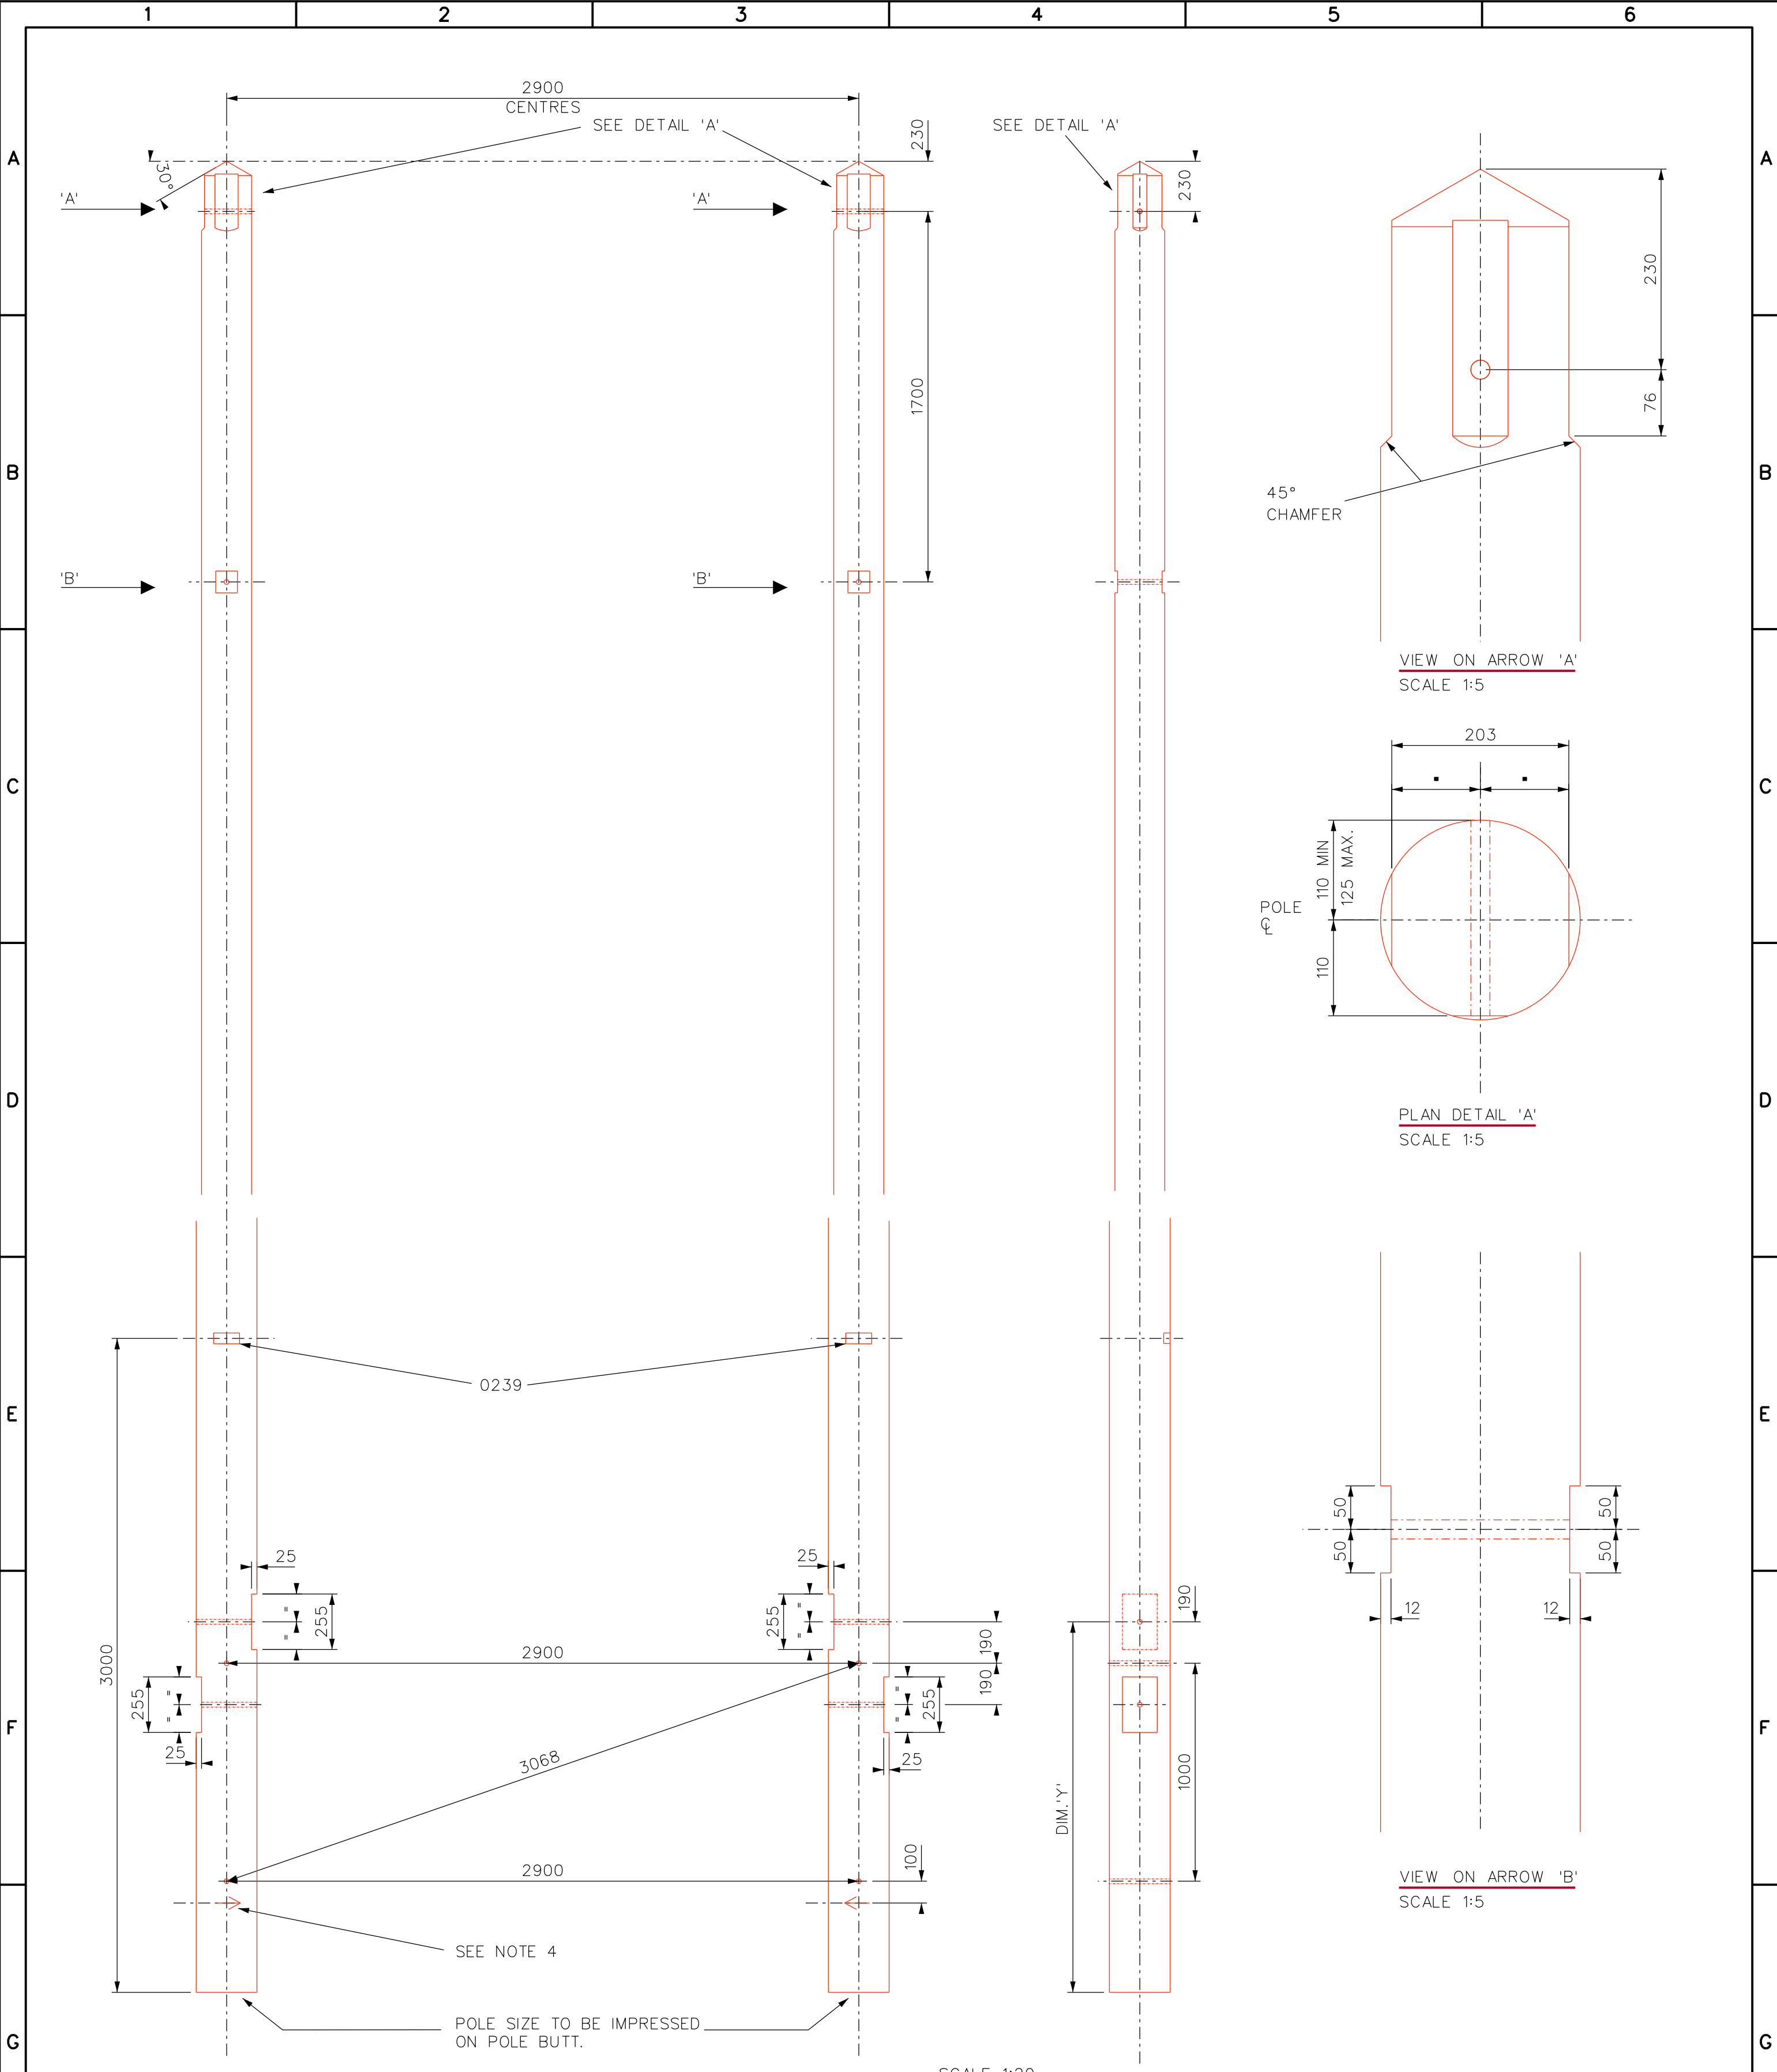

- NOTES:
- POLE LEGS TO BE MATCHED. POLE TOP MINIMUM DIAMETER BEFORE FABRICATION 'STOUT' – 220mm.
 - ALL HOLES TO BE 22mm DIA. DRILLED AT RIGHT ANGLES TO VERTICAL CENTRE LINE OF POLE. ALL DRILLING AND CUTTING TO BE DONE STRICTLY TO TEMPLATE PRIOR TO PRESERVATION TREATMENT.
 - POLE BUTTS TO BE CUT AT RIGHT ANGLES TO AXIS OF POLE. POLES TO BE NOTCHED AND DRILLED FOR DUPLICATE 250 X 125 BAULKS.
 - 50 X 6 X 6 DEEP ARROW MARK POINTING TOWARDS OPPOSITE POLE LEG TO BE GOUGED ON POLE FACE.

POLE LENGTH (m)	DIM 'Y' (mm)
13 – 15 INCLUSIVE.	1700
16 – 18 INCLUSIVE.	1900
20	2500

ALL DIMENSIONS SHOWN ARE IN MILLIMETRES UNLESS OTHERWISE STATED.

**NORTHERN
POWERGRID**

Manufacturer Details

Sheet No.
2

Scale
AS SHOWN

Prepared By
W7Brian.James

Modified
22/03/2023

Created

Grid Reference

Checked By
G HAMMEL

Lloyds Court, 78 Grey Street, Newcastle Upon Tyne, NE1 6AF

33KV OVERHEAD LINES STRAIGHT LINE DC WOOD H POLE
DRILLING, SCARFING AND MARKING
2900 CENTRES POLE FABRICATION

ISO A2

C.A.D

Document Details

Drawing No.
C115998

Revision

LEGACY OTHER

Historic Drawing No.
1091161151

Copyright of Northern Powergrid Holding Company. No part of this drawing to be reproduced without prior permission.