


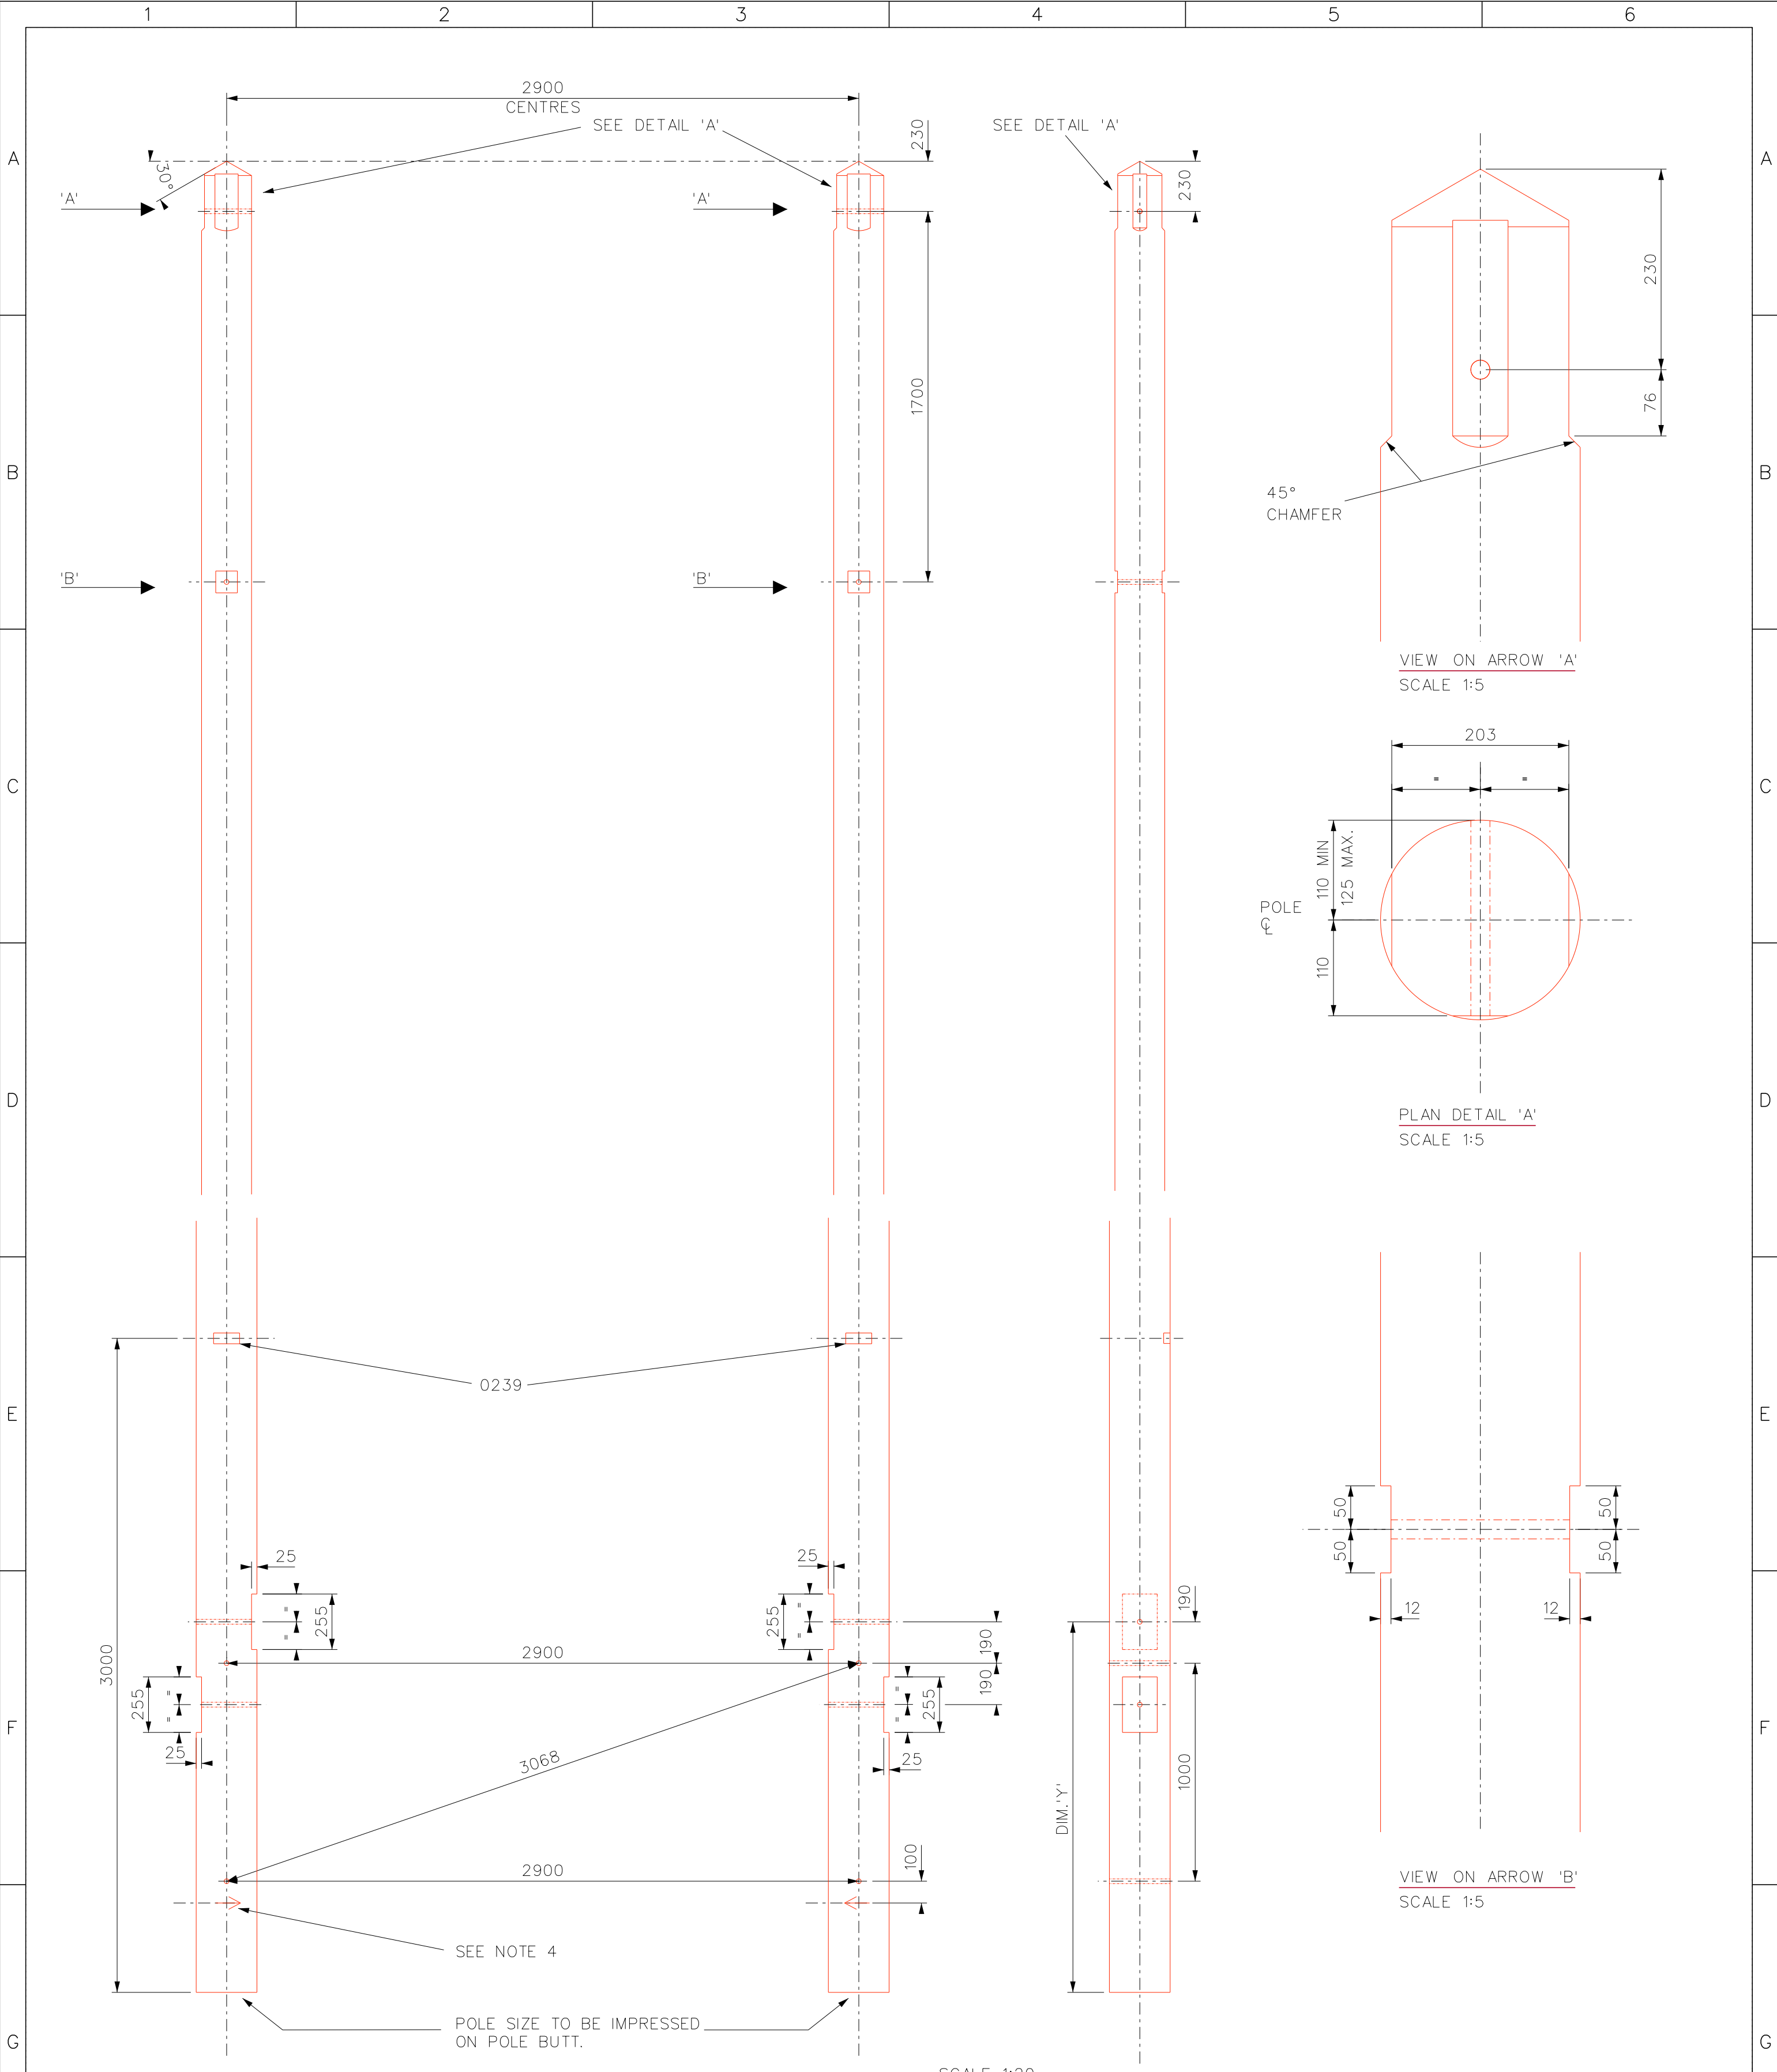

- NOTES:
- POLE LEGS TO BE MATCHED. POLE TOP MINIMUM DIAMETER BEFORE FABRICATION 'STOUT' – 220mm. **'EXTRA STOUT' - 250MM**
 - ALL HOLES TO BE 22mm DIA. DRILLED AT RIGHT ANGLES TO VERTICAL CENTRE LINE OF POLE. ALL DRILLING AND CUTTING TO BE DONE STRICTLY TO TEMPLATE PRIOR TO PRESERVATION TREATMENT.
 - POLE BUTTS TO BE CUT AT RIGHT ANGLES TO AXIS OF POLE. POLES TO BE NOTCHED AND DRILLED FOR DUPLICATE 250 X 125 BAULKS.
 - 50 X 6 X 6 DEEP ARROW MARK POINTING TOWARDS OPPOSITE POLE LEG TO BE GOUGED ON POLE FACE.

POLE LENGTH (m)	DIM 'Y' (mm)
13 – 15 INCLUSIVE.	1700
16 – 18 INCLUSIVE.	1900
20	2500

12 and below DIM 'Y' = 1500mm

ALL DIMENSIONS SHOWN ARE IN MILLIMETRES UNLESS OTHERWISE STATED.

		Lloyds Court, 78 Grey Street, Newcastle Upon Tyne, NE1 6AF	
Manufacturer Details		33KV OVERHEAD LINES STRAIGHT LINE DC WOOD H POLE DRILLING, SCARFING AND MARKING 2900 CENTRES POLE FABRICATION	
Sheet No. 2	Scale AS SHOWN	ISO A2 C.A.D	
Prepared By W7Brian.James		Document Details	
Modified 22/03/2023	Grid Reference	Drawing No. C115998	Legacy Other Historic Drawing No. 1091161151
Created	Checked By G HAMMEL	Revision	Notes